
Revisión 27/10/2026 · cd2850e7 | Modelo y propuesta de coordinación - comprobar en sitio

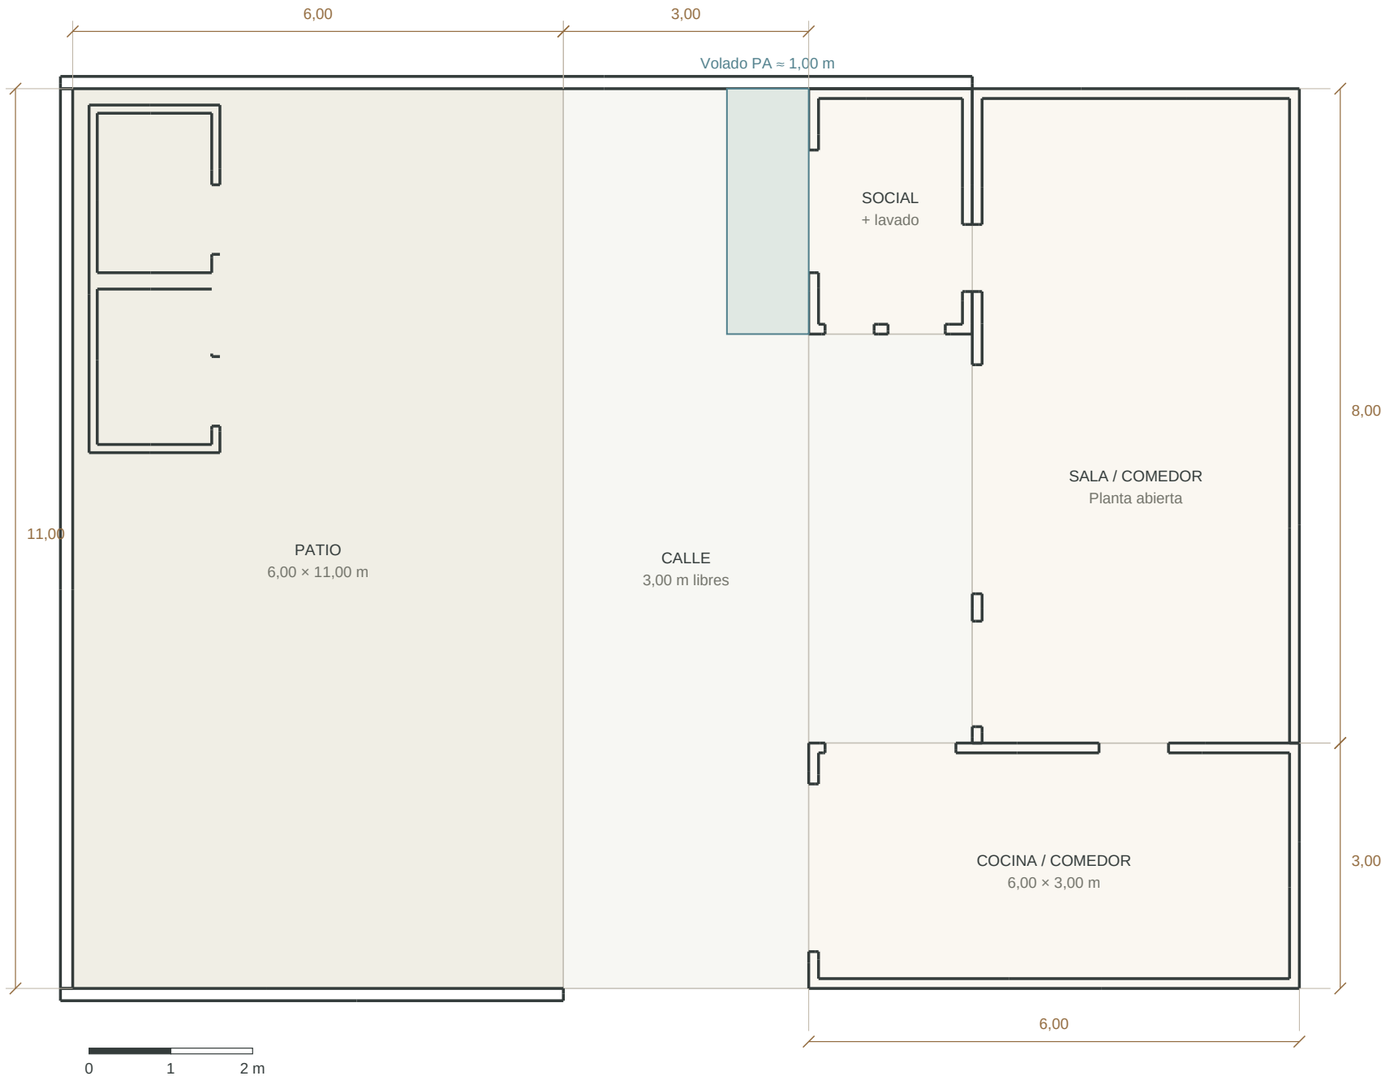

FRENTE / LLEGADA DESDE LA CALLE

ESCALA 1:75 / A3 AL 100 %

No ajustar a página. Comprobar escala gráfica.

Patio
6,00 × 11,00 m
Modelo · verificar en sitio

Calle de acceso
3,00 m de ancho
Confirmado por el usuario; comprobar replanteo.

Cocina / comedor
6,00 × 3,00 m
Modelo · verificar en sitio

Cuerpo de dos pisos
4,00 × 8,00 m
Modelo · verificar en sitio

Baño social / lavado
2,00 × 3,00 m
Modelo · verificar en sitio

Baño principal PA
3,00 × 3,00 m
Modelo · verificar en sitio

NOTAS PARA REPLANTEO


Cotas arquitectónicas del modelo; comprobar medidas libres y espesores en sitio.

Lavandería dentro del baño social. El frente de 6 × 3 m es cocina y comedor.

Giro redondo de gradas: 13 contrahuellas y seis peldaños compensados provisionales.

No usar los planos históricos de la escalera en C ni la antigua división de lavandería.

Revisión 27/10/2026 · cd2850e7 | Modelo y propuesta de coordinación - comprobar en sitio

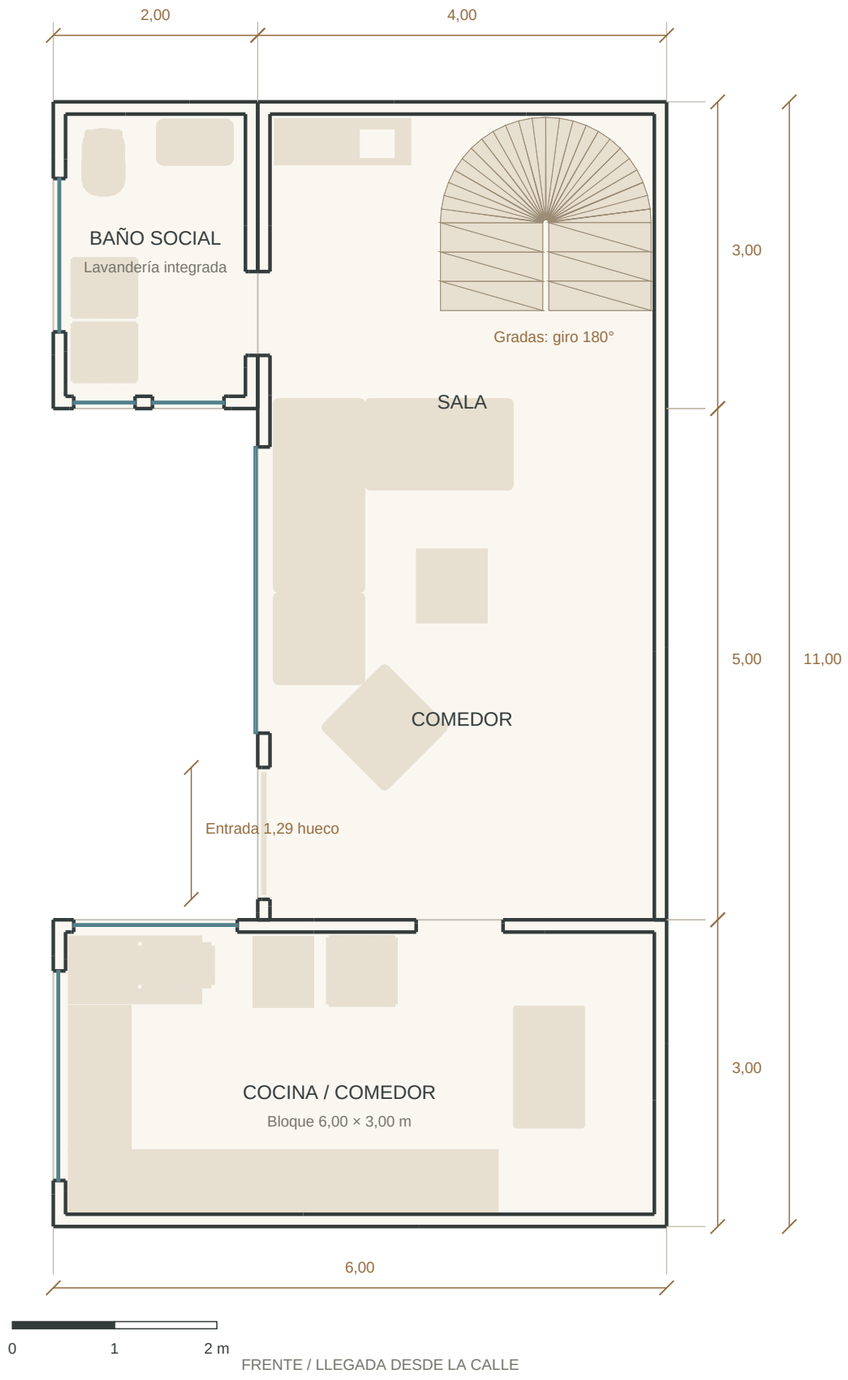

FRENTE / LLEGADA DESDE LA CALLE

ESCALA 1:60 / A3 AL 100 %

No ajustar a página. Comprobar escala gráfica.

Cocina / comedor
6,00 × 3,00 m
Dimensión exterior, sin antigua división de lavandería.

Sala / comedor abierto
4,00 × 8,00 m
Sin tabique entre sala y comedor.

Social con lavado
2,00 × 3,00 m
Lavadora y secadora lado a lado.

Piso cocina
-0,15 m
Desnivel respecto a sala; verificar nivel real.

Entrada de una hoja
1,20 × 2,10 m objetivo
Apertura exterior. Hueco 1,29 × 2,15 m por verificar: cielo interior a 2 m.

Altura sala
2,00 m aprox.
Cara inferior del cielo modelado; verificar vigas.

NOTAS PARA REPLANTEO


Cotas arquitectónicas del modelo; comprobar medidas libres y espesores en sitio.

Lavandería dentro del baño social. El frente de 6 × 3 m es cocina y comedor.

Giro redondo de gradas: 13 contrahuellas y seis peldaños compensados provisionales.

No usar los planos históricos de la escalera en C ni la antigua división de lavandería.

Revisión 27/10/2026 · cd2850e7 | Modelo y propuesta de coordinación - comprobar en sitio

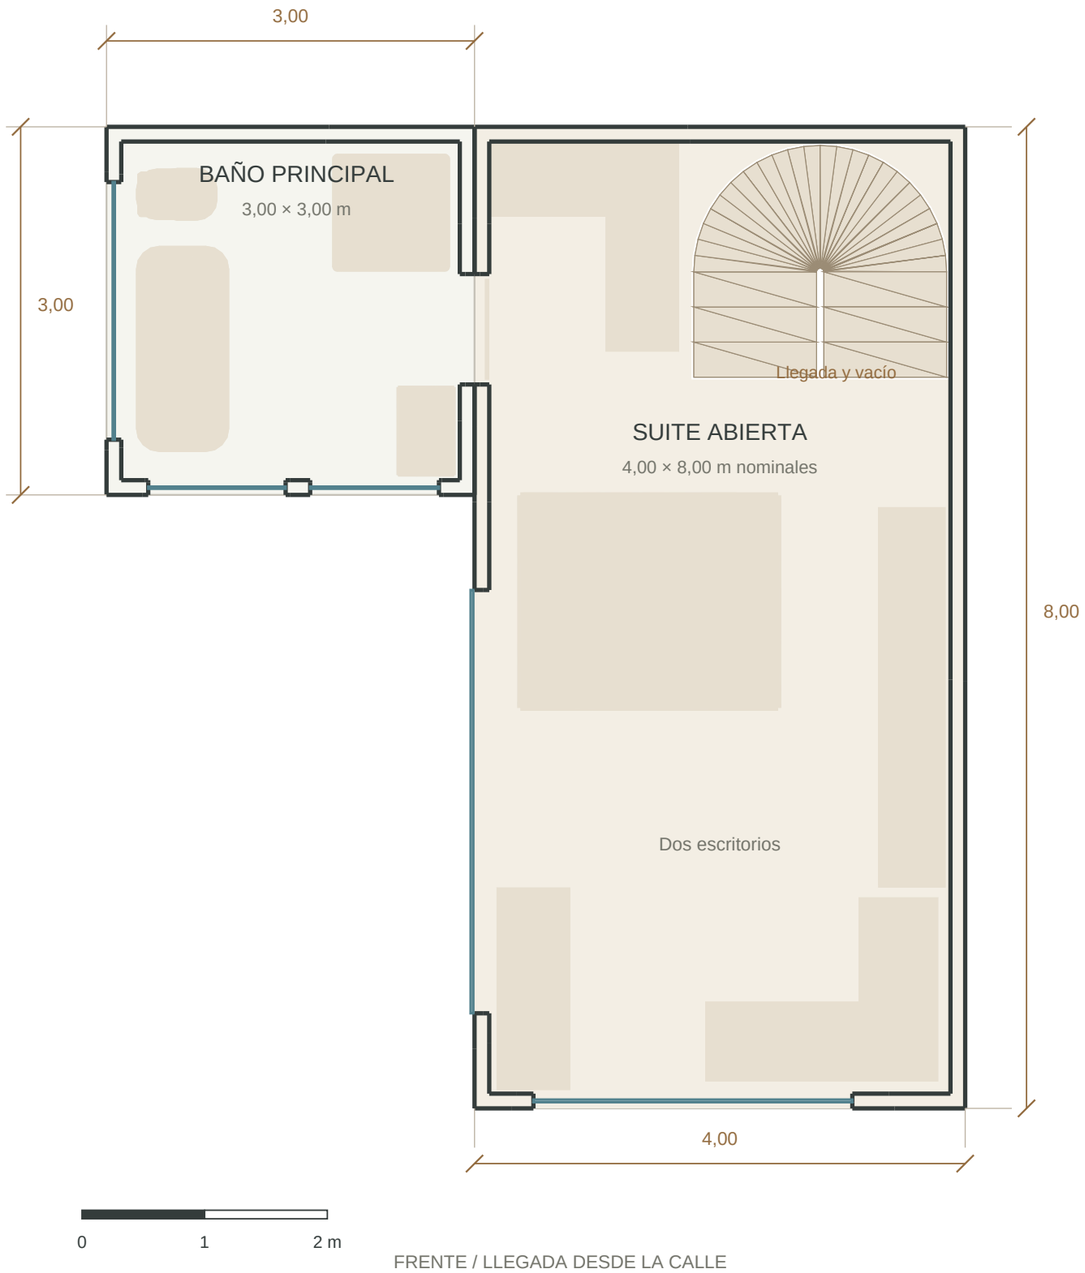

FRENTE / LLEGADA DESDE LA CALLE

ESCALA 1:50 / A3 AL 100 %

No ajustar a página. Comprobar escala gráfica.

Suite abierta
4,00 × 8,00 m
Envolvente de 32 m²; incluye vacío y llegada de gradas.

Baño principal
3,00 × 3,00 m
Antiguo balcón integrado. Volado aproximado de 1 m.

Armario frente a cama
3,10 × 0,61 × 2,18 m
Largo × fondo × alto; carpintería provisional.

Escritorio ventanal
1,65 × 0,60 m
Altura de tablero 0,75 m.

Escritorio en L
1,90 × 1,50 m
Fondo de tablero 0,65 m.

Vacío de escalera
3,57 m²
Forma tomada del entrepiso actual; no es área habitable.

NOTAS PARA REPLANTEO


Suite sin pasillo separado; dos escritorios y armario con TV frente a cama.

Gradas provisionales: 13 subidas de 17,69 cm; huella recta 28,62 cm; ancho nominal 1,00 m.

Subida +2,30 m supuesta. Verificar entrepiso, paso y barandas; vacío irregular conservado.

Volado del baño, anclajes y refuerzos pendientes de cálculo.

Revisión 27/10/2026 · cd2850e7 | Modelo y propuesta de coordinación - comprobar en sitio

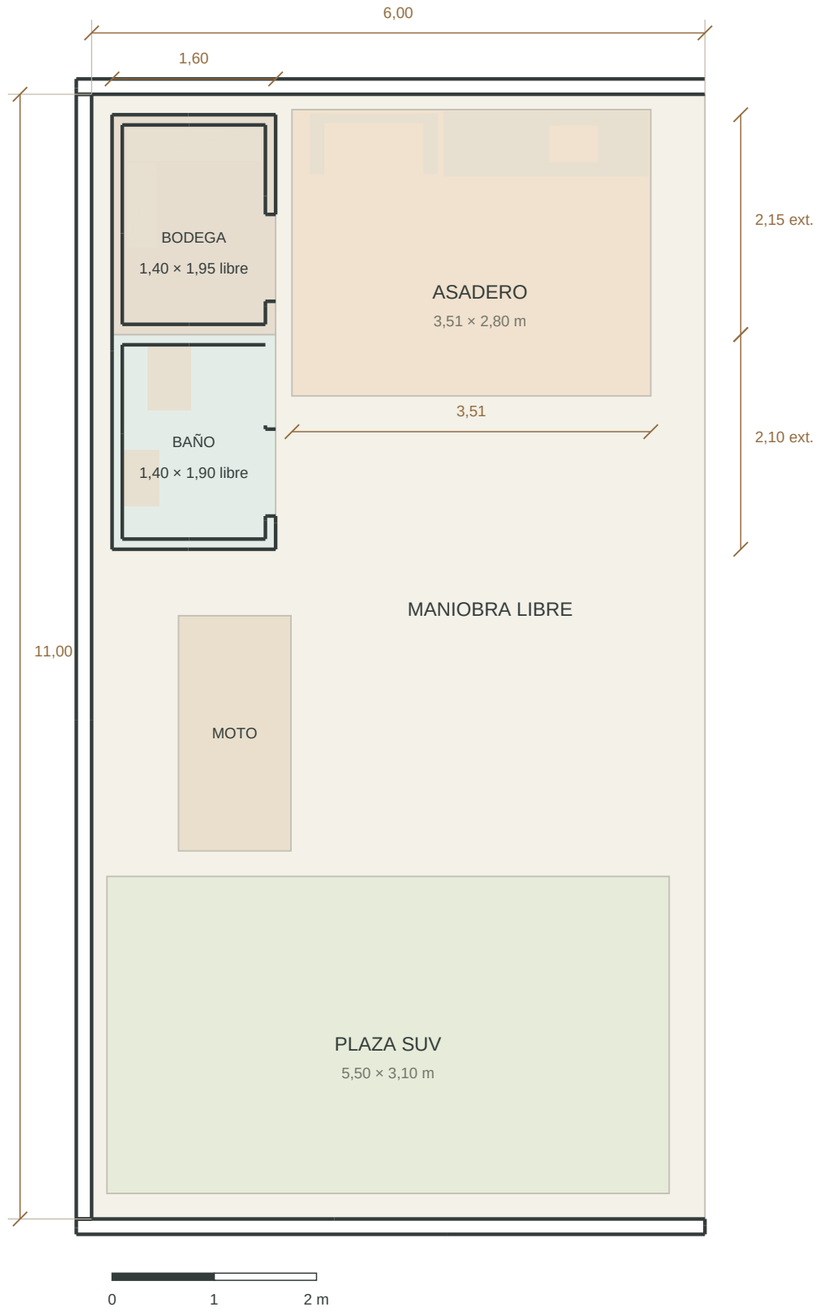

FRENTE / LLEGADA DESDE LA CALLE

ESCALA 1:60 / A3 AL 100 %

No ajustar a página. Comprobar escala gráfica.

Terreno patio
6,00 × 11,00 m
66 m²; las reservas interiores no se suman otra vez.

Servicios exterior
1,60 × 4,25 m
Modelo · verificar en sitio

Baño libre
1,40 × 1,90 m
Libre modelado; medir antes de levantar muros.

Bodega libre
1,40 × 1,95 m
Modelo · verificar en sitio

Asadero
3,51 × 2,80 m
Modelo · verificar en sitio

SUV / moto
5,50 × 3,10 / 1,10 × 2,30 m
Reservas de parqueo; mantener libre el giro.

NOTAS PARA REPLANTEO


Baño y asadero con porcelanato beige. Bodega con adoquín del patio.

Ventana de baño patio ampliada a 0,75 × 0,60 m, vidrio de privacidad.

Una sola cubierta en L para moto, baño, bodega y asadero.

Ventilación, agua, desagües y separación de chimenea por definir en sitio.

Revisión 27/10/2026 · cd2850e7 | Modelo y propuesta de coordinación - comprobar en sitio

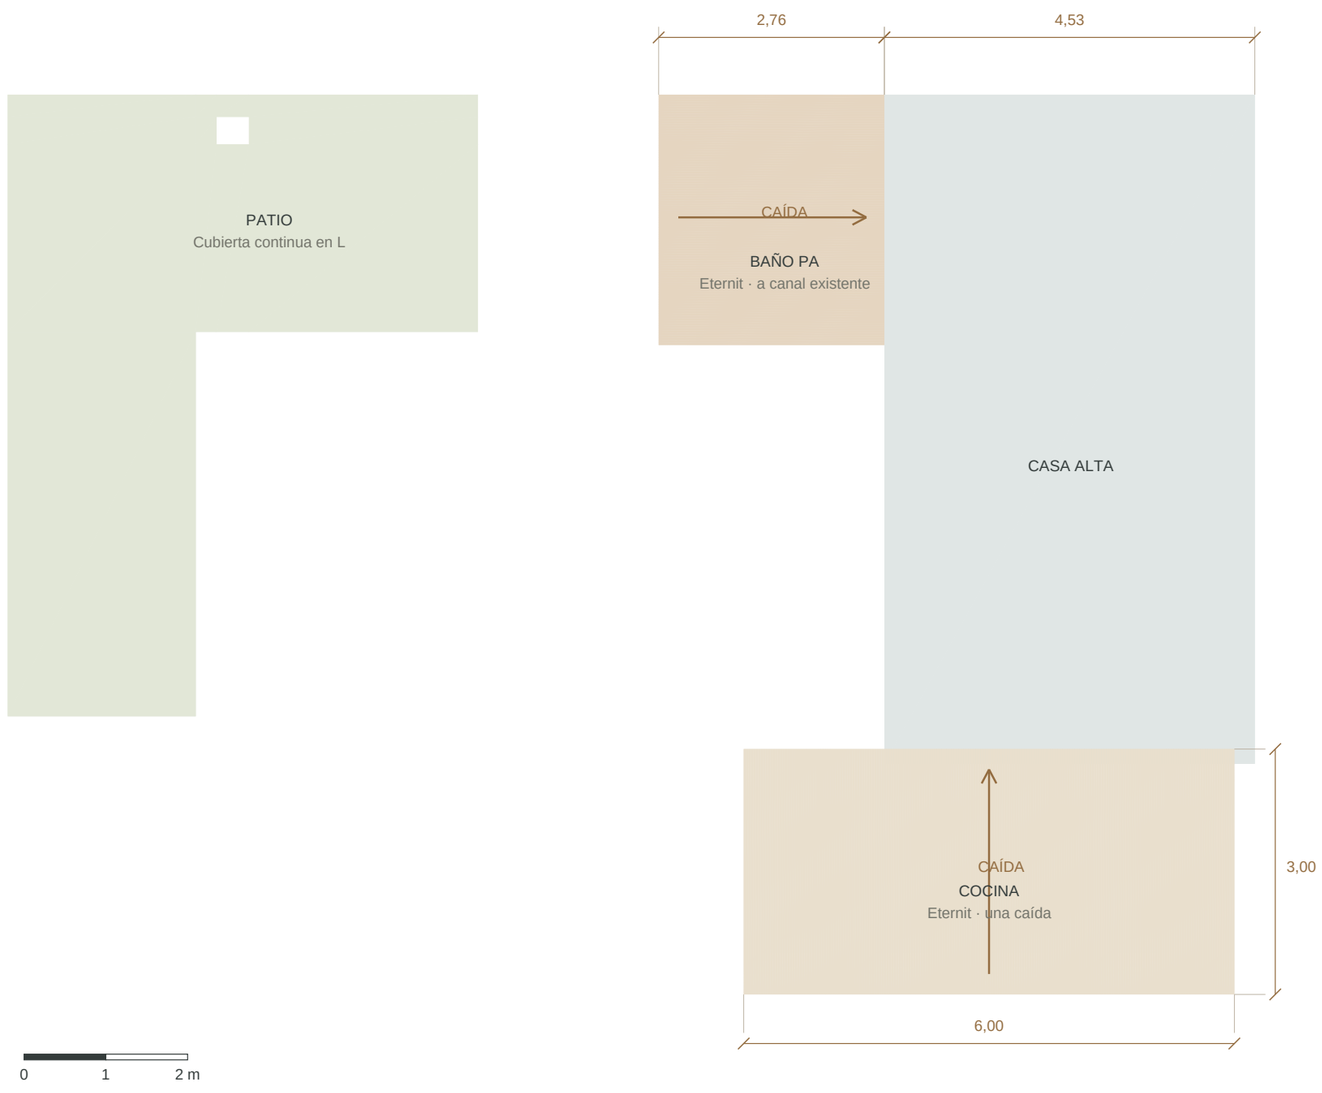

FRENTE / LLEGADA DESDE LA CALLE

ESCALA 1:75 / A3 AL 100 %

No ajustar a página. Comprobar escala gráfica.

Cubierta casa alta
4,53 × 8,18 m
Envolvente de proyección; no es cantidad de material.

Cubierta cocina
6,00 × 3,00 m
Envolvente de proyección; no es cantidad de material.

Cubierta baño principal
2,76 × 3,06 m
Envolvente de proyección; no es cantidad de material.

Cubierta patio en L
5,75 × 7,60 m
Envolvente de proyección; no es cantidad de material.

Cocina · niveles del modelo
+2,72 / +3,17 m
Borde bajo / borde alto sin onda. Inclinación del boceto; sistema de baja pendiente por confirmar con fabricante local.

Baño PA · niveles del modelo
+4,73 / +5,14 m
Borde bajo / borde alto sin onda. Inclinación del boceto; sistema de baja pendiente por confirmar con fabricante local.

NOTAS PARA REPLANTEO


Una caída por cubierta. Baño a CanalCeleste existente; cocina a un canal y bajante propios hacia patio. Cielos, entrepiso y volado conservados.

Las cotas verticales usan un origen común del modelo; no son altura libre.

Perfiles, apoyos, anclajes, pendiente, traslapes y desagües pendientes de definición.

No se especifican secciones estructurales ni cantidades comerciales.

Revisión 27/10/2026 · cd2850e7 | Modelo y propuesta de coordinación - comprobar en sitio

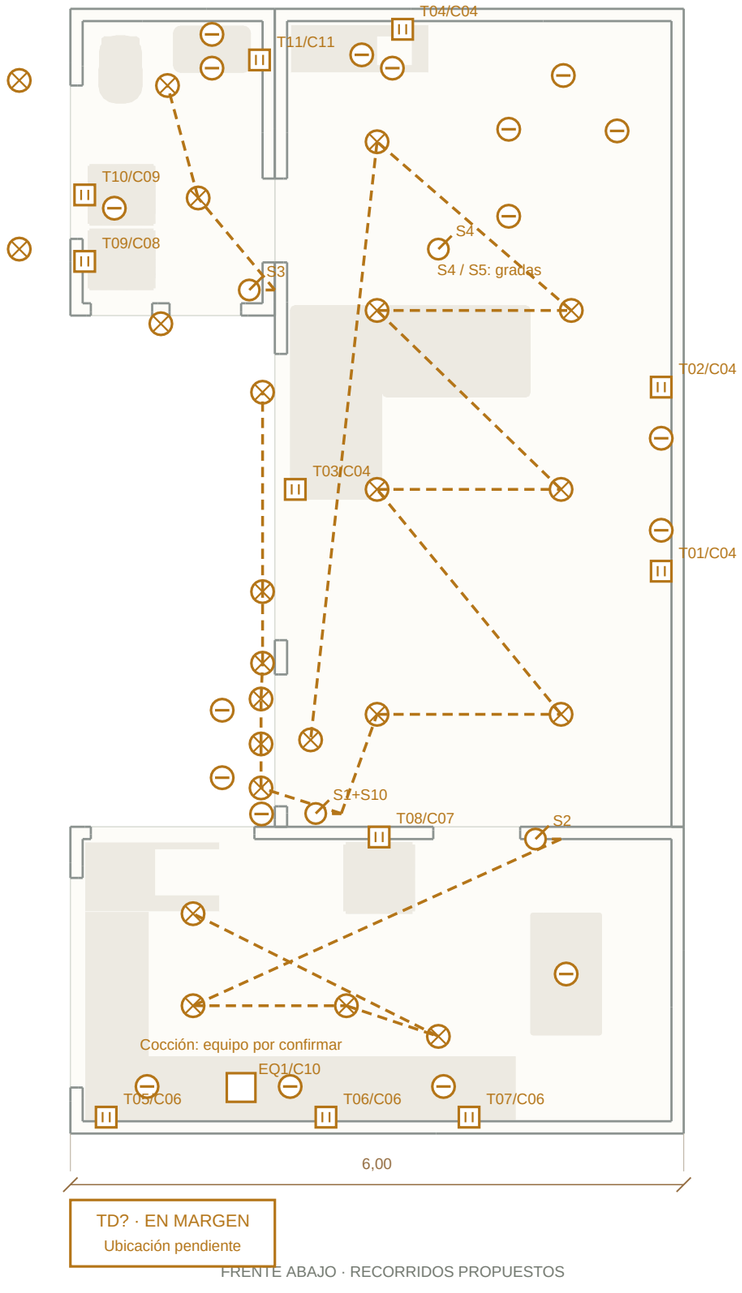

FRENTE ABAJO · RECORRIDOS PROPUESTOS

ESCALA 1:60 / A3 AL 100 %

Propuesta de coordinación; diseño pendiente.

Luz general del modelo

23 puntos

Círculo con cruz. Los puntos del visor no equivalen siempre a luminarias comerciales.

Apoyo / trabajo

18 referencias

Círculo con barra; LED y apliques del modelo.

Tomas propuestas

11 puntos

T01-T21: ubicación y altura por revisar.

Mandos propuestos

S1, S2, S3, S4, S10

S4 / S5: prever control de gradas desde ambos niveles.

Circuitos por usos

Ver E-04

Grupos preliminares, sujetos a carga real.

NOTAS PARA REPLANTEO

Luminarias desde el modelo; tomas y mandos son nuevos puntos propuestos.


Líneas punteadas: relación de mando y recorrido conceptual; no son número de conductores.

Tablero, suministro, cargas, calibres, protecciones y tierra: levantar y calcular antes de tender.

Bajo Eternit: canalización y cajas fijadas a soporte definido, nunca a las planchas.

Verificar zonas húmedas y protección de tomas del baño.

Revisión 27/10/2026 · cd2850e7 | Modelo y propuesta de coordinación - comprobar en sitio

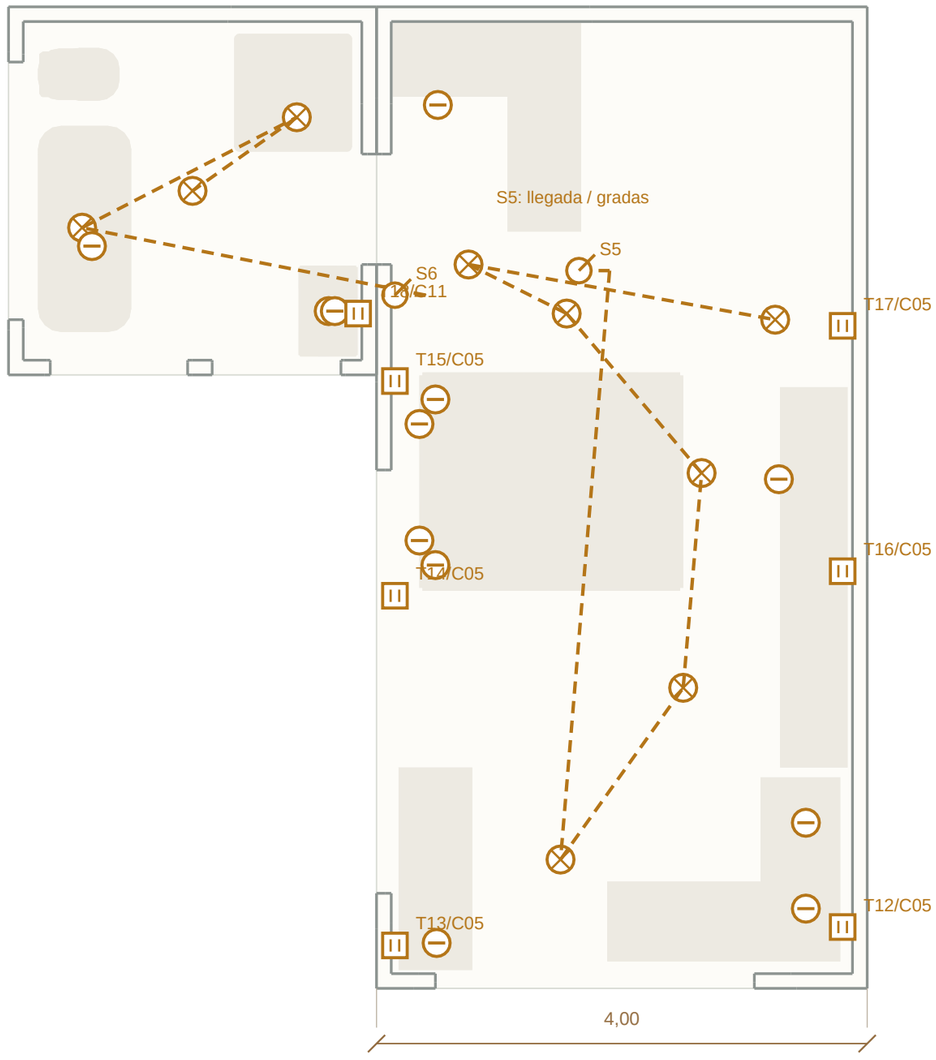

FRENTE ABAJO · RECORRIDOS PROPUESTOS

ESCALA 1:50 / A3 AL 100 %

Propuesta de coordinación; diseño pendiente.

Luz general del modelo
9 puntos
Círculo con cruz. Los puntos del visor no equivalen siempre a luminarias comerciales.

Apoyo / trabajo
12 referencias
Círculo con barra; LED y apliques del modelo.

Tomas propuestas
7 puntos
T01-T21: ubicación y altura por revisar.

Mandos propuestos
S5, S6
S4 / S5: prever control de gradas desde ambos niveles.

Circuitos por usos
Ver E-04
Grupos preliminares, sujetos a carga real.

NOTAS PARA REPLANTEO

Luminarias desde el modelo; tomas y mandos son nuevos puntos propuestos.


Líneas punteadas: relación de mando y recorrido conceptual; no son número de conductores.

Tablero, suministro, cargas, calibres, protecciones y tierra: levantar y calcular antes de tender.

Bajo Eternit: canalización y cajas fijadas a soporte definido, nunca a las planchas.

Verificar zonas húmedas y protección de tomas del baño.

Revisión 27/10/2026 · cd2850e7 | Modelo y propuesta de coordinación - comprobar en sitio

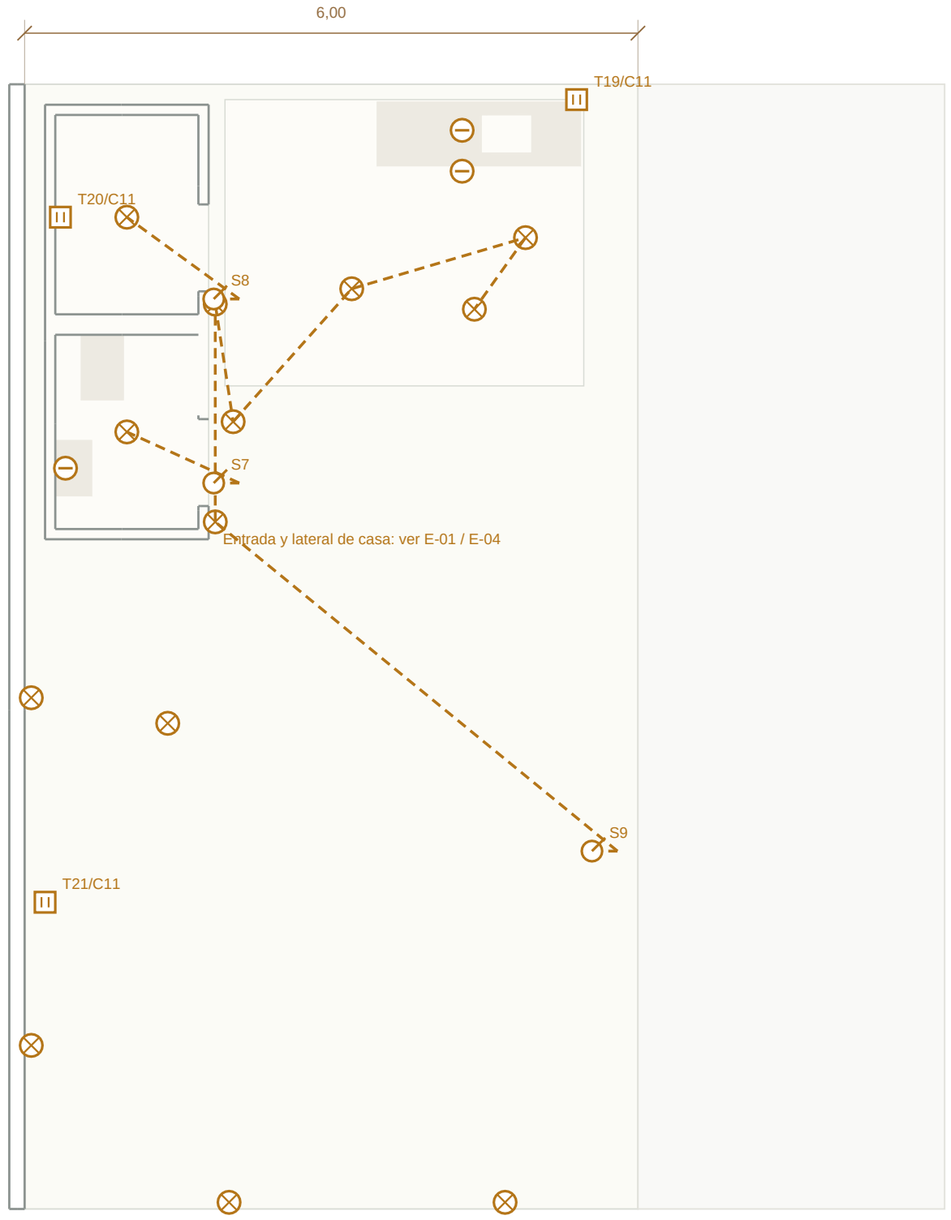

FRENTE ABAJO · RECORRIDOS PROPUESTOS

ESCALA 1:60 / A3 AL 100 %

Propuesta de coordinación; diseño pendiente.

Luz general del modelo

13 puntos

Círculo con cruz. Los puntos del visor no equivalen siempre a luminarias comerciales.

Apoyo / trabajo

3 referencias

Círculo con barra; LED y apliques del modelo.

Tomas propuestas

3 puntos

T01-T21: ubicación y altura por revisar.

Mandos propuestos

S7, S8, S9

S4 / S5: prever control de gradas desde ambos niveles.

Circuitos por usos

Ver E-04

Grupos preliminares, sujetos a carga real.

NOTAS PARA REPLANTEO

Luminarias desde el modelo; tomas y mandos son nuevos puntos propuestos.


Líneas punteadas: relación de mando y recorrido conceptual; no son número de conductores.

Tablero, suministro, cargas, calibres, protecciones y tierra: levantar y calcular antes de tender.

Bajo Eternit: canalización y cajas fijadas a soporte definido, nunca a las planchas.

Prever equipos aptos para intemperie y maniobra despejada.

Revisión 27/10/2026 · cd2850e7 | Modelo y propuesta de coordinación - comprobar en sitio

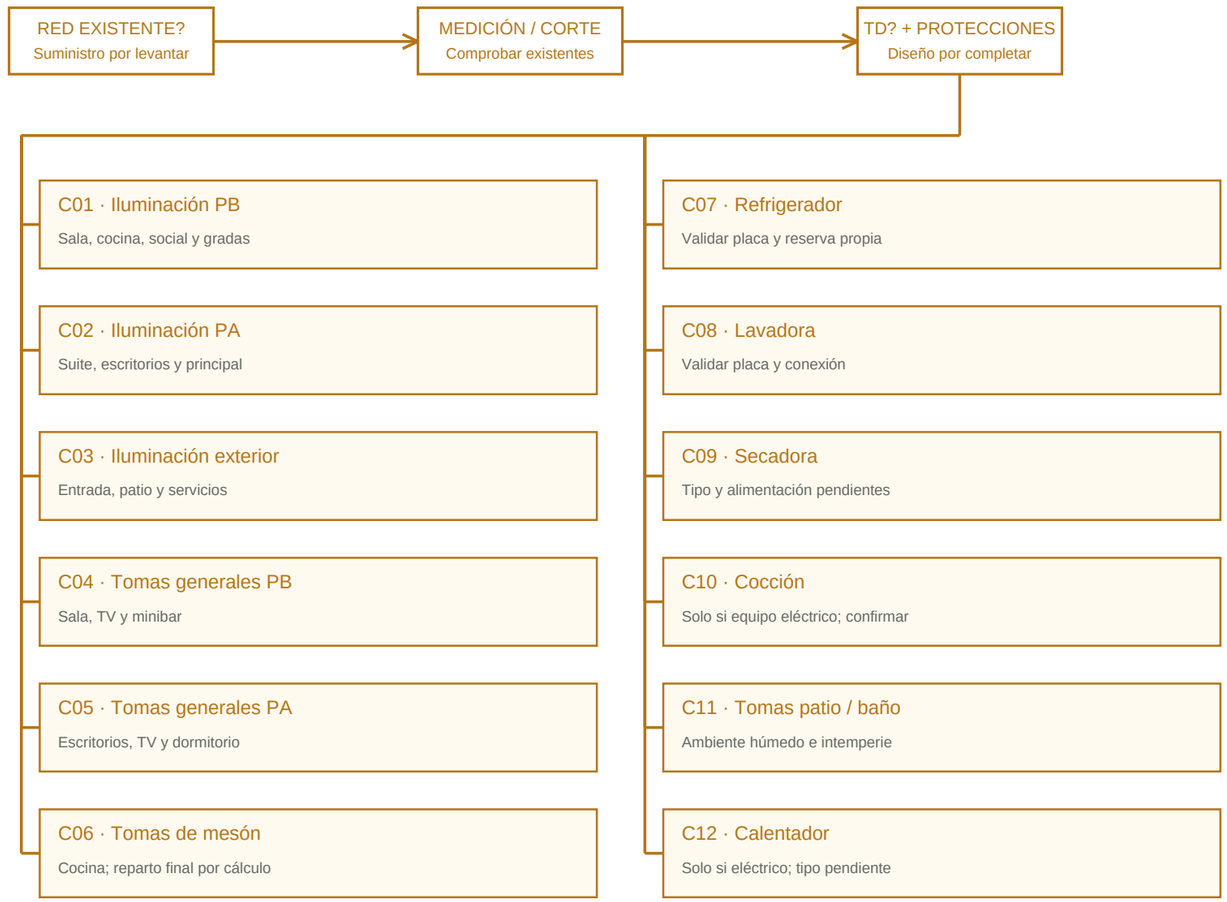

Calibre, polos, A, tensión y canalización: PENDIENTES DE CÁLCULO

ESQUEMA SIN ESCALA

Propuesta de coordinación; diseño pendiente.

Acometida y tablero
Ubicación pendiente
Suministro y capacidad contratada por comprobar.

12 grupos propuestos
Reparto funcional
No es número definitivo de breakers.

Protecciones y tierra
Por dimensionar
Sobrecorriente, diferencial, sobretensión y PE según diseño.

Equipo eléctrico grande
Revisar placa
Secadora, cocción y calentador pueden cambiar el suministro.

NOTAS PARA REPLANTEO


Esquema funcional sin escala; no es un plano de bornes ni un cableado para ejecutar.

Separar mando por ambiente de circuitos de potencia: no equivalen entre sí.

Levantar cargas y longitudes; calcular demanda, caída de tensión y protecciones.

Confirmar protección en baños y exterior y verificar puesta a tierra con el instalador.

Revisión 27/10/2026 · cd2850e7 | Modelo y propuesta de coordinación - comprobar en sitio

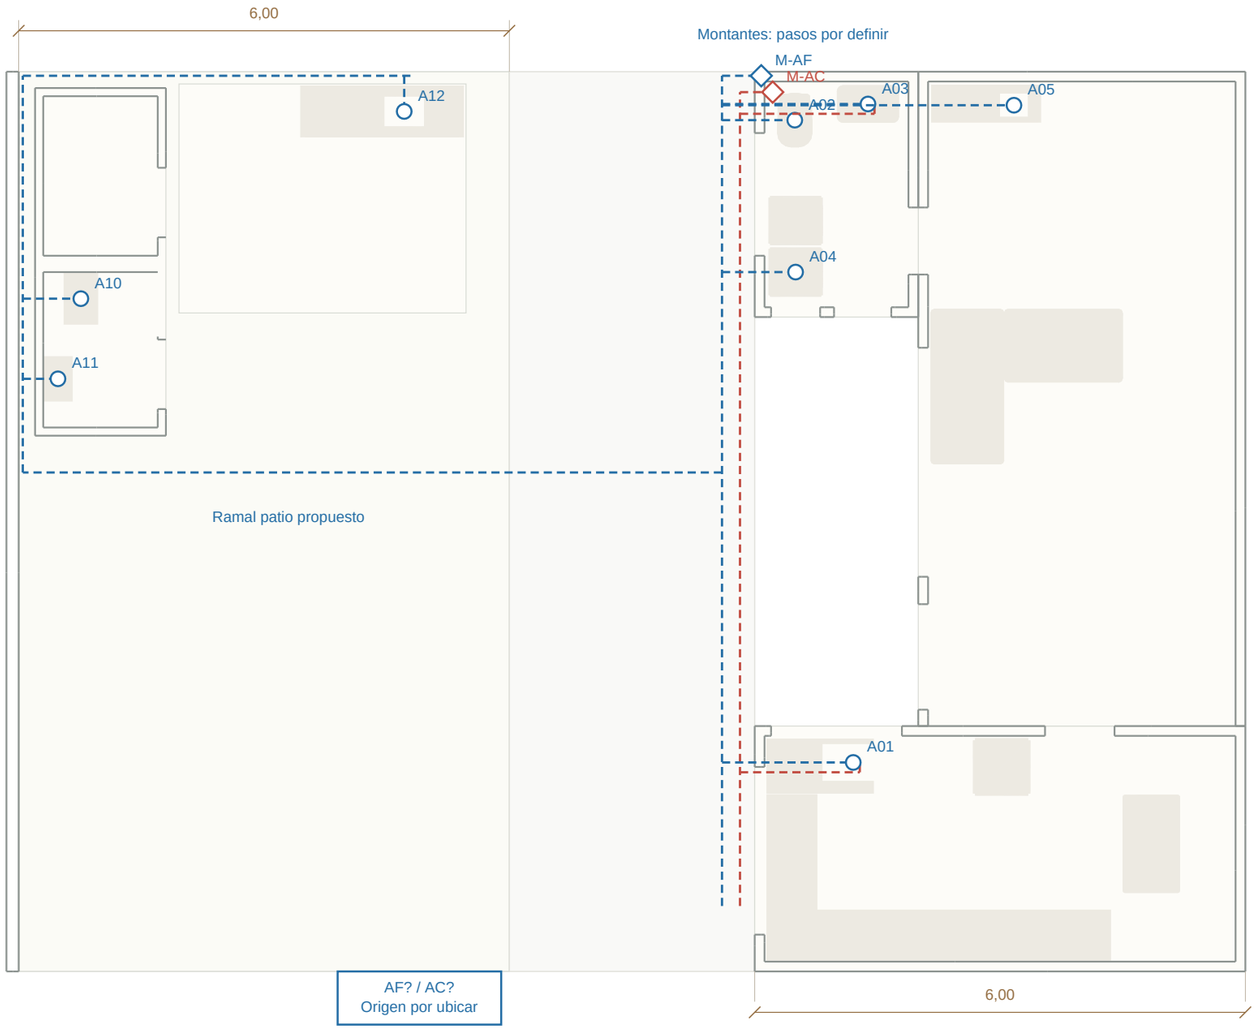

FRENTE ABAJO · RECORRIDOS PROPUESTOS

ESCALA 1:75 / A3 AL 100 %

Propuesta de coordinación; diseño pendiente.

Puntos de agua

8 aparatos

A01-A12: detalle en cuadro de instalaciones.

Agua caliente propuesta

A01, A03

Confirmar alcance y tipo de calentador.

M-AF / M-AC

Montantes propuestos

Coinciden entre H-01 y H-02; huecos no definidos.

Diámetros / presión

Por calcular

No comprar tubería por el grosor del dibujo.

NOTAS PARA REPLANTEO

Azul: agua fría. Rojo: reserva propuesta de agua caliente. Trazos punteados: recorridos por confirmar.


A01-A12 identifican aparatos del modelo; la salida exacta se ajusta al equipo real.

Medidor y calentador no se ubican físicamente. Conexiones AF? / AC? son referencias de margen.

Medir presión y caudal; calcular diámetros, llaves y pruebas antes de instalar.

No ranurar vigas ni perforar el entrepiso o volado sin definir el paso con el responsable técnico.

Revisión 27/10/2026 · cd2850e7 | Modelo y propuesta de coordinación - comprobar en sitio

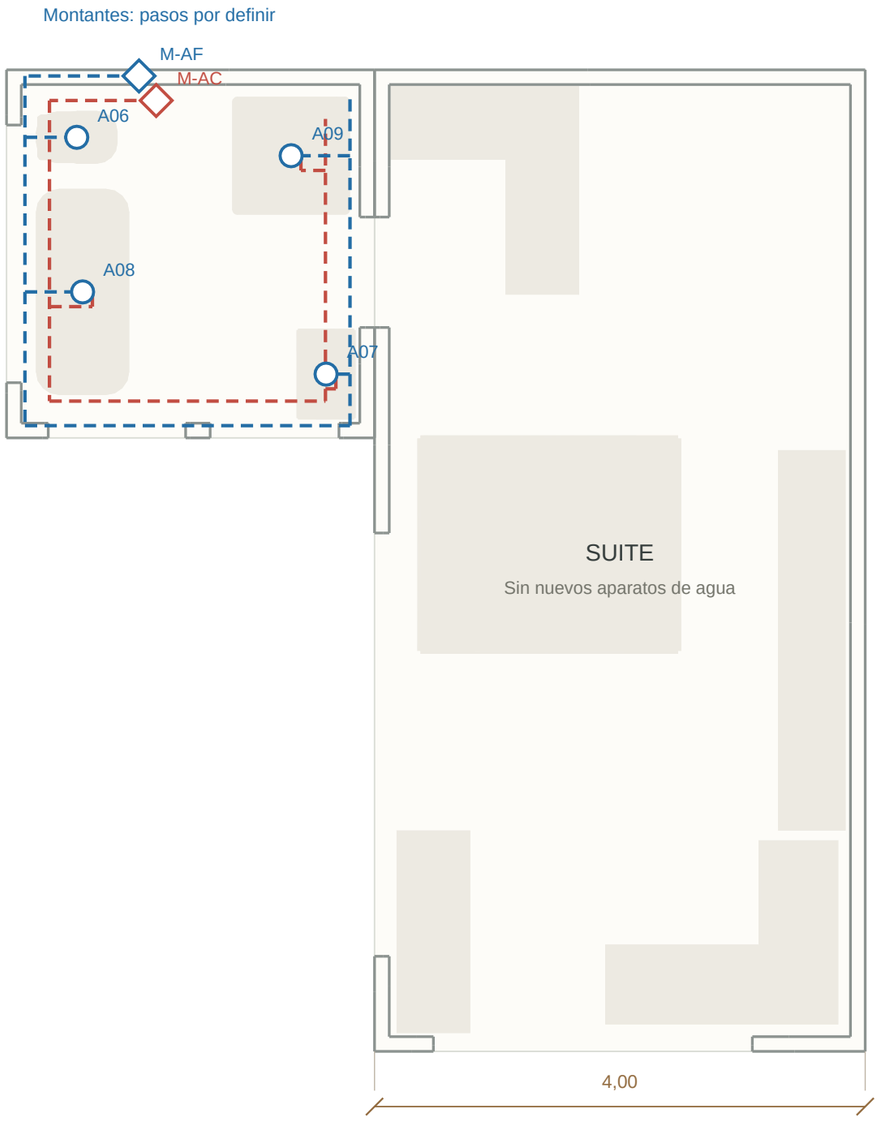

FRENTE ABAJO · RECORRIDOS PROPUESTOS

ESCALA 1:50 / A3 AL 100 %

Propuesta de coordinación; diseño pendiente.

Puntos de agua

4 aparatos

A01-A12: detalle en cuadro de instalaciones.

Agua caliente propuesta

A07, A08, A09

Confirmar alcance y tipo de calentador.

M-AF / M-AC

Montantes propuestos

Coinciden entre H-01 y H-02; huecos no definidos.

Diámetros / presión

Por calcular

No comprar tubería por el grosor del dibujo.

NOTAS PARA REPLANTEO

Azul: agua fría. Rojo: reserva propuesta de agua caliente. Trazos punteados: recorridos por confirmar.


A01-A12 identifican aparatos del modelo; la salida exacta se ajusta al equipo real.

Medidor y calentador no se ubican físicamente. Conexiones AF? / AC? son referencias de margen.

Medir presión y caudal; calcular diámetros, llaves y pruebas antes de instalar.

No ranurar vigas ni perforar el entrepiso o volado sin definir el paso con el responsable técnico.

Revisión 27/10/2026 · cd2850e7 | Modelo y propuesta de coordinación - comprobar en sitio

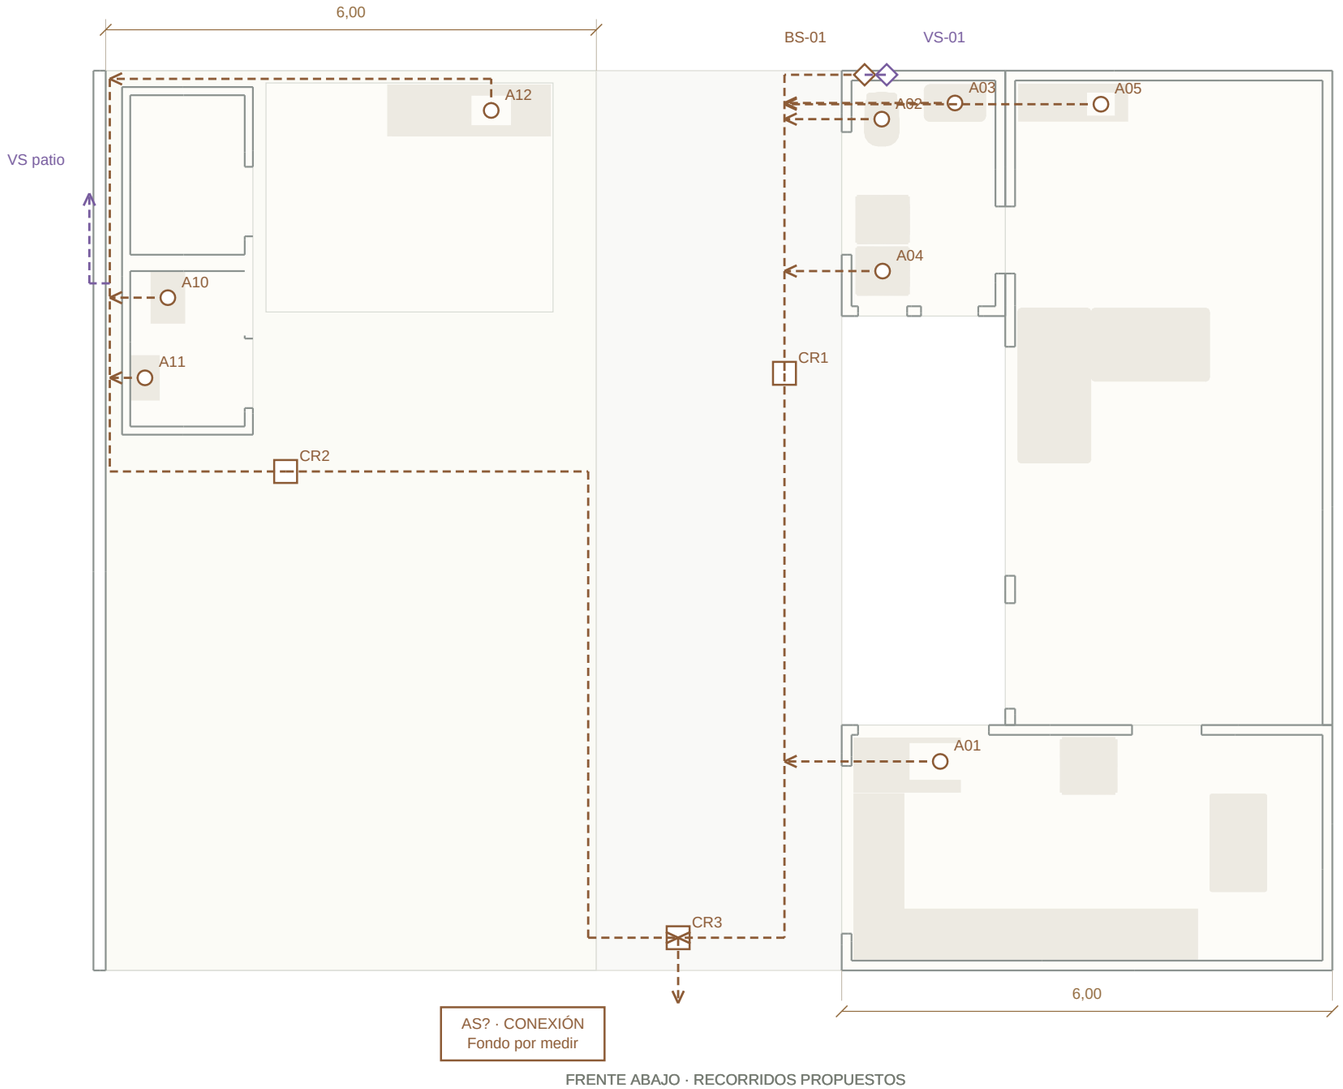

FRENTE ABAJO · RECORRIDOS PROPUESTOS

ESCALA 1:75 / A3 AL 100 %

Propuesta de coordinación; diseño pendiente.

Aparatos conectados

8 puntos sanitarios

Identificación A01-A12 igual a la red de agua.

BS-01 / VS-01

Bajante / ventilación

Trazo propuesto, sin perforación definida.

CR-01 / CR-02 / CR-03

Registros propuestos

En PB: accesos y niveles por comprobar.

Diámetros / pendientes

Por calcular

Dependen de carga y cota real de descarga.

NOTAS PARA REPLANTEO

Marrón: aguas servidas. Violeta: ventilación sanitaria a resolver hasta cubierta.


Flechas indican destino conceptual; no fijan pendiente ni profundidad.

Salida sanitaria, cotas de fondo y red existente: levantar antes de zanjas o cortes.

Prever sifones y registros accesibles; dimensionar ramales, bajantes y ventilación.

Las aguas lluvias tienen red separada en P-01; su destino final se comprueba con la red del predio.

Revisión 27/10/2026 · cd2850e7 | Modelo y propuesta de coordinación - comprobar en sitio

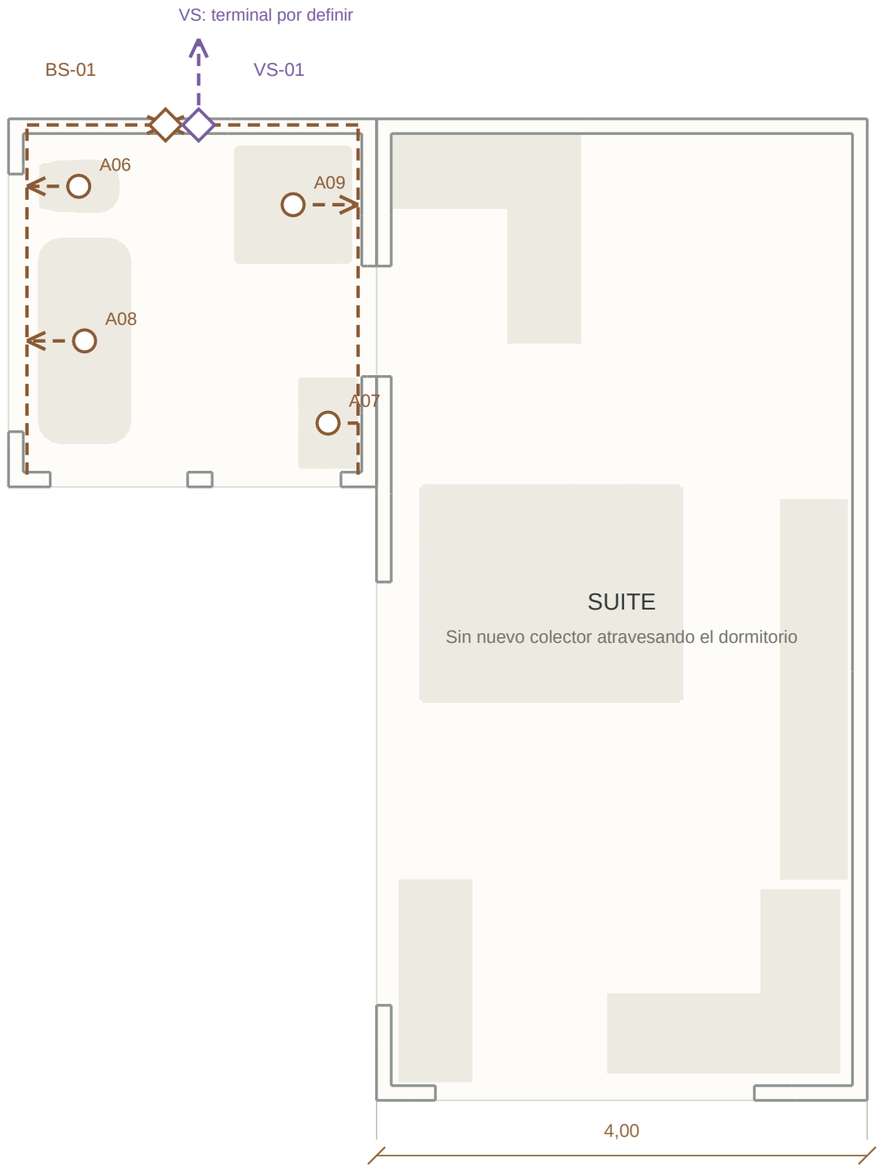

FRENTE ABAJO · RECORRIDOS PROPUESTOS

ESCALA 1:50 / A3 AL 100 %

Propuesta de coordinación; diseño pendiente.

Aparatos conectados

4 puntos sanitarios

Identificación A01-A12 igual a la red de agua.

BS-01 / VS-01

Bajante / ventilación

Trazo propuesto, sin perforación definida.

CR-01 / CR-02 / CR-03

Registros propuestos

En PB: accesos y niveles por comprobar.

Diámetros / pendientes

Por calcular

Dependen de carga y cota real de descarga.

NOTAS PARA REPLANTEO

Marrón: aguas servidas. Violeta: ventilación sanitaria a resolver hasta cubierta.


Flechas indican destino conceptual; no fijan pendiente ni profundidad.

Salida sanitaria, cotas de fondo y red existente: levantar antes de zanjas o cortes.

Prever sifones y registros accesibles; dimensionar ramales, bajantes y ventilación.

Las aguas lluvias tienen red separada en P-01; su destino final se comprueba con la red del predio.

Revisión 27/10/2026 · cd2850e7 | Modelo y propuesta de coordinación - comprobar en sitio

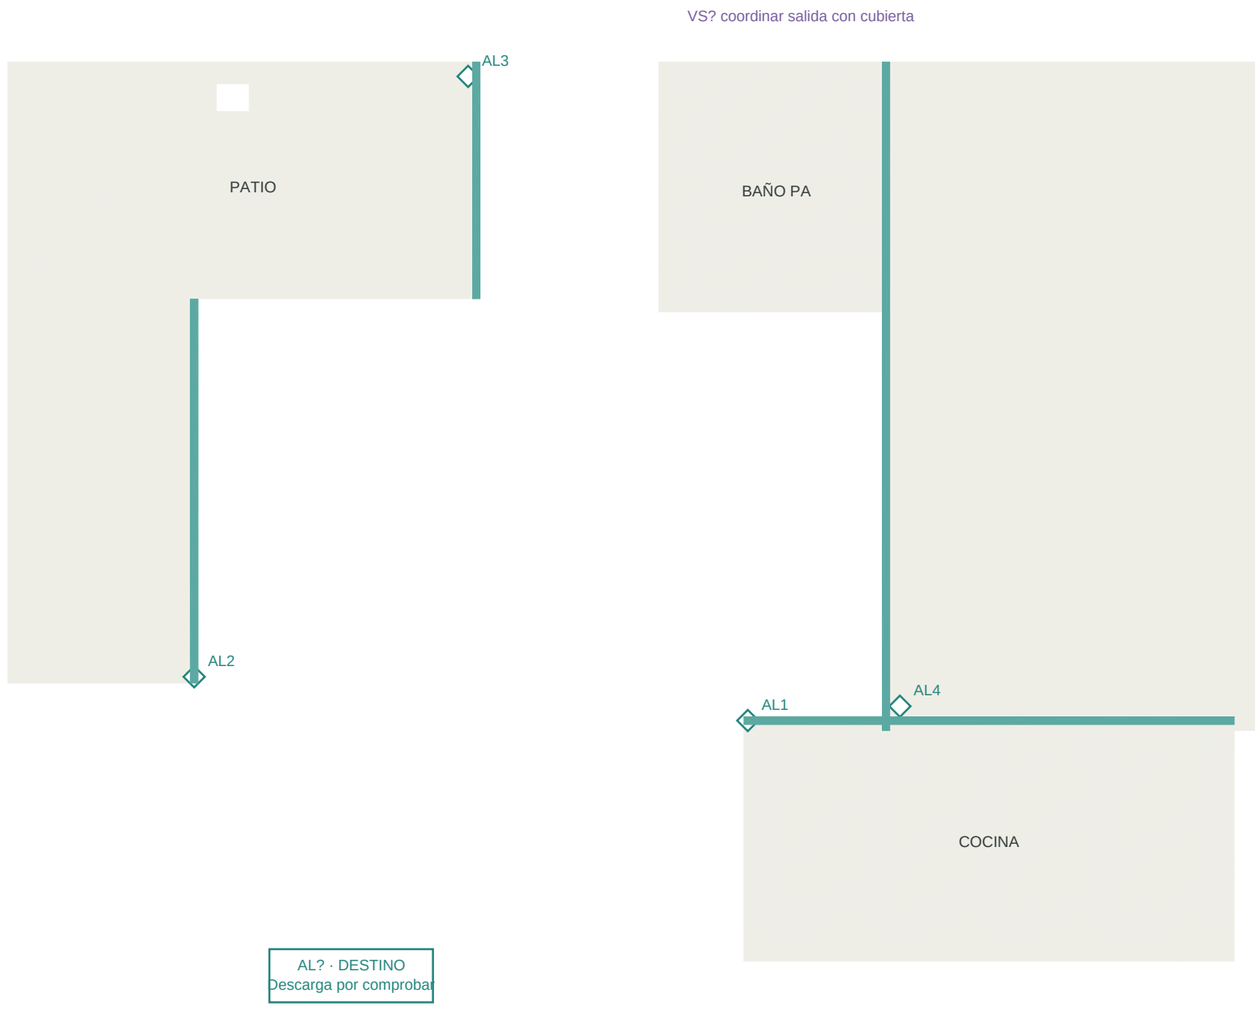

ESCALA 1:75 / A3 AL 100 %

Propuesta de coordinación; diseño pendiente.

Cubiertas Eternit

Cocina y baño principal

Una caída por techo; baño a canaleta existente. Cielos independientes.

Canaletas y bajantes

Posiciones del modelo

Capacidad, diámetro y unión final por calcular.

VS-01 y VS patio

Remates por coordinar

No se fija un hueco ni una salida sobre Eternit.

Descarga pluvial

Ubicación pendiente

No conectada aquí al colector de aguas servidas.

NOTAS PARA REPLANTEO


Verde azulado: canaletas y bajantes de lluvia del modelo vigente.

Azul y rojo se reservan para agua potable; marrón para desagüe sanitario.

Calcular área aportante, lluvia de diseño, capacidad de canaletas y descarga.

Coordinar pasos de ventilación con cerchas, correas, ventanas y sellos; sin cortar Eternit en esta propuesta.

Revisión 27/10/2026 · cd2850e7 | Modelo y propuesta de coordinación - comprobar en sitio

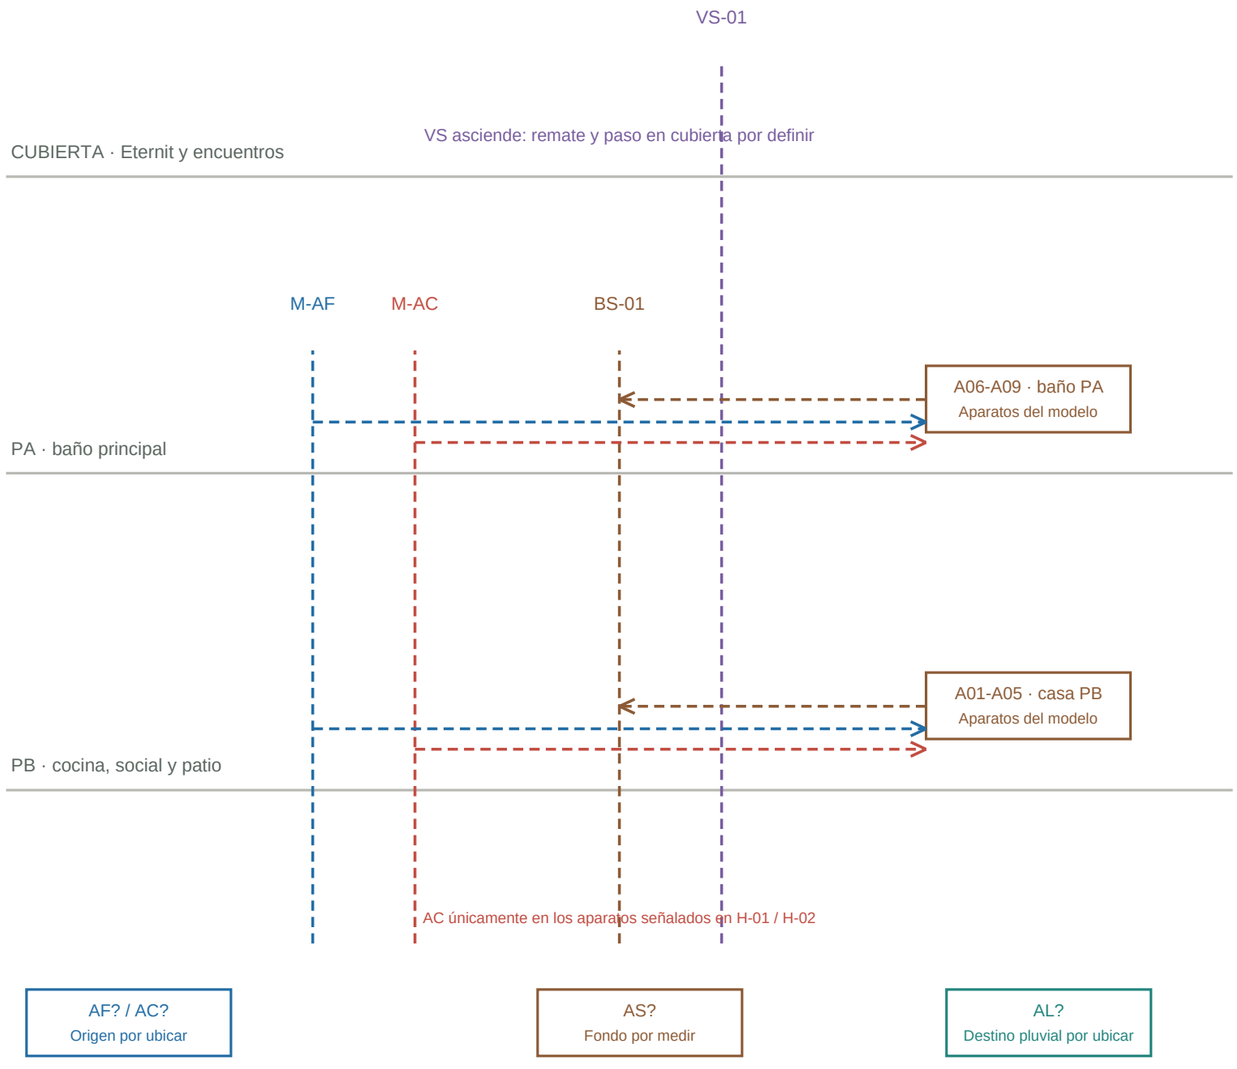

ESQUEMA SIN ESCALA

Propuesta de coordinación; diseño pendiente.

AF? / AC?

Origen por localizar

Entrada de agua y calentador no definidos.

AS? / AL?

Destinos por localizar

Sanitario y lluvia se coordinan por separado.

Entrepisos y apoyos

Conservados

No se autorizan huecos ni ranuras con este esquema.

Alturas de conexión

Por medir

Símbolos en planta sobre el aparato, sin plantilla de obra.

NOTAS PARA REPLANTEO

Esquema funcional sin escala. No representa la posición física de acometidas, calentador o colectores.

Antes de ejecutar: levantar instalaciones existentes y calcular electricidad e hidráulica.

Comprobar presión, caudal y cotas de fondo para resolver agua y gravedad.

La ventilación sanitaria necesita salida y distancias a huecos verificadas en cubierta.

Revisión 27/10/2026 · cd2850e7 | Modelo y propuesta de coordinación - comprobar en sitio

APARATOS DEL MODELO Y SERVICIOS PROPUESTOS

ID	APARATO	NIVEL	AF	AC	AS
A01	Lavaplatos cocina	PB	Sí	Sí*	Sí
A02	Inodoro social	PB	Sí	-	Sí
A03	Lavabo social	PB	Sí	Sí*	Sí
A04	Lavadora	PB	Sí	-	Sí
A05	Lavavasos minibar	PB	Sí	-	Sí
A06	Inodoro principal	PA	Sí	-	Sí
A07	Lavabo principal	PA	Sí	Sí*	Sí
A08	Tina principal	PA	Sí	Sí*	Sí
A09	Ducha principal	PA	Sí	Sí*	Sí
A10	Inodoro patio	Patio	Sí	-	Sí
A11	Lavabo patio	Patio	Sí	-	Sí
A12	Fregadero asadero	Patio	Sí	-	Sí

* AC: propuesta de servicio; calentador y alcance por definir.

Referencias de consulta (no acreditan un diseño calculado):

NEC: www.mit.gob.ec/norma-ecuatoriana-de-la-construccion/

MIDUVI: Directrices de proyectos de vivienda, apartados 2.3 y 2.4 (gob.ec).

ESQUEMA SIN ESCALA

Propuesta de coordinación; diseño pendiente.

12 aparatos

Origen: modelo vigente

Cada A conserva el mismo código en agua y desagües.

AF / AC / AS

Fría / caliente / servidas

AC es reserva propuesta y debe confirmarse.

Cota de salida

Pendiente de medir

El centro dibujado no es la perforación de obra.

Base de consulta

NEC y directrices MIDUVI

Diseños y cálculos de ingeniería por desarrollar.

NOTAS PARA REPLANTEO

Inodoros y ramales de patio solo con AF en esta propuesta.

Lavadora con AF; confirmar ficha del equipo. La secadora no incorpora agua ni desagüe automático.

Si una secadora de condensación requiere descarga, añadir su ramal después de seleccionar equipo.

Medir aparatos reales, llaves, sifones, pasos y pruebas antes del montaje.

Revisión 27/10/2026 · cd2850e7 | Modelo y propuesta de coordinación - comprobar en sitio

HUECOS DE PUERTAS Y VENTANAS - MEDIDAS NOMINALES

IDENTIFICACIÓN	NIVEL	ANCHO m	ALTO m	COTA INFERIOR m
Acceso al baño principal	PA	0,90	2,10	2,30
Entrada 1,20 x 2,10 (altura por verificar)	PB	1,29	2,15	0,00
Sala · ventanal hacia el patio	PB	2,80	1,20	0,65
Social · frente, lado izquierdo	PB	0,60	0,57	1,22
Social · frente, lado derecho	PB	0,70	0,57	1,22
Principal · frente, lado izquierdo	PA	1,12	0,75	3,47
Principal · frente, lado derecho	PA	1,05	0,75	3,47
Social · ventana hacia calle	PB	1,50	0,75	1,10
Principal · ventana hacia calle	PA	2,10	0,85	3,40
Dormitorio · ventanal hacia patio	PA	3,45	1,40	3,00
Dormitorio · ventana de retorno	PA	2,60	1,40	3,00
Cocina · ventana hacia calle	PB	2,05	1,20	0,95
Cocina · ventana de retorno	PB	1,60	1,20	0,95
Baño social (hoja 0,80 x 1,95)	PB	0,82	1,98	0,00
Puerta baño patio (hoja 0,80 x 1,98)	Patio	0,85	2,05	-0,23
Puerta bodega (hoja 0,80 x 1,98)	Patio	0,85	2,05	-0,23
Ventana bodega	Patio	0,80	0,20	1,85
Ventana baño patio	Patio	0,75	0,60	Por medir

Cotas inferiores referidas al origen común del modelo. En PA no equivalen a antepecho desde su piso.

PENDIENTES DE MEDICIÓN

Replantear anchos libres, espesores de muro y posición real de cada hueco.

Medir niveles de piso, entrepiso, vigas y altura libre antes de definir las gradas.

Verificar hojas, marcos y giro real de puertas. Diferenciar hueco de obra y paso útil.

Cubiertas: definir ficha del producto, pendiente, traslapes, anclajes y drenajes.

Confirmar ubicación de agua, desagües, ventilación, luminarias, mandos y tomas.

Dimensionar volado, gradas, barandas, refuerzos y cimentaciones con el responsable técnico.

Entrada objetivo: 1,20 x 2,10 m, apertura exterior. Cielo a 2 m: resolver altura y dintel antes de fabricar. Descanso exterior y giro por medir.