
A-01 · Conjunto y medidas generales

CASA LALES · MAPA COMPLETO · ESCALA 1:60 · IMPRIMIR AL 100 %

Revisión 12/11/2026 · 22dd2a9a

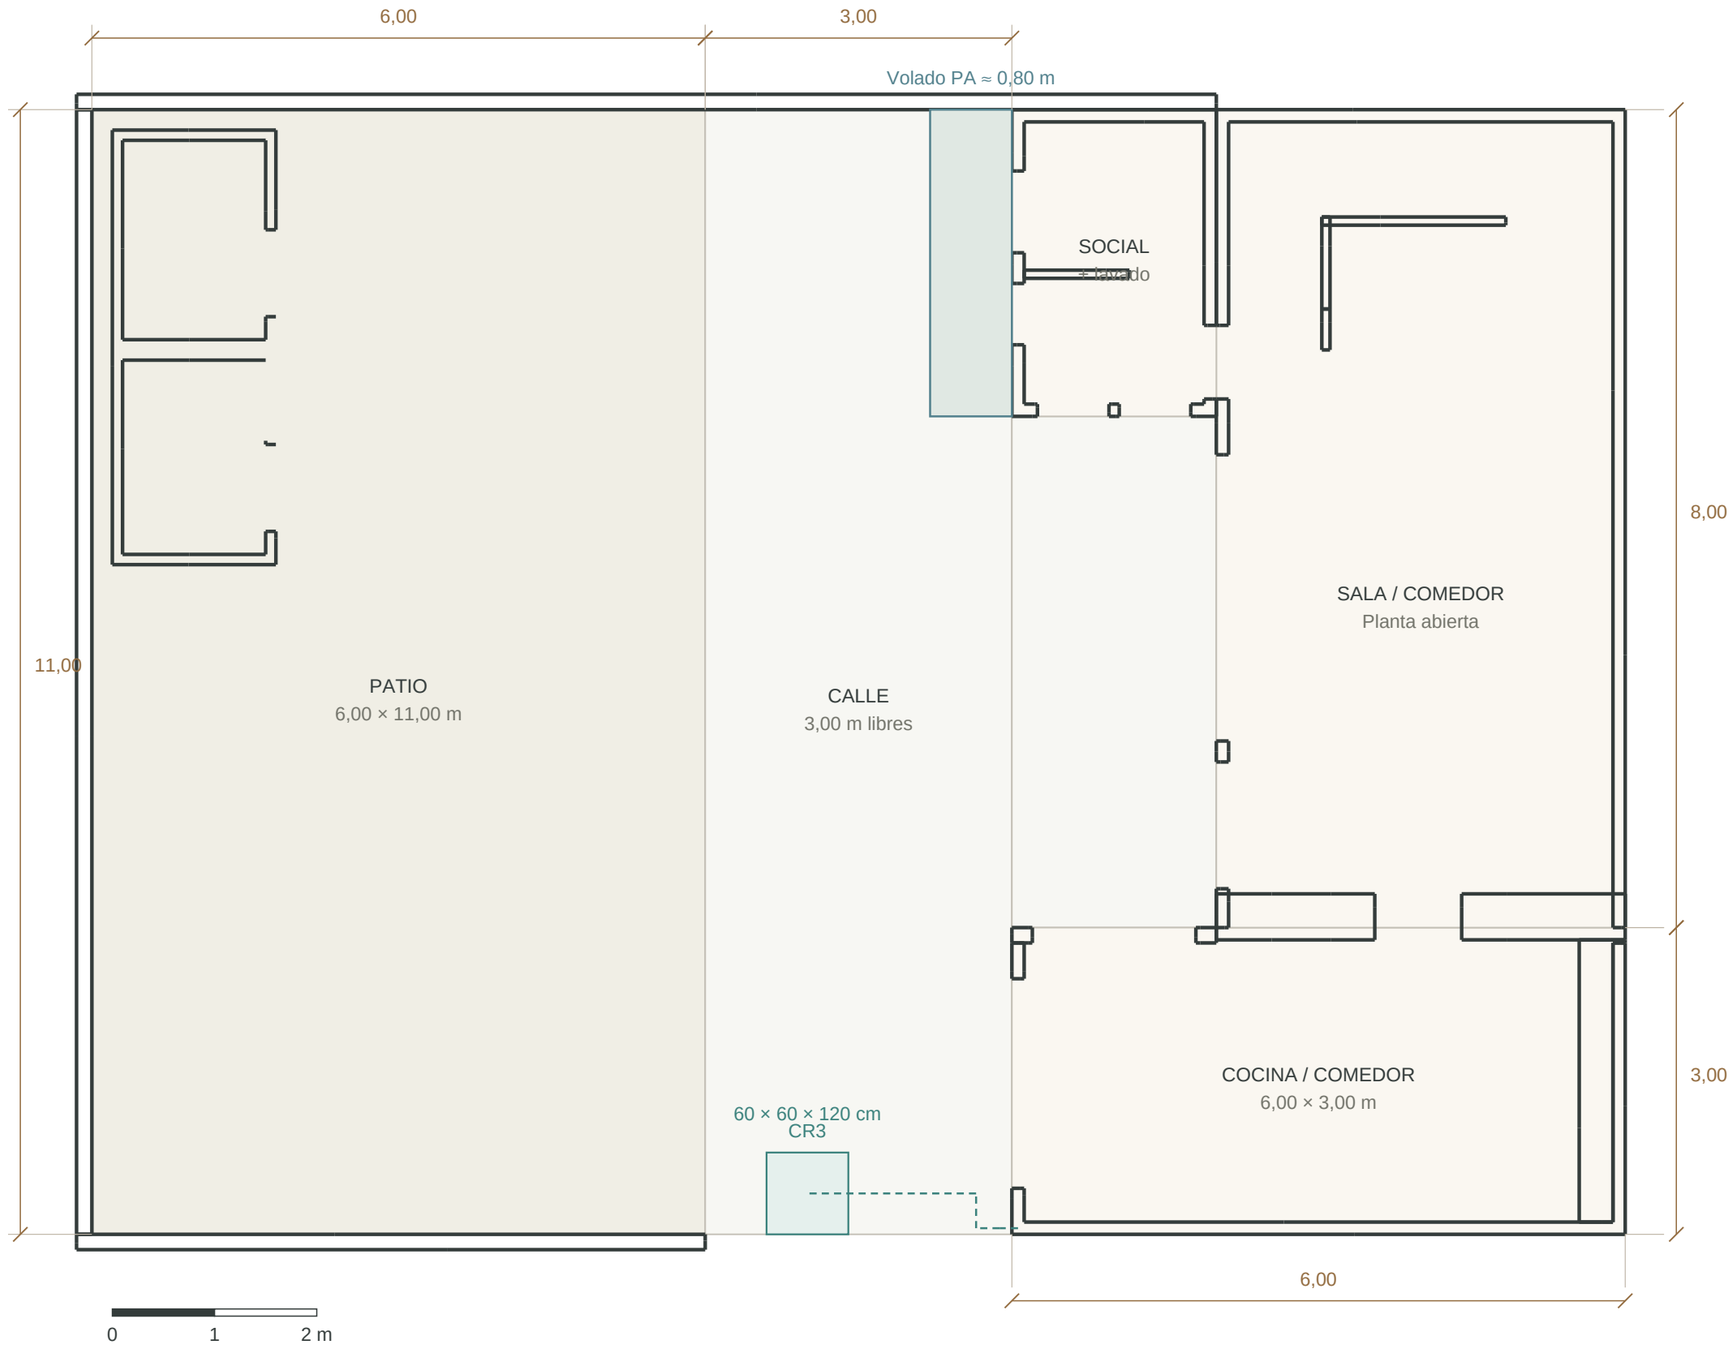


FRENTE / LLEGADA DESDE LA CALLE

A-02 · Planta baja · cocina, sala y servicios

CASA LALES · MAPA COMPLETO · ESCALA 1:40 · IMPRIMIR AL 100 %


Revisión 12/11/2026 · 22dd2a9a

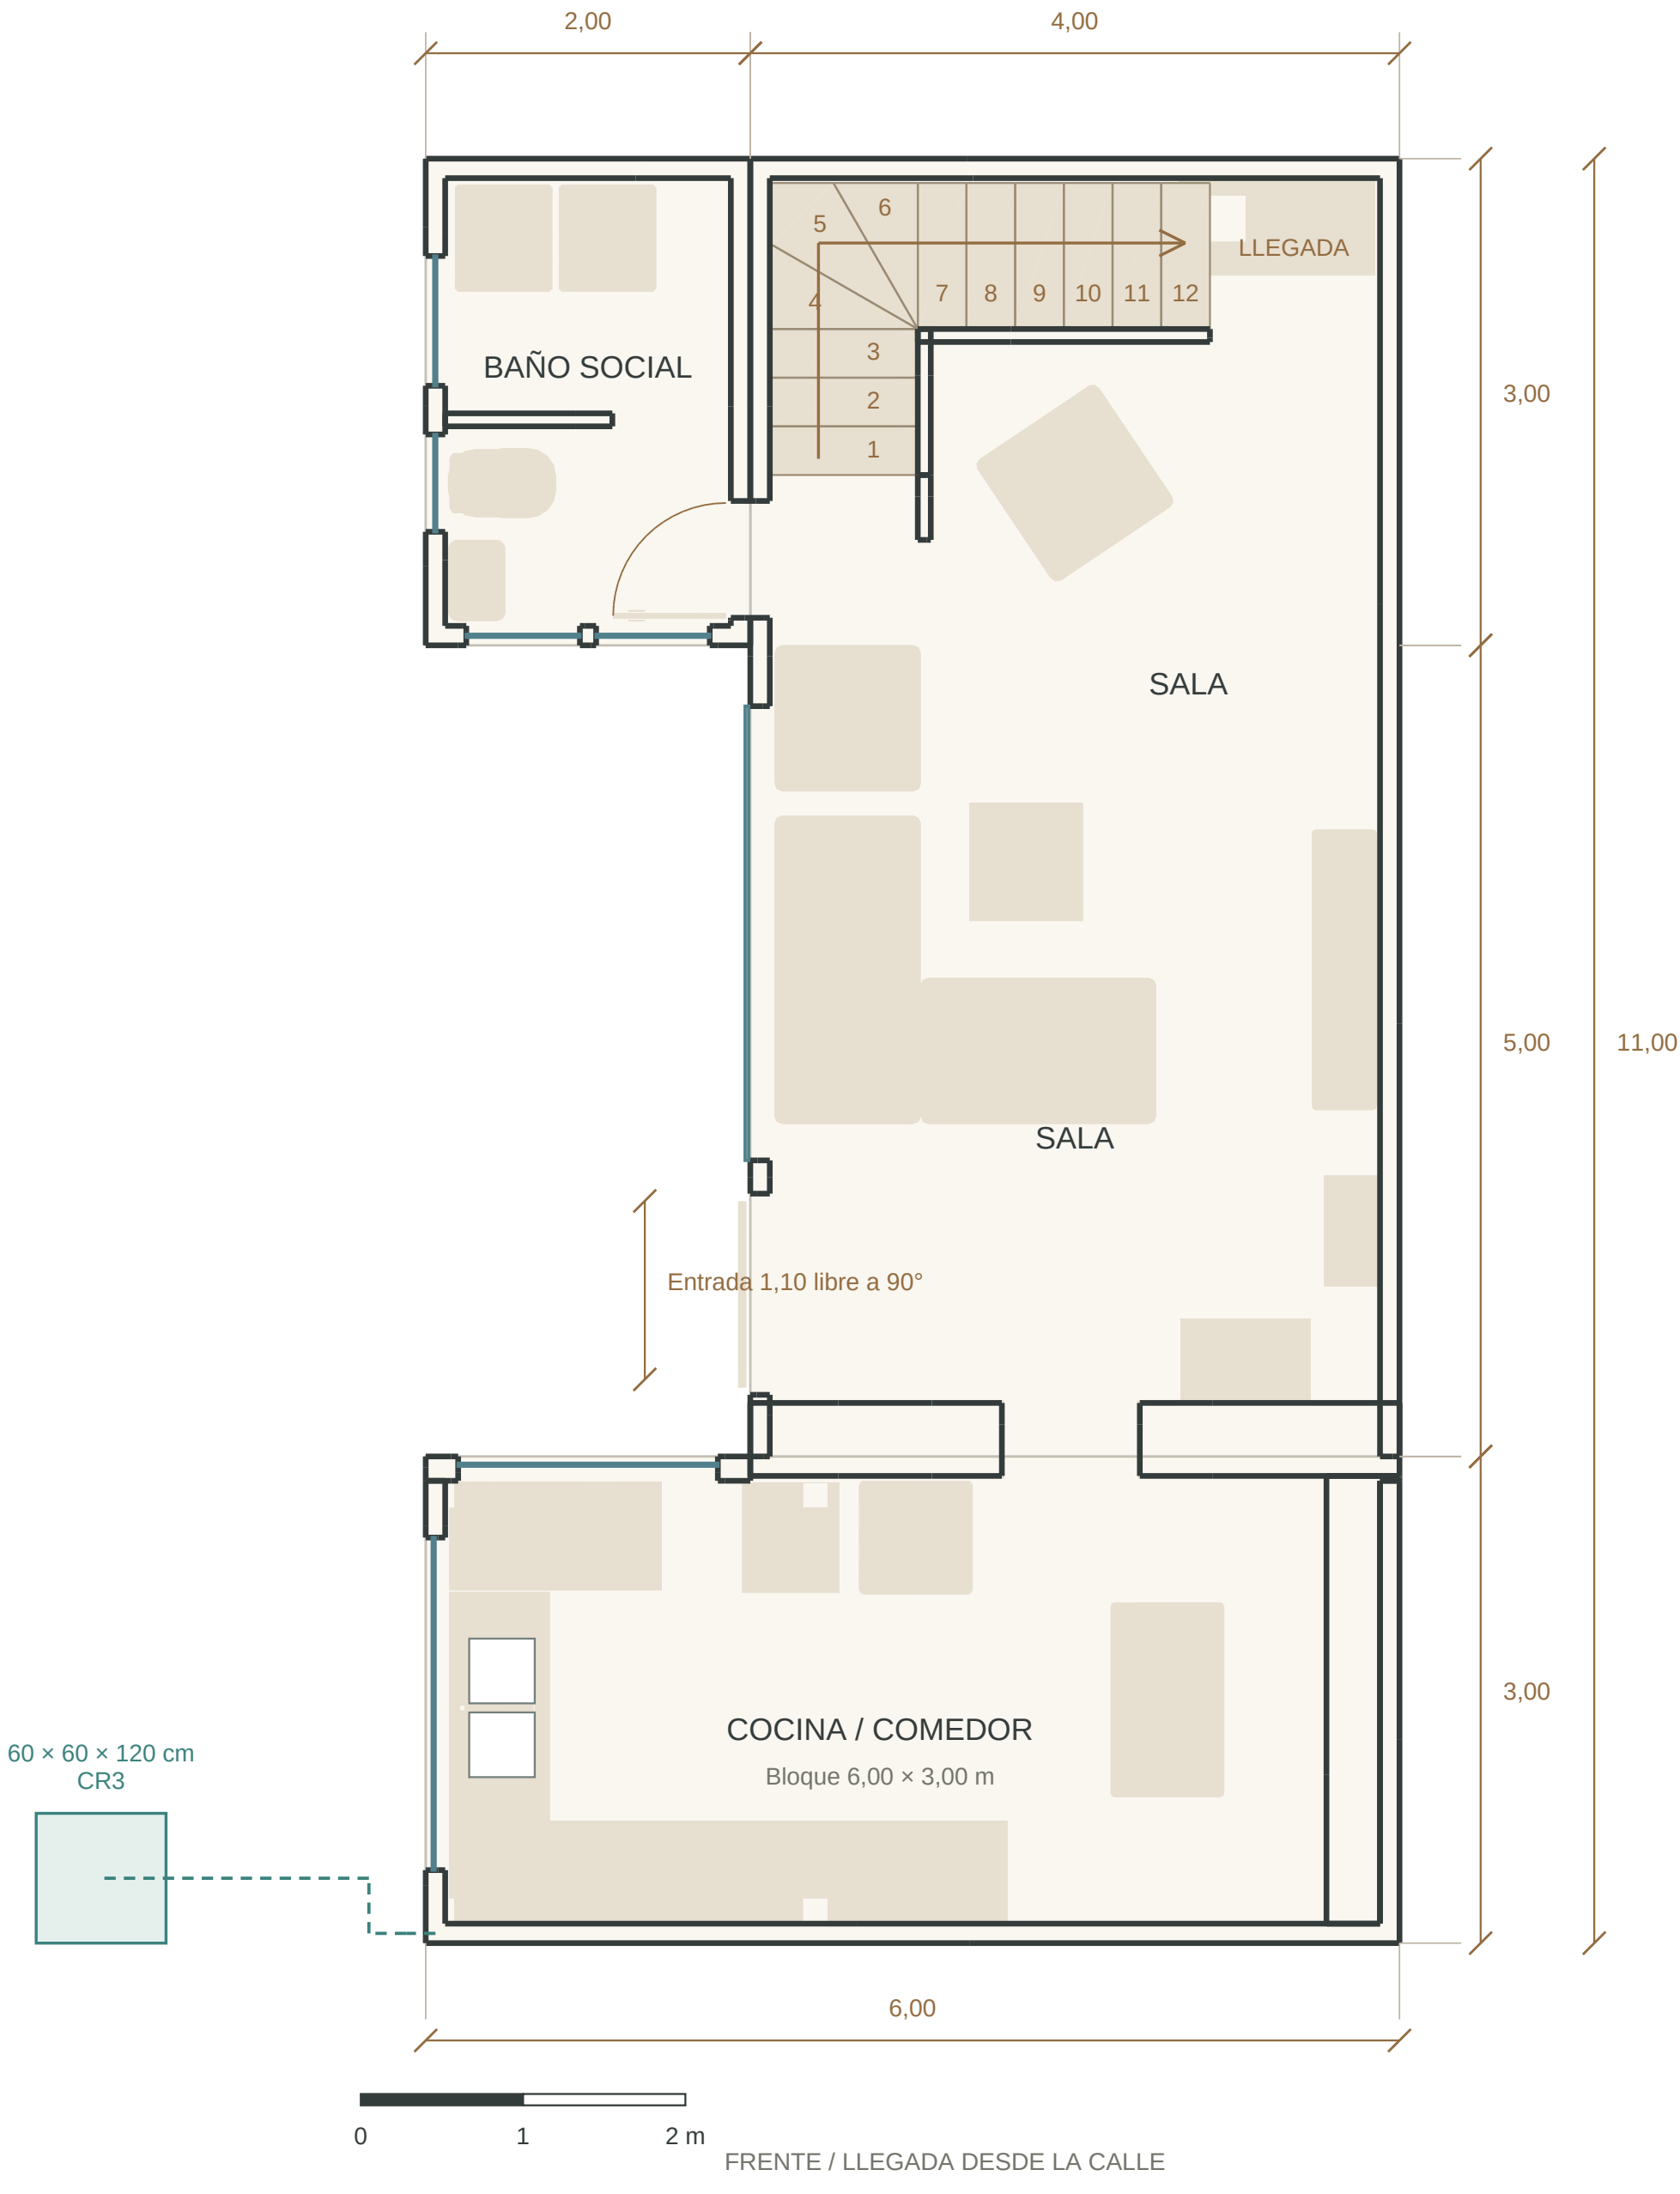

A-08 · Entrada · paso libre y traslado de sillones

CASA LALES · MAPA COMPLETO · ESCALA 1:25 · IMPRIMIR AL 100 %

Revisión 12/11/2026 · 22dd2a9a

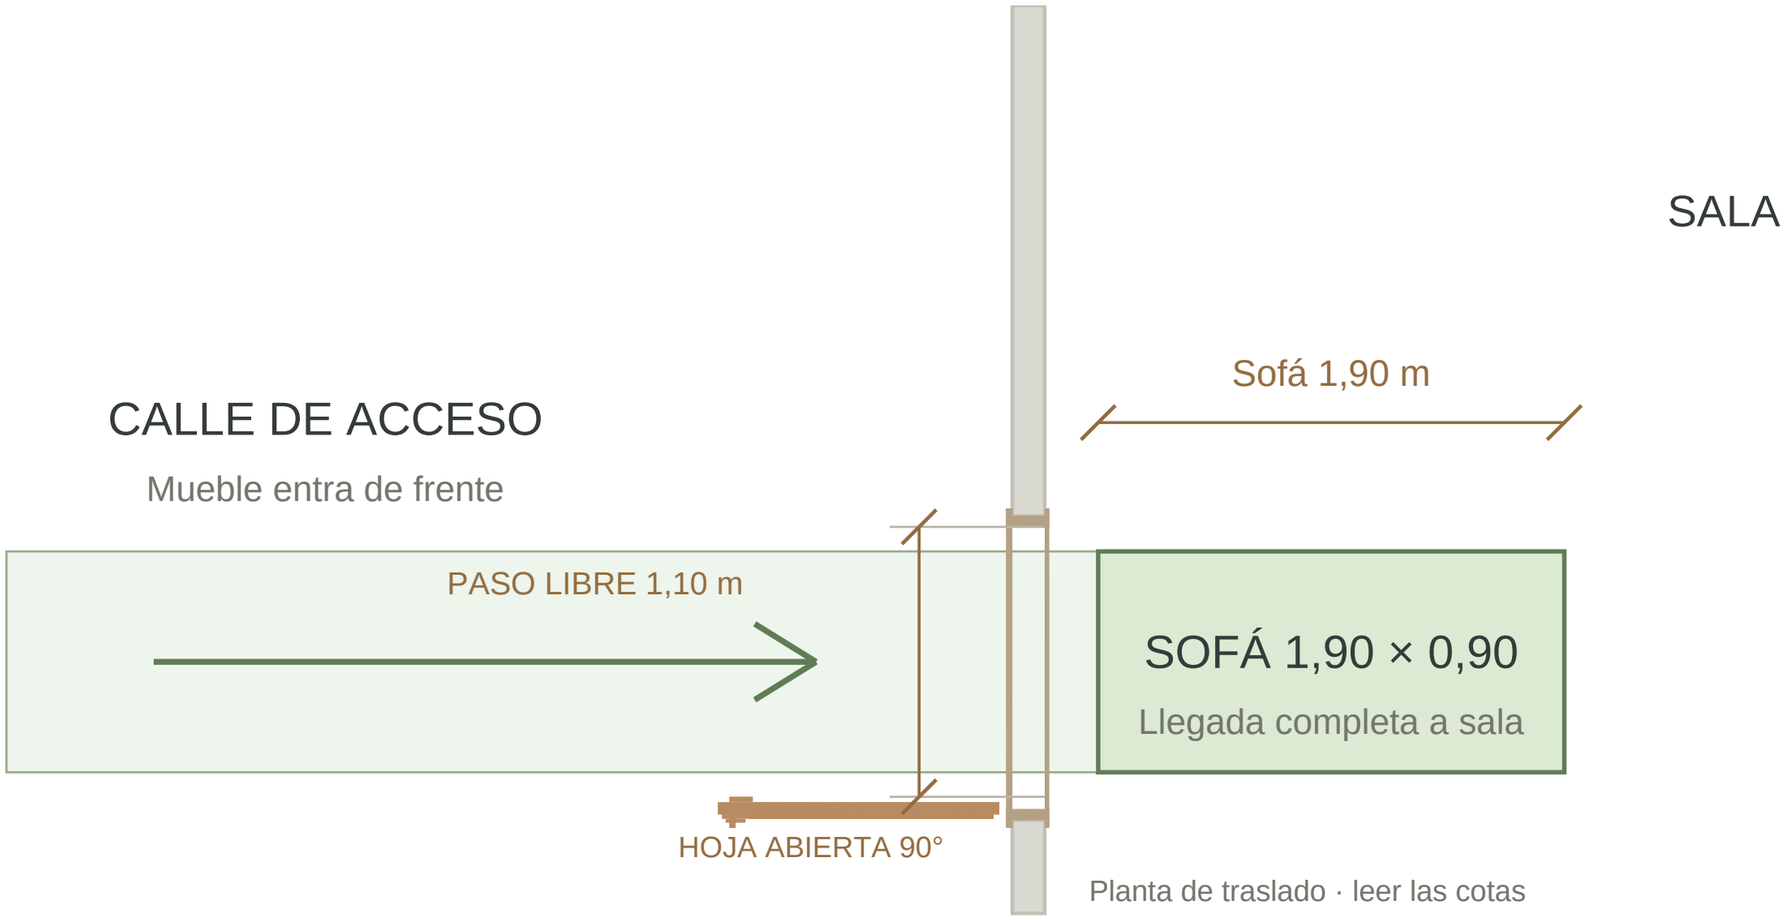


Planta de traslado · leer las cotas

A-03 · Planta alta · dormitorio, estudio y balcón

CASA LALES · MAPA COMPLETO · ESCALA 1:40 · IMPRIMIR AL 100 %


Revisión 12/11/2026 · 22dd2a9a

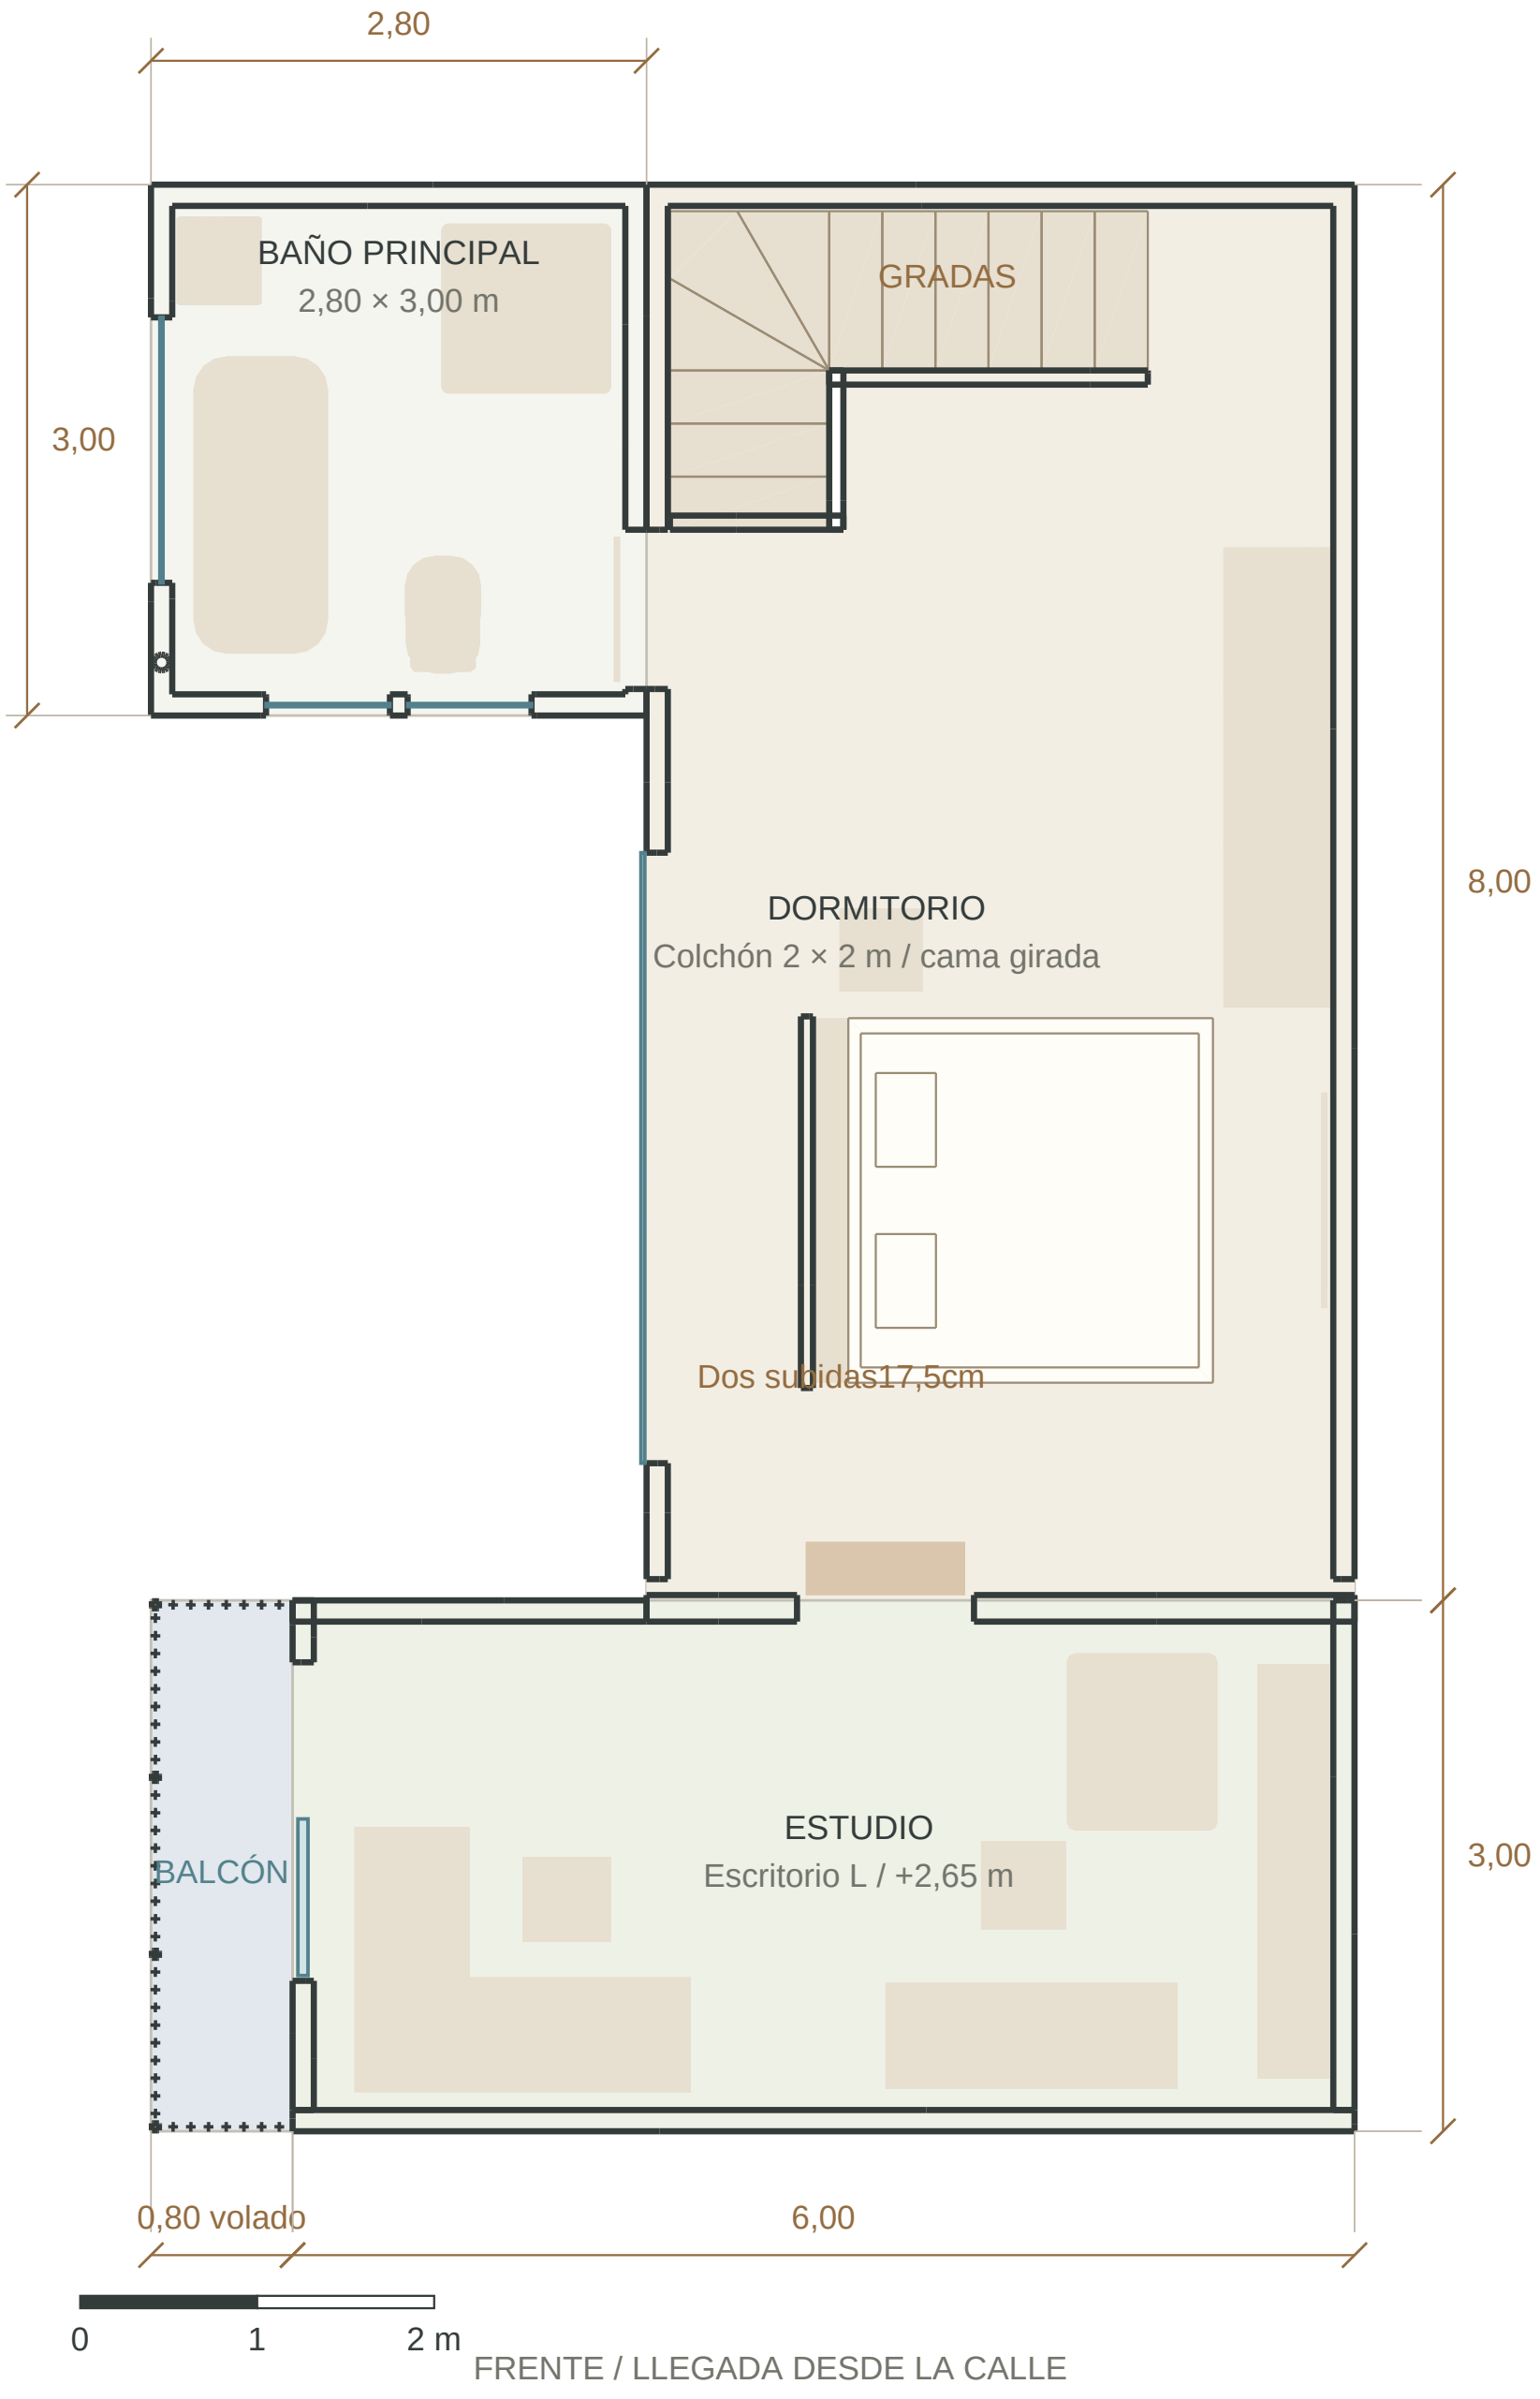

A-04 · Patio · baño, bodega y asadero

CASA LALES · MAPA COMPLETO · ESCALA 1:40 · IMPRIMIR AL 100 %


Revisión 12/11/2026 · 22dd2a9a

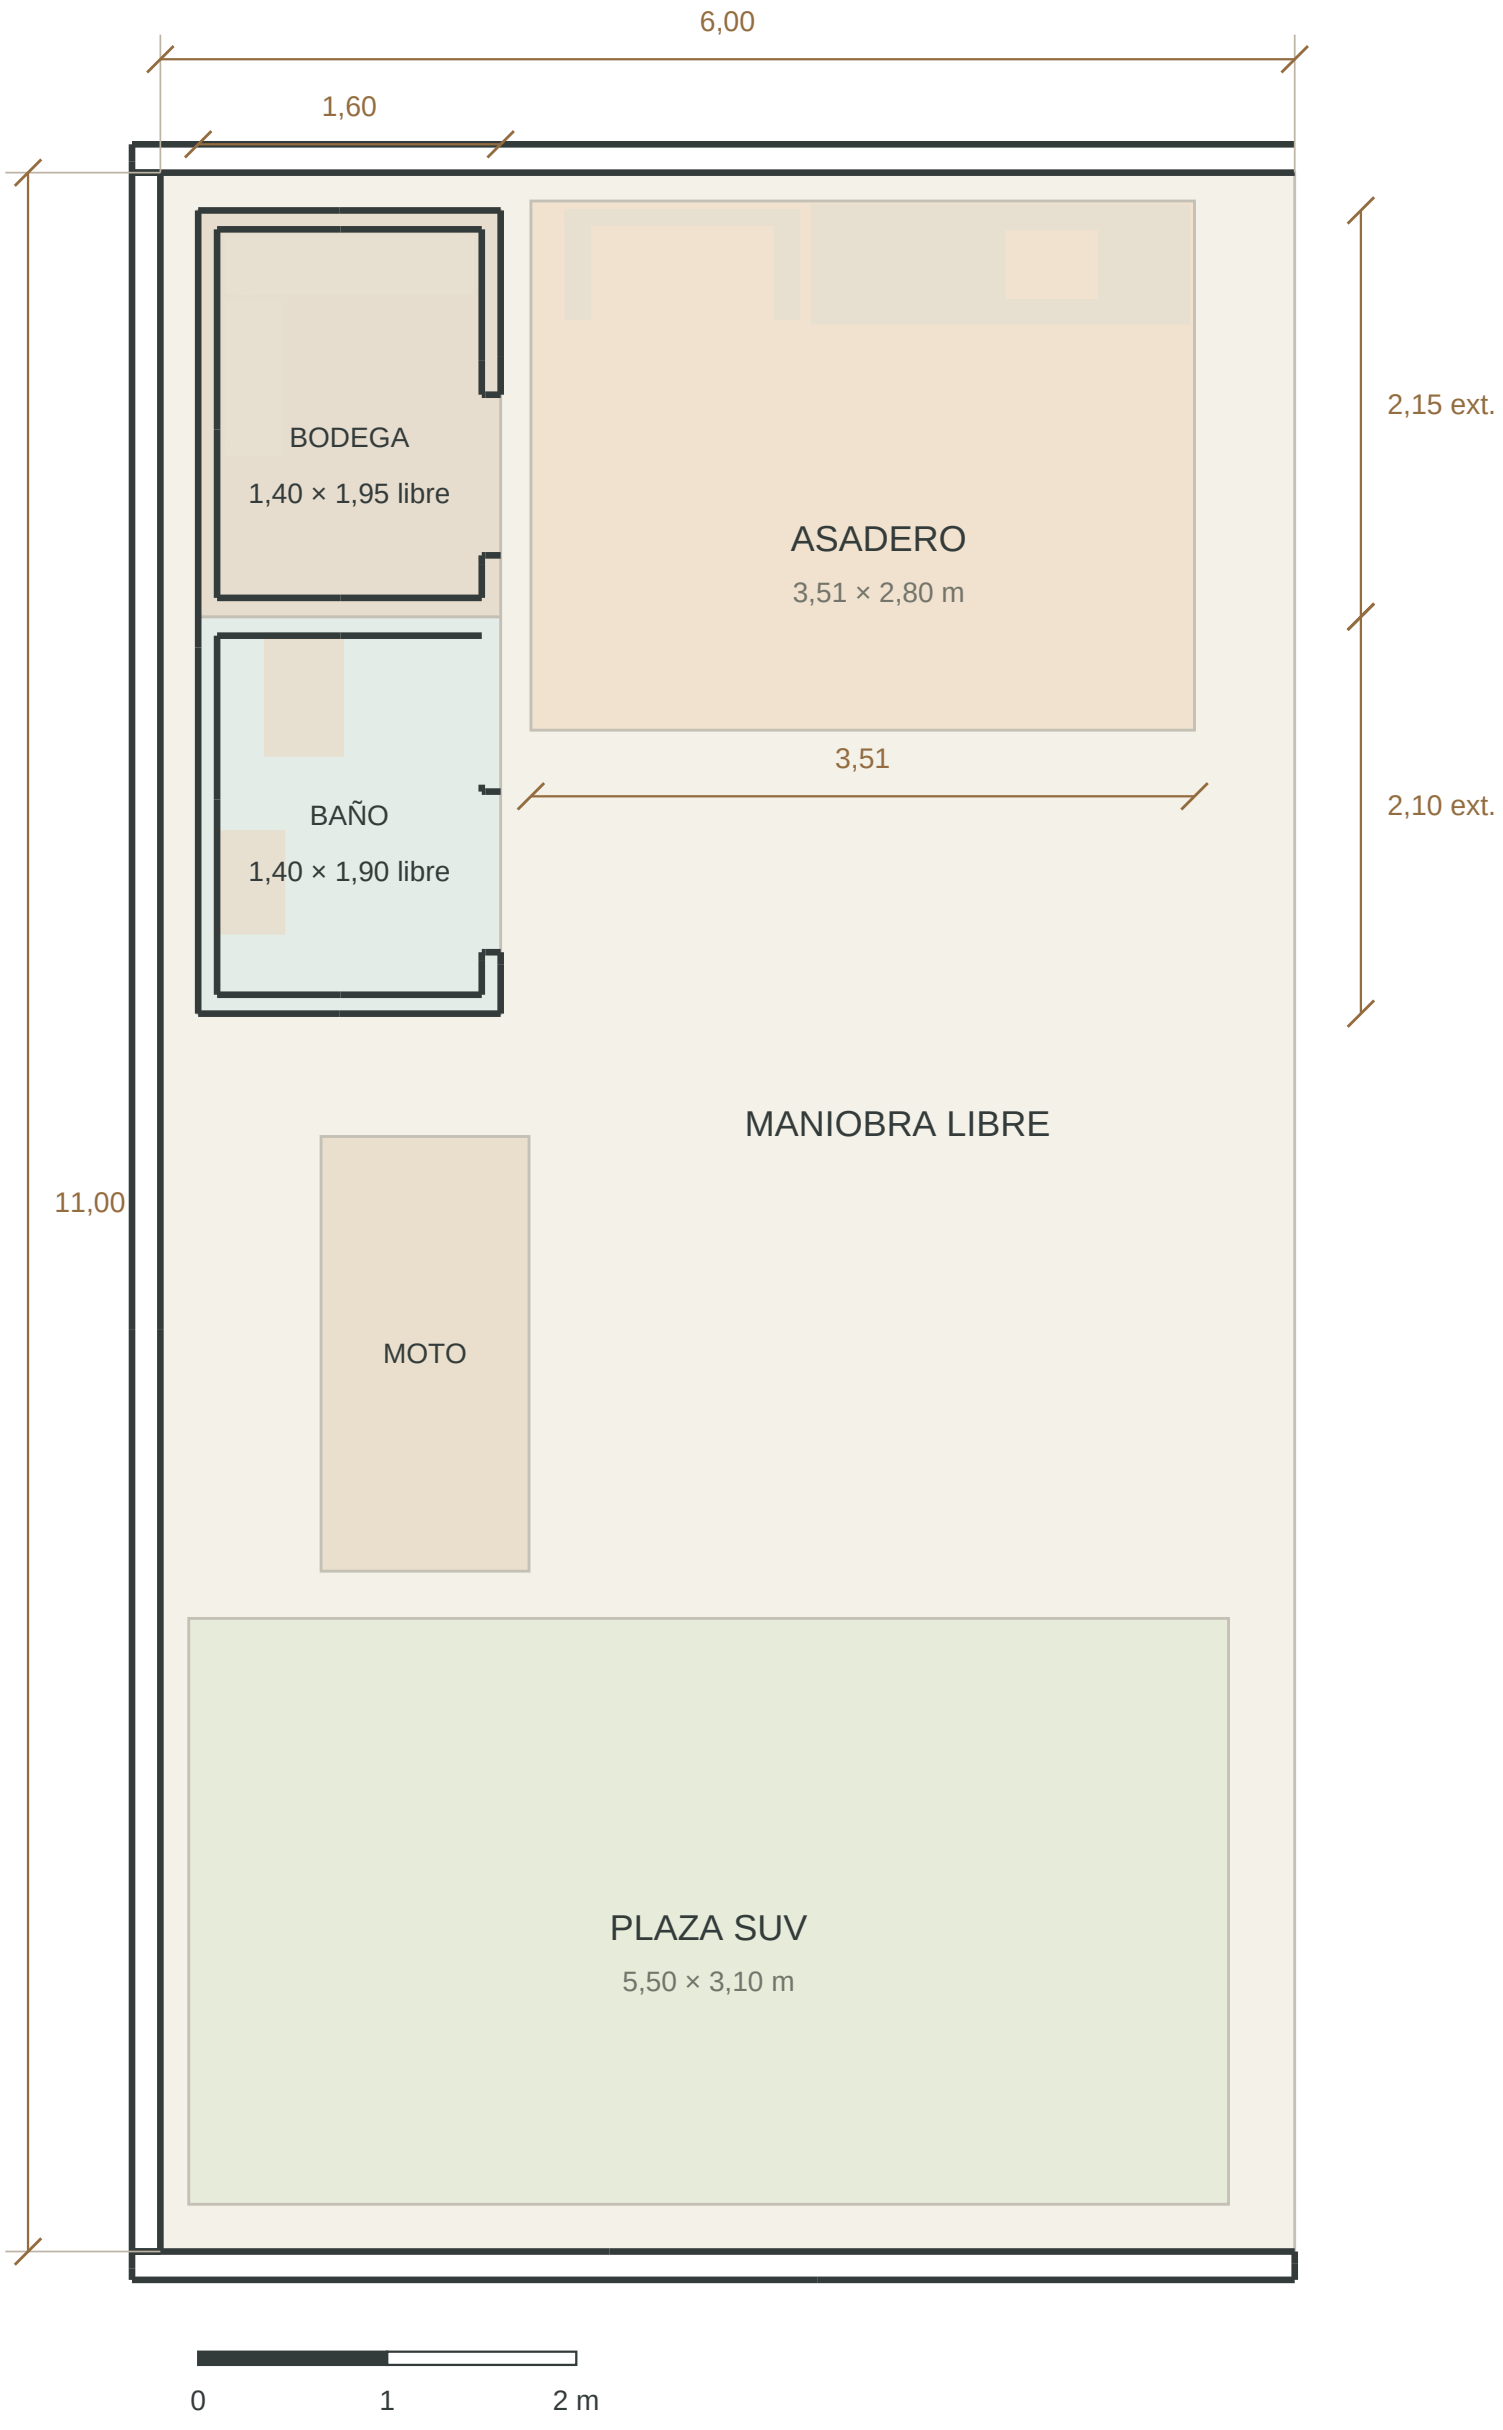

E-01T · Tomacorrientes y equipos · Planta baja

CASA LALES · MAPA COMPLETO · ESCALA 1:40 · IMPRIMIR AL 100 %

Revisión 12/11/2026 · 22dd2a9a

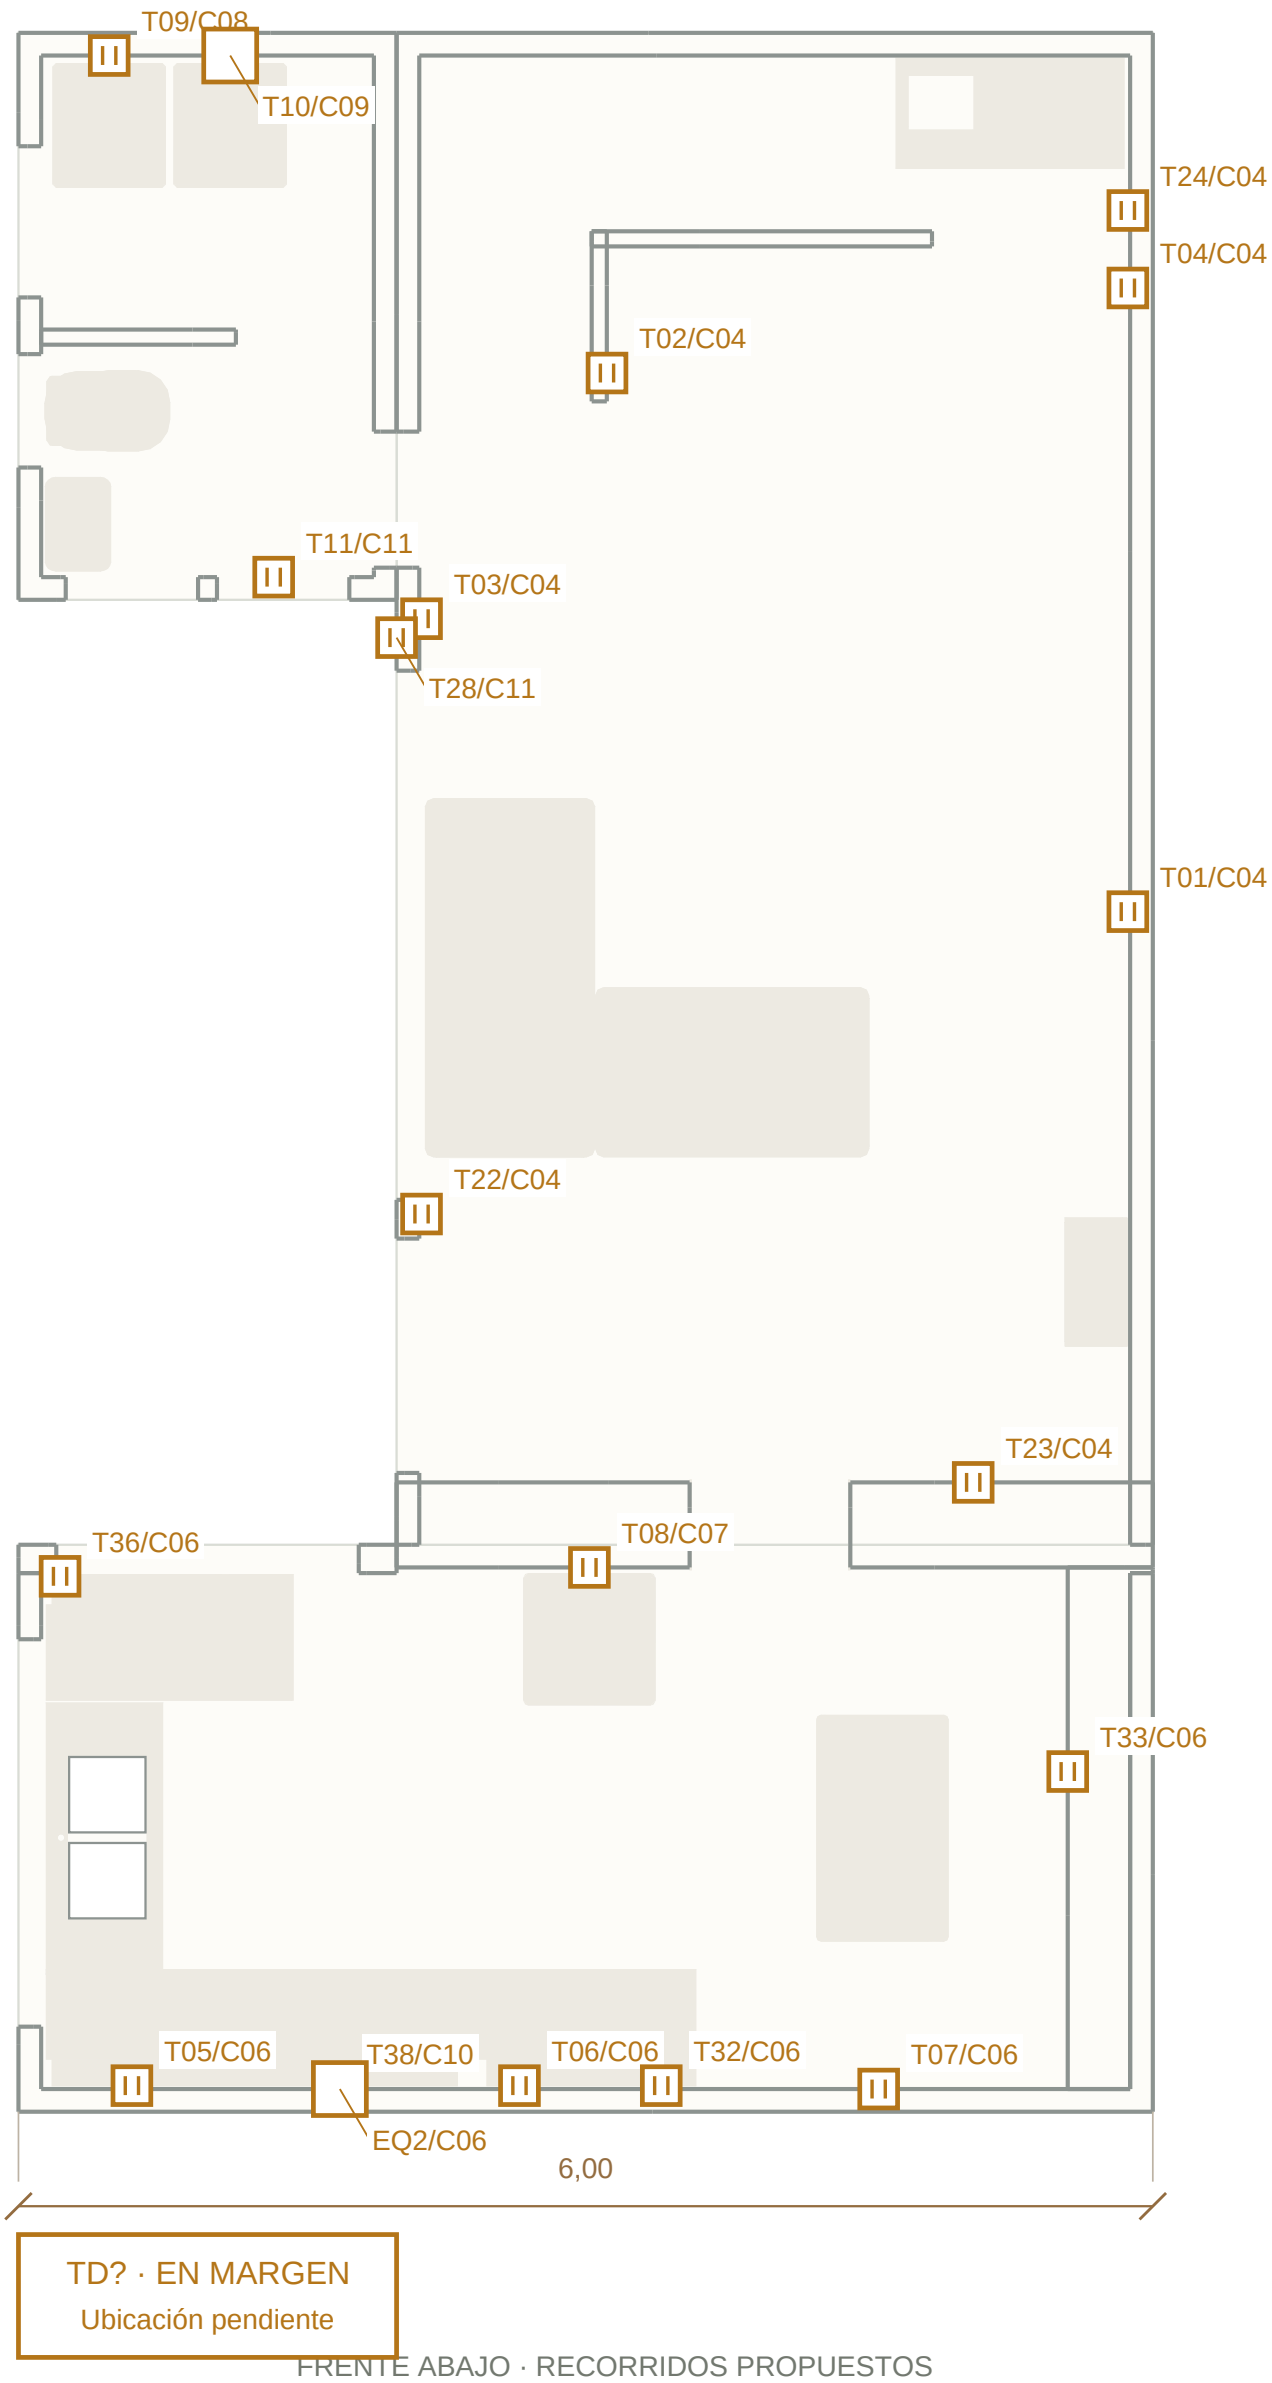

Simbología y notas en la hoja siguiente.

EXPLICACIÓN · E-01T

Tomacorrientes y equipos · Planta baja

Casa Lales · Revisión 12/11/2026 · 22dd2a9a

QUÉ SIGNIFICA CADA FIGURA



Cuadrado con dos rayas · T

Tomacorriente. Código T y grupo C coinciden con el visor 3D; no indican voltaje ni amperaje.



Cuadrado vacío · reserva

EQ1: cocción; EQ2: campana. T10: conexión de secadora por definir según equipo.



Líneas grises · muro

Paredes del modelo como referencia para situar los puntos.



C04-C11 · grupo funcional

El sufijo /C identifica un uso propuesto, sujeto al cálculo de cargas y protecciones.



Rectángulo TD? · tablero

Se dibuja al margen. La ubicación y las protecciones siguen pendientes.



Figura beige · mueble o aparato

Huella de referencia; se conservan las posiciones del modelo.

DATOS Y CRITERIOS DEL PLANO

Tomacorrientes: 19 puntos

Códigos T conservados. /C identifica grupo funcional; no es voltaje ni capacidad.

Reservas de equipos: 1 cajas

EQ: conexión de equipo por definir. T10 sigue identificado como reserva para secadora.

Plano de luces y mandos: E-01L

Consultar su mapa independiente; no se representan aquí sus símbolos.

NOTAS PARA REVISIÓN EN OBRA

Mismas posiciones y códigos que en imágenes 3D; alturas propuestas. Cabezal sin instalaciones.

Dimensiones y capacidades de conductores, protecciones y puesta a tierra pendientes de cálculo.


T10 es caja de conexión por definir según secadora; no se asigna tensión.

Baños y exterior: posición, protección y equipo apropiado por validar.

E-01L · Iluminación y mandos · Planta baja

CASA LALES · MAPA COMPLETO · ESCALA 1:40 · IMPRIMIR AL 100 %

Revisión 12/11/2026 · 22dd2a9a

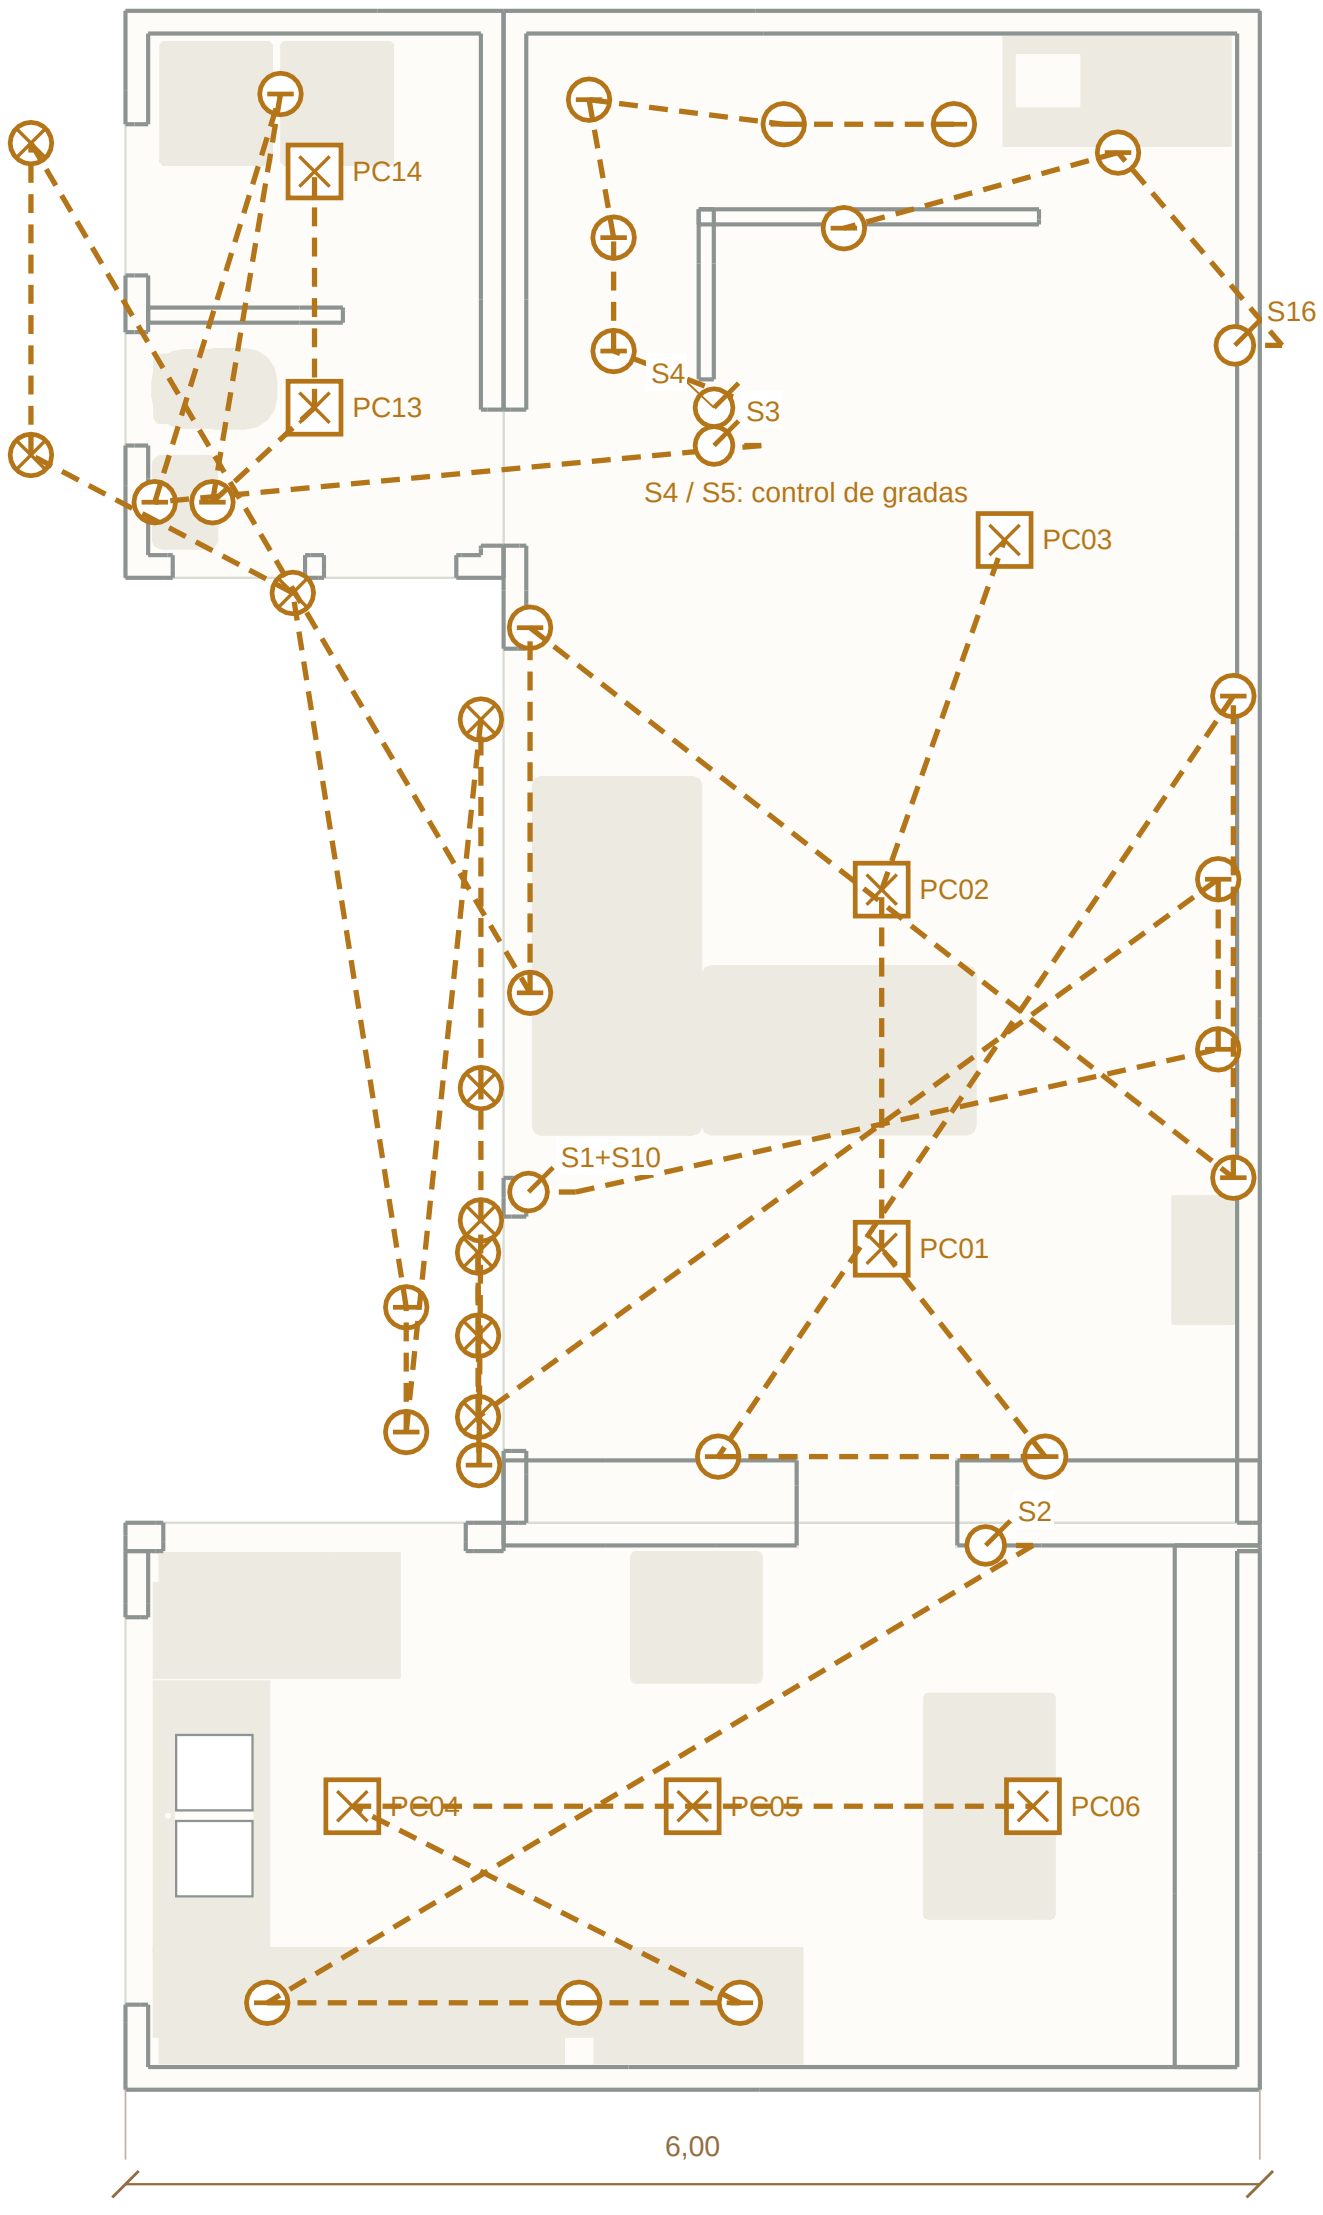

FRENTE ABAJO · RECORRIDOS PROPUESTOS

Simbología y notas en la hoja siguiente.

EXPLICACIÓN · E-01L

Iluminación y mandos · Planta baja

Casa Lales · Revisión 12/11/2026 · 22dd2a9a

QUÉ SIGNIFICA CADA FIGURA

Cuadrado con X · plafón PC
Lámpara cuadrada de sobreponer. Cada código PC identifica una unidad; potencia y temperatura en el cuadro de esta hoja.

Círculo con X · luz general
Punto de iluminación general del modelo. No equivale siempre a una unidad comercial.

Círculo con raya · luz de apoyo
Referencia de trabajo o ambiente: LED, espejo, mueble, aplique o escalón.

Círculo con trazo · S
Interruptor o caja de teclas. Misma posición y código que el visor; S4/S5 coordinan las gradas.

Línea punteada · relación de mando
Relaciona el mando con sus luces. No fija un cableado, conductores ni trayecto de ejecución.

Líneas grises · muro
Paredes del modelo como referencia para situar los puntos.

Figura beige · mueble o aparato
Huella de referencia; se conservan las posiciones del modelo.

DATOS Y CRITERIOS DEL PLANO

Iluminación general: 8 plafones PC / 9 otros
Cuadrado con X: plafón PC; círculo con X: otra luz general.

Luz de trabajo / ambiente: 24 referencias
Círculo con raya; incluye LED, apliques y apoyos.

Cajas de mandos: S1+S10, S2, S3, S4, S16
S4/S5: coordinar el control de gradas desde ambos niveles.

Plano de tomacorrientes: E-01T
Consultar su mapa independiente; no se representan aquí sus símbolos.

Sala: 3 × 24 W · 3000 K
Interior seco

Cocina y comedor: 3 × 24 W · 4000 K
Interior seco

Baño social y lavandería: 2 × 12 W · 4000 K
Sellado para zona húmeda; por confirmar

NOTAS PARA REVISIÓN EN OBRA

Mismas tomas y mandos que en imágenes 3D. Alturas propuestas; dormitorio según distribución aplicada.

Líneas punteadas: relación de mando y recorrido conceptual; no son número de conductores.

Grupos C01-C12 funcionales: dividir por planta, cargas y protecciones en cálculo. Tablero y tierra pendientes.

Bajo Eternit: canalización y cajas fijadas a soporte definido, nunca a las planchas.

Las luces de gradas se asignan a PB o PA por cota: cada referencia aparece una sola vez.

PC: plafón cuadrado sobrepuesto. Modelo seco de referencia 28,5 × 28,5 × 2,8 cm, 24 W, 1800 lm, 0,583 kg; 100–240 V. Confirmar equipo y suministro.

Fijar herraje a perfil/refuerzo del cielo; no cargar sólo la placa. Revisar perfilería, anclaje y acceso al driver; no suspender del Eternit.


Baños: variante sellada IP44 mínimo; IP65 si la zona lo exige. Potencia y formato menores orientativos; modelo y protección por elegir.

Plafón de referencia sin dimmer. LED indirecto y tarea separados. Cantidad propuesta; verificar iluminación con fotometría y medidas reales.

E-02T · Tomacorrientes y equipos · Planta alta

CASA LALES · MAPA COMPLETO · ESCALA 1:40 · IMPRIMIR AL 100 %

Revisión 12/11/2026 · 22dd2a9a

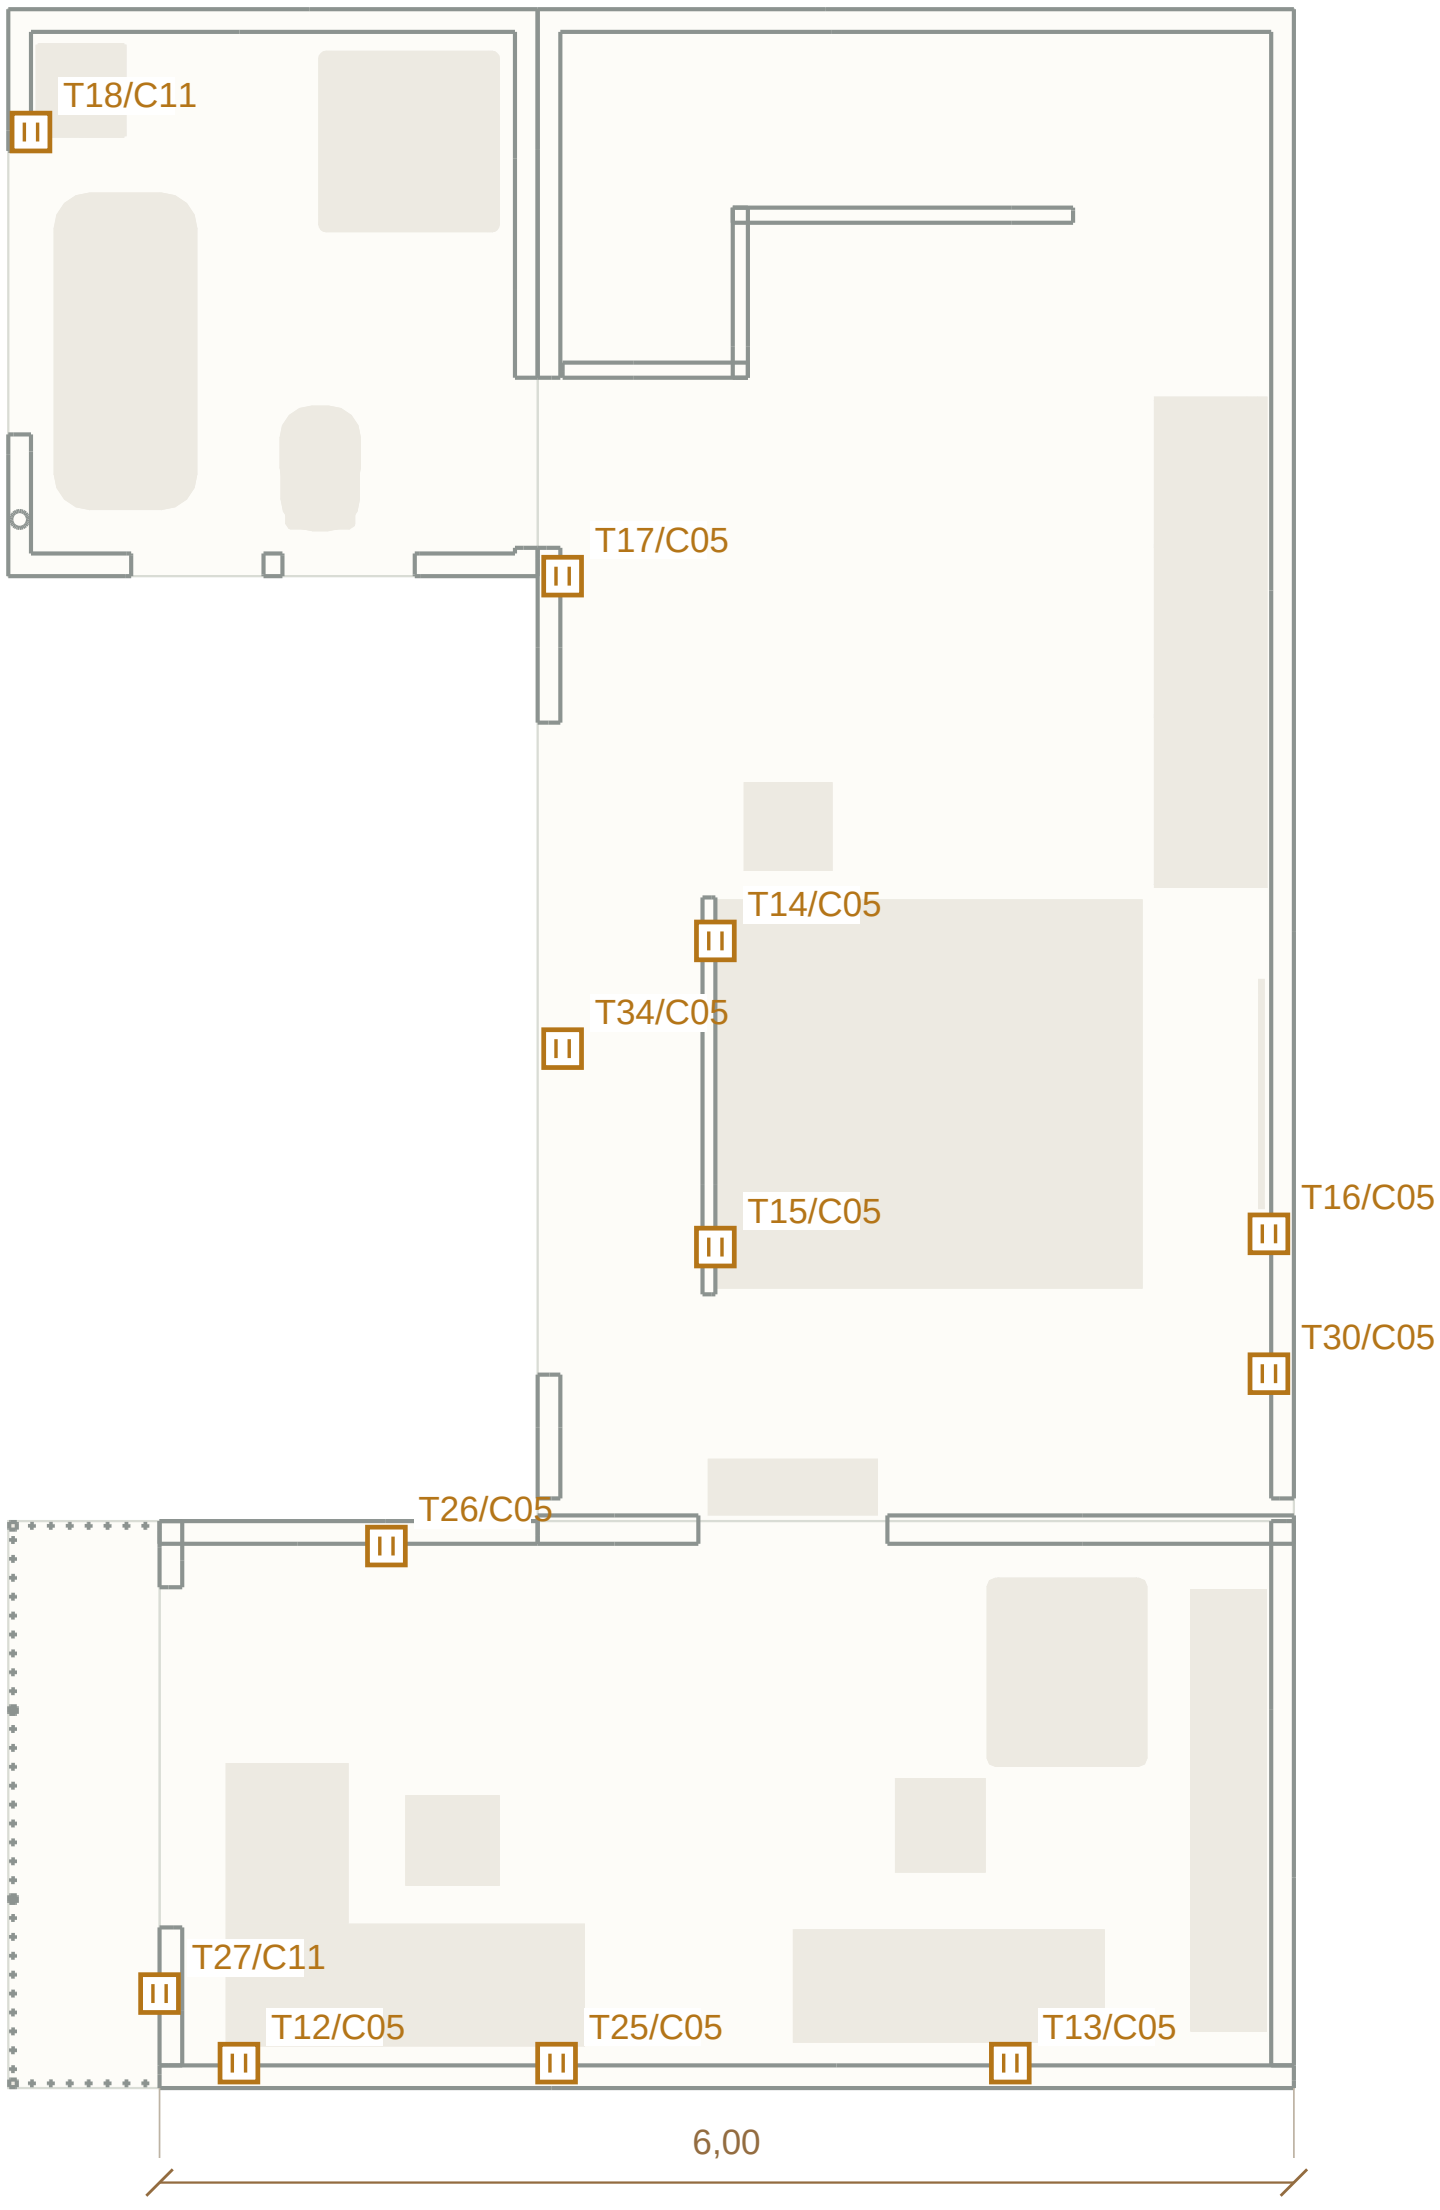

FRENTE ABAJO · RECORRIDOS PROPUESTOS

Simbología y notas en la hoja siguiente.

EXPLICACIÓN · E-02T

Tomacorrientes y equipos · Planta alta

Casa Lales · Revisión 12/11/2026 · 22dd2a9a

QUÉ SIGNIFICA CADA FIGURA



Cuadrado con dos rayas · T

Tomacorriente. Código T y grupo C coinciden con el visor 3D; no indican voltaje ni amperaje.

C01

C04-C11 · grupo funcional

El sufijo /C identifica un uso propuesto, sujeto al cálculo de cargas y protecciones.



Líneas grises · muro

Paredes del modelo como referencia para situar los puntos.



Figura beige · mueble o aparato

Huella de referencia; se conservan las posiciones del modelo.

DATOS Y CRITERIOS DEL PLANO

Tomacorrientes: 12 puntos

Códigos T conservados. /C identifica grupo funcional; no es voltaje ni capacidad.

Reservas de equipos: 0 cajas

No hay cajas EQ adicionales en este nivel.

Plano de luces y mandos: E-02L

Consultar su mapa independiente; no se representan aquí sus símbolos.

NOTAS PARA REVISIÓN EN OBRA

Mismas posiciones y códigos que en imágenes 3D; alturas propuestas. Cabezal sin instalaciones.


Dimensiones y capacidades de conductores, protecciones y puesta a tierra pendientes de cálculo.

Baños y exterior: posición, protección y equipo apropiado por validar.

E-02L · Iluminación y mandos · Planta alta

CASA LALES · MAPA COMPLETO · ESCALA 1:40 · IMPRIMIR AL 100 %

Revisión 12/11/2026 · 22dd2a9a

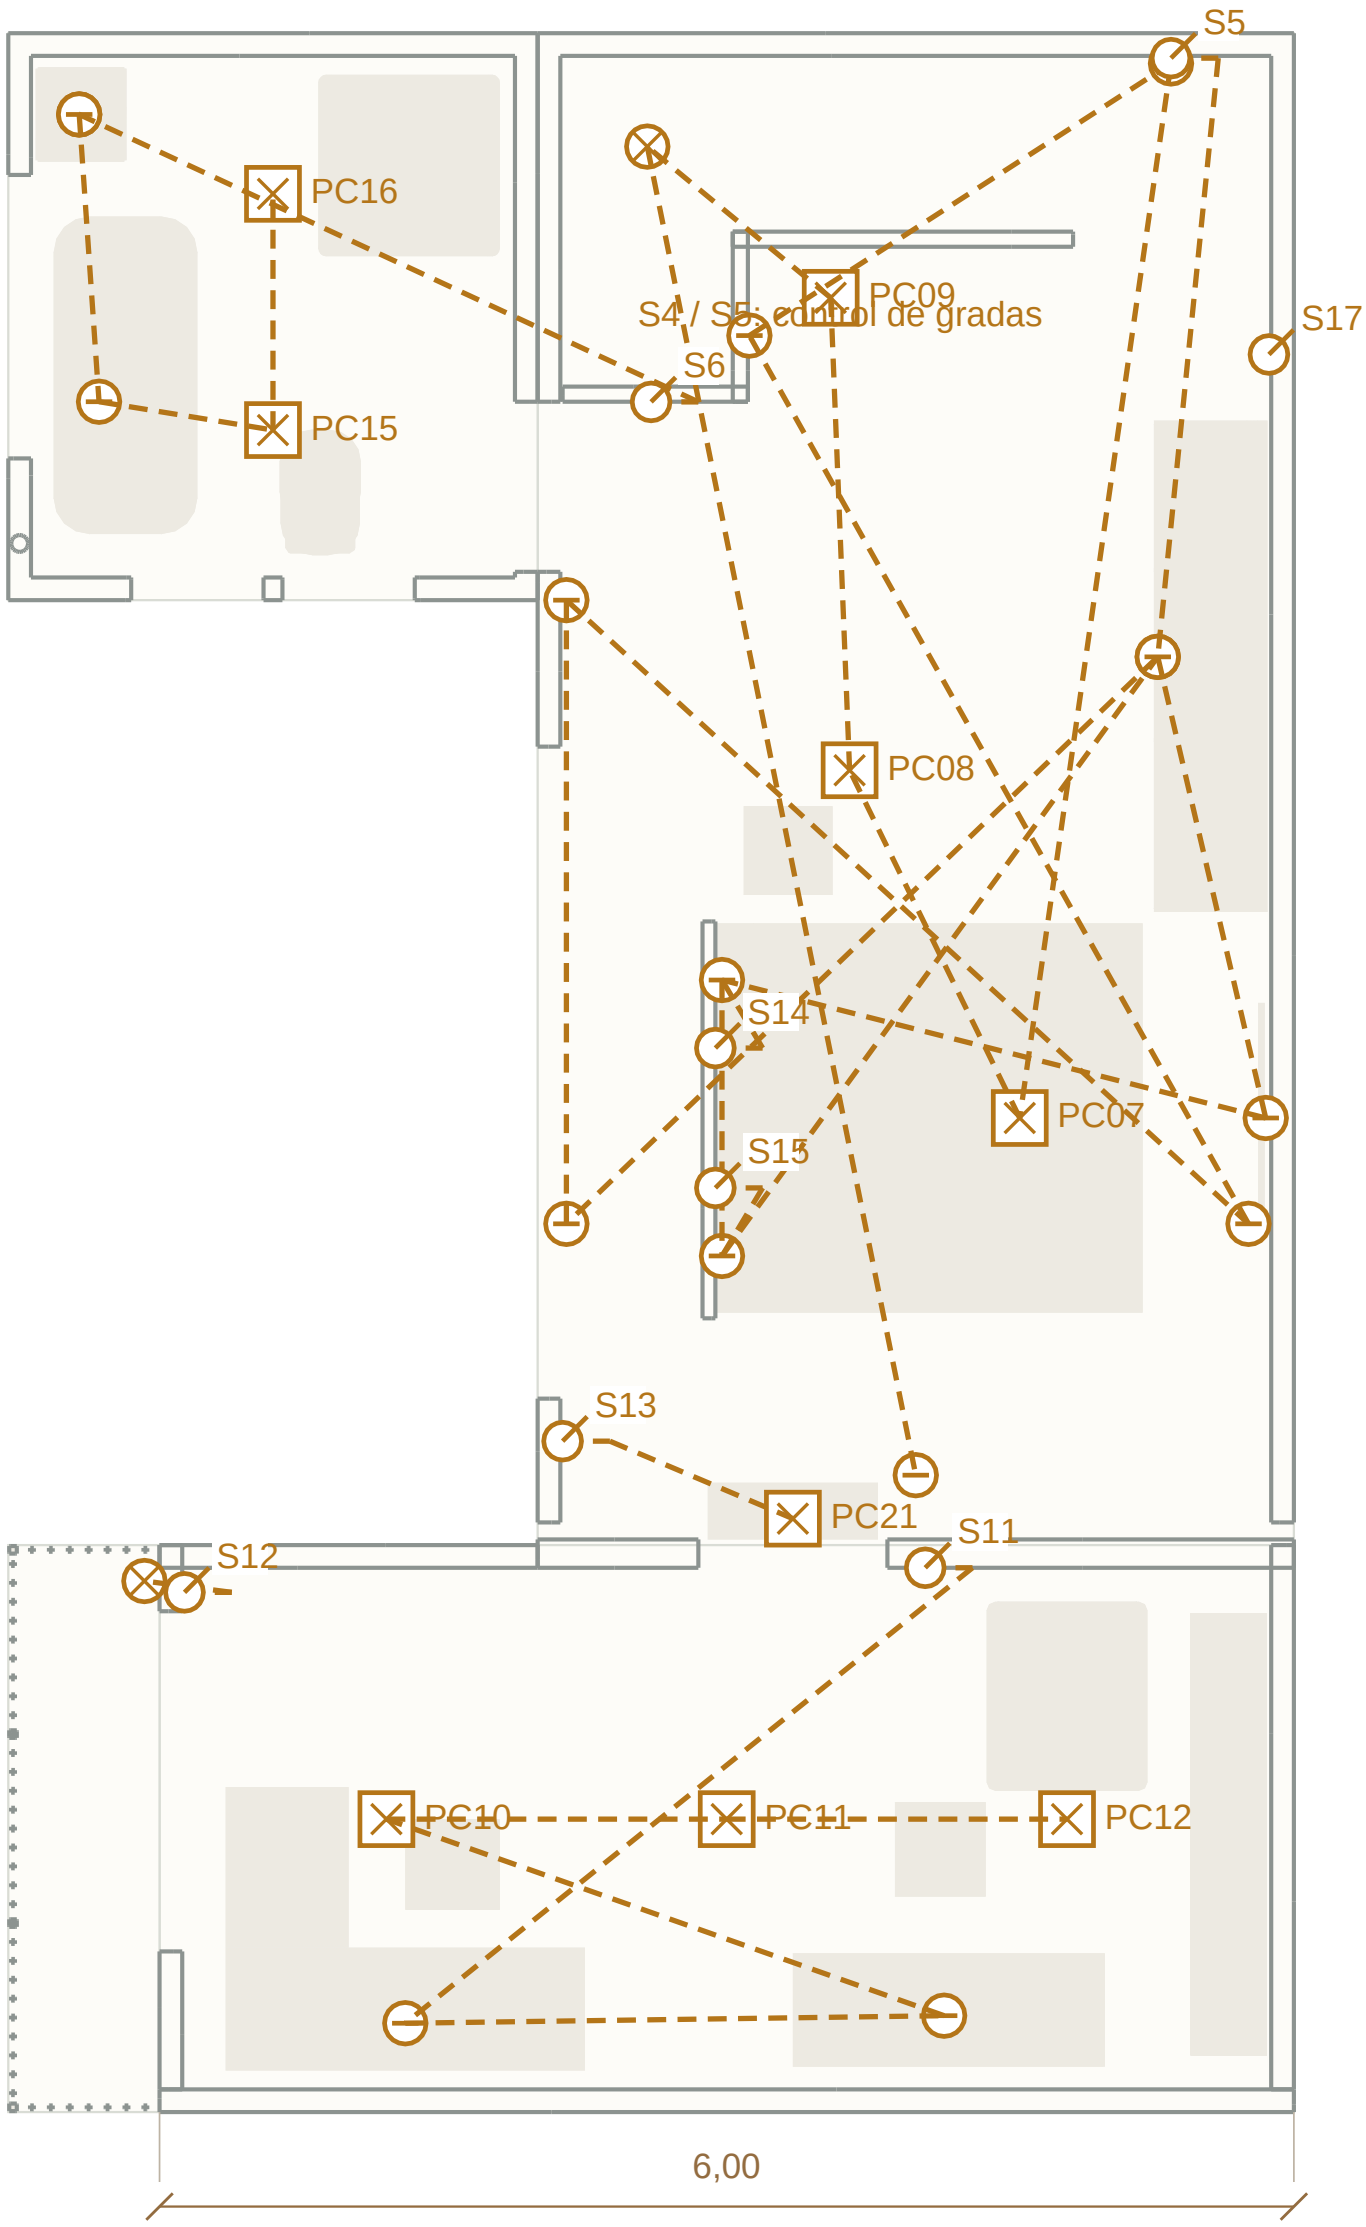

FRENTE ABAJO · RECORRIDOS PROPUESTOS

Simbología y notas en la hoja siguiente.

EXPLICACIÓN · E-02L

Iluminación y mandos · Planta alta

Casa Lales · Revisión 12/11/2026 · 22dd2a9a

QUÉ SIGNIFICA CADA FIGURA

Cuadrado con X · plafón PC
Lámpara cuadrada de sobreponer. Cada código PC identifica una unidad; potencia y temperatura en el cuadro de esta hoja.

Círculo con X · luz general
Punto de iluminación general del modelo. No equivale siempre a una unidad comercial.

Círculo con raya · luz de apoyo
Referencia de trabajo o ambiente: LED, espejo, mueble, aplique o escalón.

Círculo con trazo · S
Interruptor o caja de teclas. Misma posición y código que el visor; S4/S5 coordinan las gradas.

Línea punteada · relación de mando
Relaciona el mando con sus luces. No fija un cableado, conductores ni trayecto de ejecución.

Líneas grises · muro
Paredes del modelo como referencia para situar los puntos.

Figura beige · mueble o aparato
Huella de referencia; se conservan las posiciones del modelo.

DATOS Y CRITERIOS DEL PLANO

Iluminación general: 9 plafones PC / 2 otros
Cuadrado con X: plafón PC; círculo con X: otra luz general.

Luz de trabajo / ambiente: 16 referencias
Círculo con raya; incluye LED, apliques y apoyos.

Cajas de mandos: S5, S17, S6, S13, S14, S15, S11, S12
S4/S5: coordinar el control de gradas desde ambos niveles.

Plano de tomacorrientes: E-02T
Consultar su mapa independiente; no se representan aquí sus símbolos.

Dormitorio y armarios: 3 × 24 W · 3000 K
Interior seco

Estudio: 3 × 24 W · 4000 K
Interior seco

Baño principal: 2 × 18 W · 4000 K
Eternit hacia casa; inclinación 12,14% en boceto. Cielo libre 2,20 m. Producto y solución de baja pendiente por confirmar.

Acceso al estudio: 1 × 12 W · 3000 K
Interior seco

NOTAS PARA REVISIÓN EN OBRA

Mismas tomas y mandos que en imágenes 3D. Alturas propuestas; dormitorio según distribución aplicada.

Líneas punteadas: relación de mando y recorrido conceptual; no son número de conductores.

Grupos C01-C12 funcionales: dividir por planta, cargas y protecciones en cálculo. Tablero y tierra pendientes.

Bajo Eternit: canalización y cajas fijadas a soporte definido, nunca a las planchas.

Las luces de gradas se asignan a PB o PA por cota: cada referencia aparece una sola vez.

PC: plafón cuadrado sobrepuesto. Modelo seco de referencia 28,5 × 28,5 × 2,8 cm, 24 W, 1800 lm, 0,583 kg; 100–240 V. Confirmar equipo y suministro.

Fijar herraje a perfil/refuerzo del cielo; no cargar sólo la placa. Revisar perfilería, anclaje y acceso al driver; no suspender del Eternit.


Baños: variante sellada IP44 mínimo; IP65 si la zona lo exige. Potencia y formato menores orientativos; modelo y protección por elegir.

Plafón de referencia sin dimmer. LED indirecto y tarea separados. Cantidad propuesta; verificar iluminación con fotometría y medidas reales.

E-03T · Tomacorrientes y equipos · Patio

CASA LALES · MAPA COMPLETO · ESCALA 1:40 · IMPRIMIR AL 100 %

Revisión 12/11/2026 · 22dd2a9a

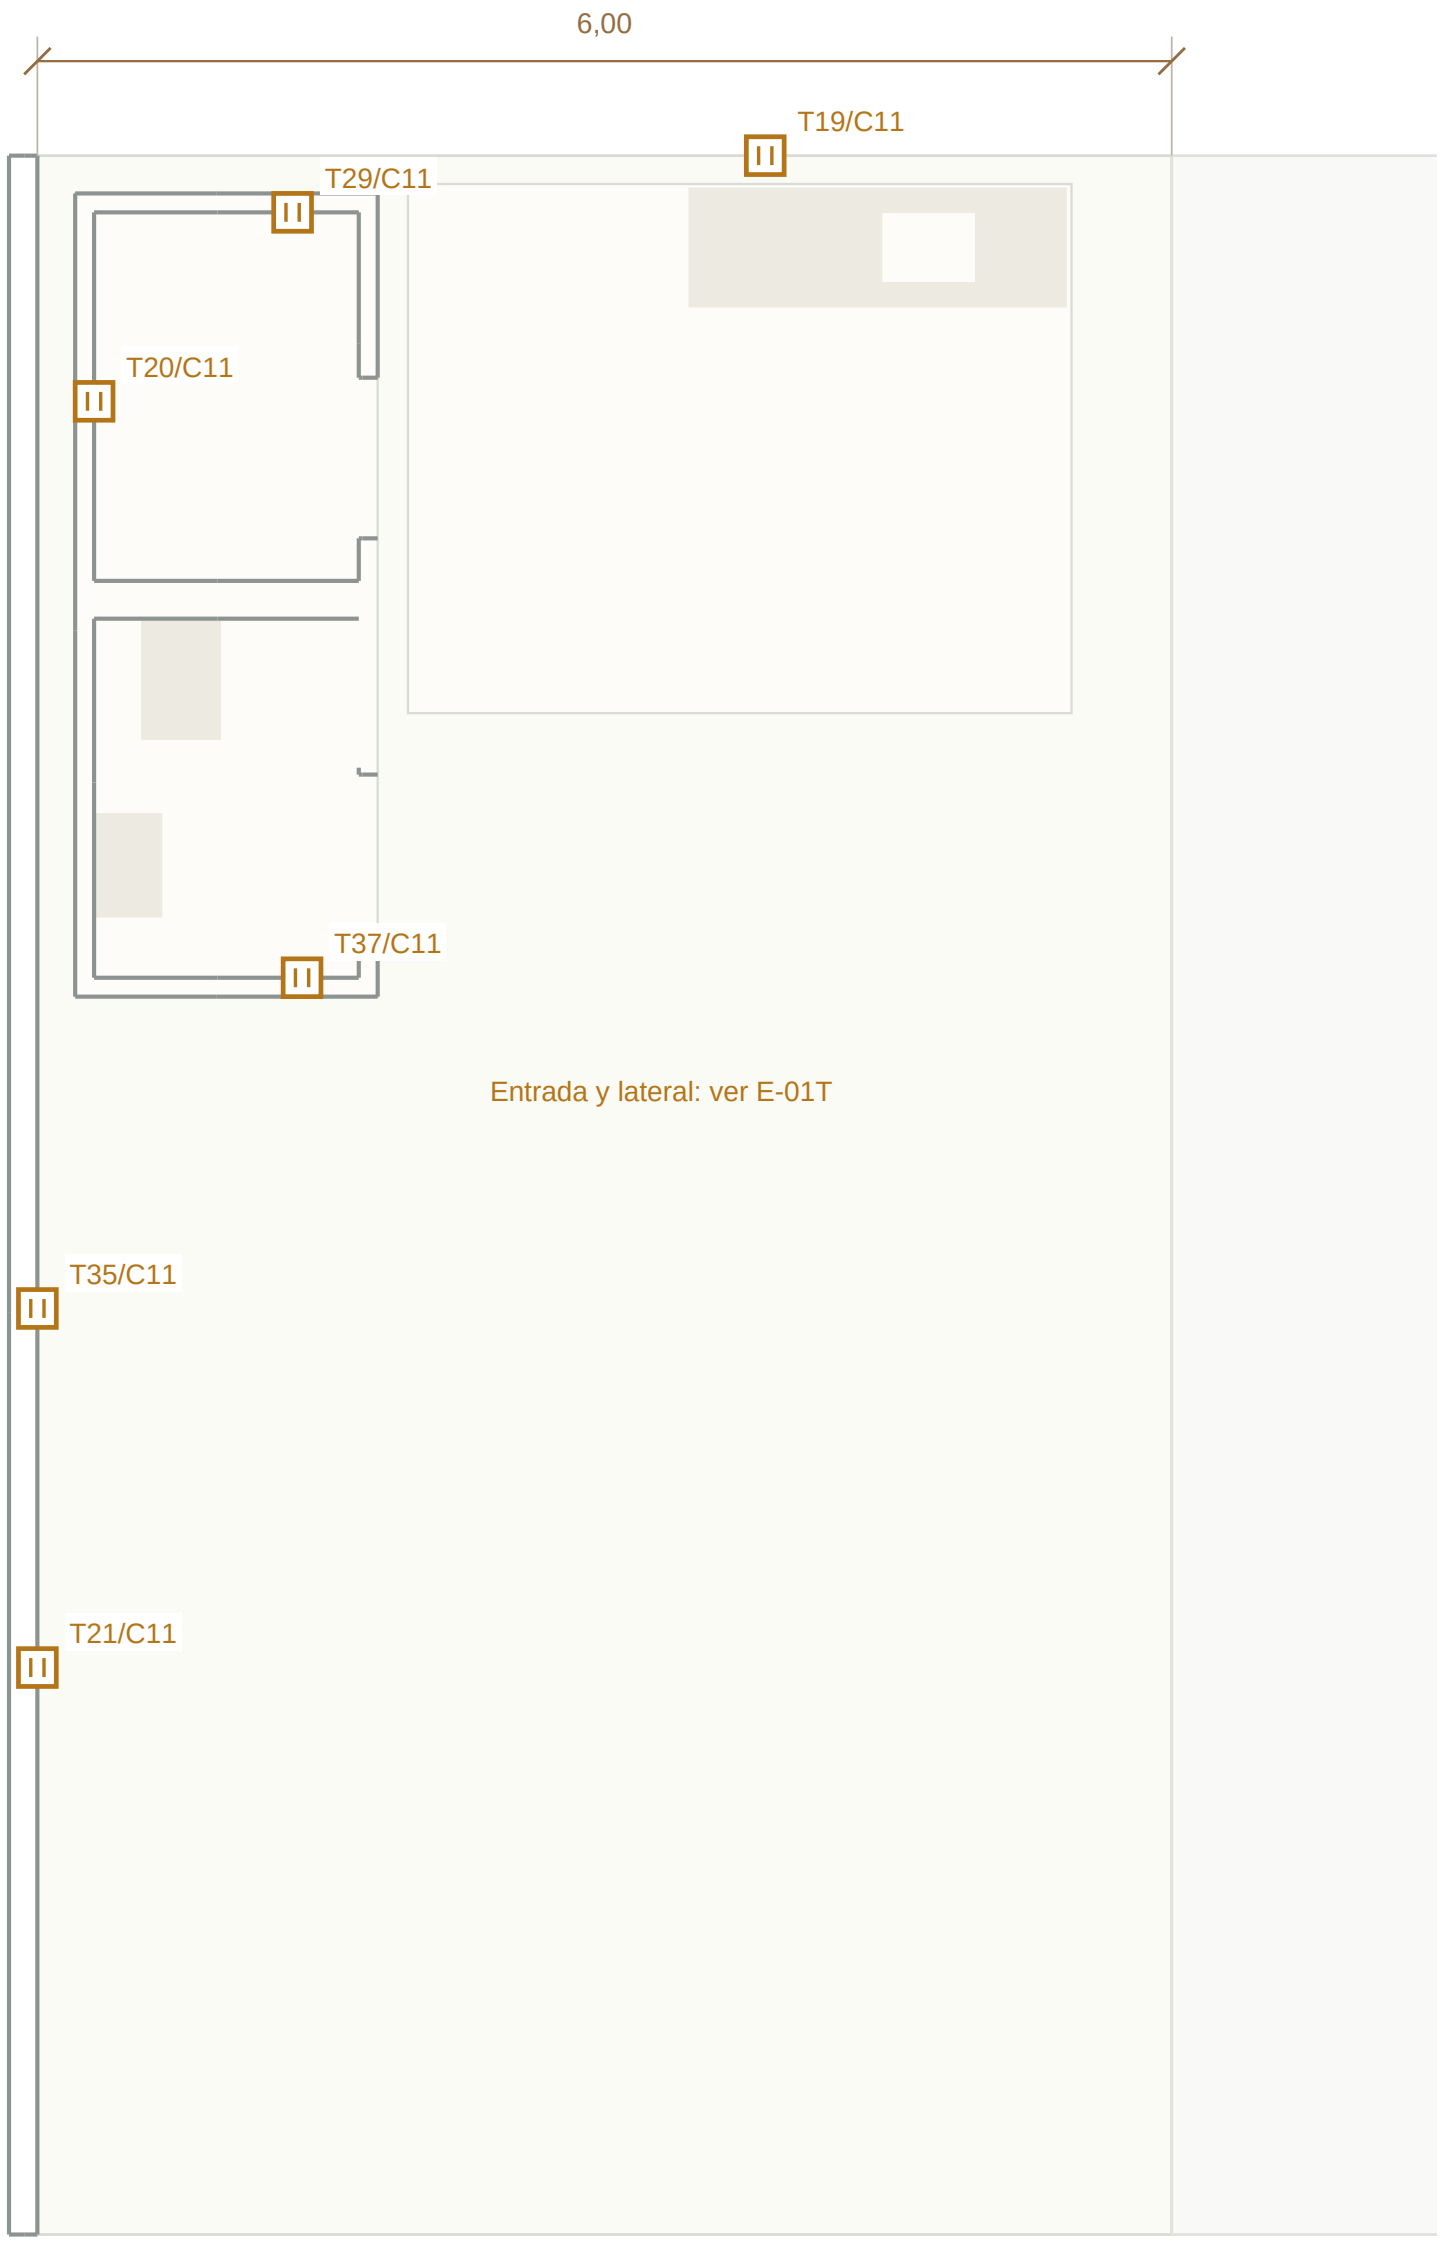

FRENTE ABAJO · RECORRIDOS PROPUESTOS

Simbología y notas en la hoja siguiente.

EXPLICACIÓN · E-03T

Tomacorrientes y equipos · Patio

Casa Lales · Revisión 12/11/2026 · 22dd2a9a

QUÉ SIGNIFICA CADA FIGURA



Cuadrado con dos rayas · T

Tomacorriente. Código T y grupo C coinciden con el visor 3D; no indican voltaje ni amperaje.

C01

C04-C11 · grupo funcional

El sufijo /C identifica un uso propuesto, sujeto al cálculo de cargas y protecciones.



Líneas grises · muro

Paredes del modelo como referencia para situar los puntos.



Figura beige · mueble o aparato

Huella de referencia; se conservan las posiciones del modelo.

DATOS Y CRITERIOS DEL PLANO

Tomacorrientes: 6 puntos

Códigos T conservados. /C identifica grupo funcional; no es voltaje ni capacidad.

Reservas de equipos: 0 cajas

No hay cajas EQ adicionales en este nivel.

Plano de luces y mandos: E-03L

Consultar su mapa independiente; no se representan aquí sus símbolos.

NOTAS PARA REVISIÓN EN OBRA

Mismas posiciones y códigos que en imágenes 3D; alturas propuestas. Cabezal sin instalaciones.


Dimensiones y capacidades de conductores, protecciones y puesta a tierra pendientes de cálculo.

Baños y exterior: posición, protección y equipo apropiado por validar.

E-03L · Iluminación y mandos · Patio

CASA LALES · MAPA COMPLETO · ESCALA 1:40 · IMPRIMIR AL 100 %

Revisión 12/11/2026 · 22dd2a9a

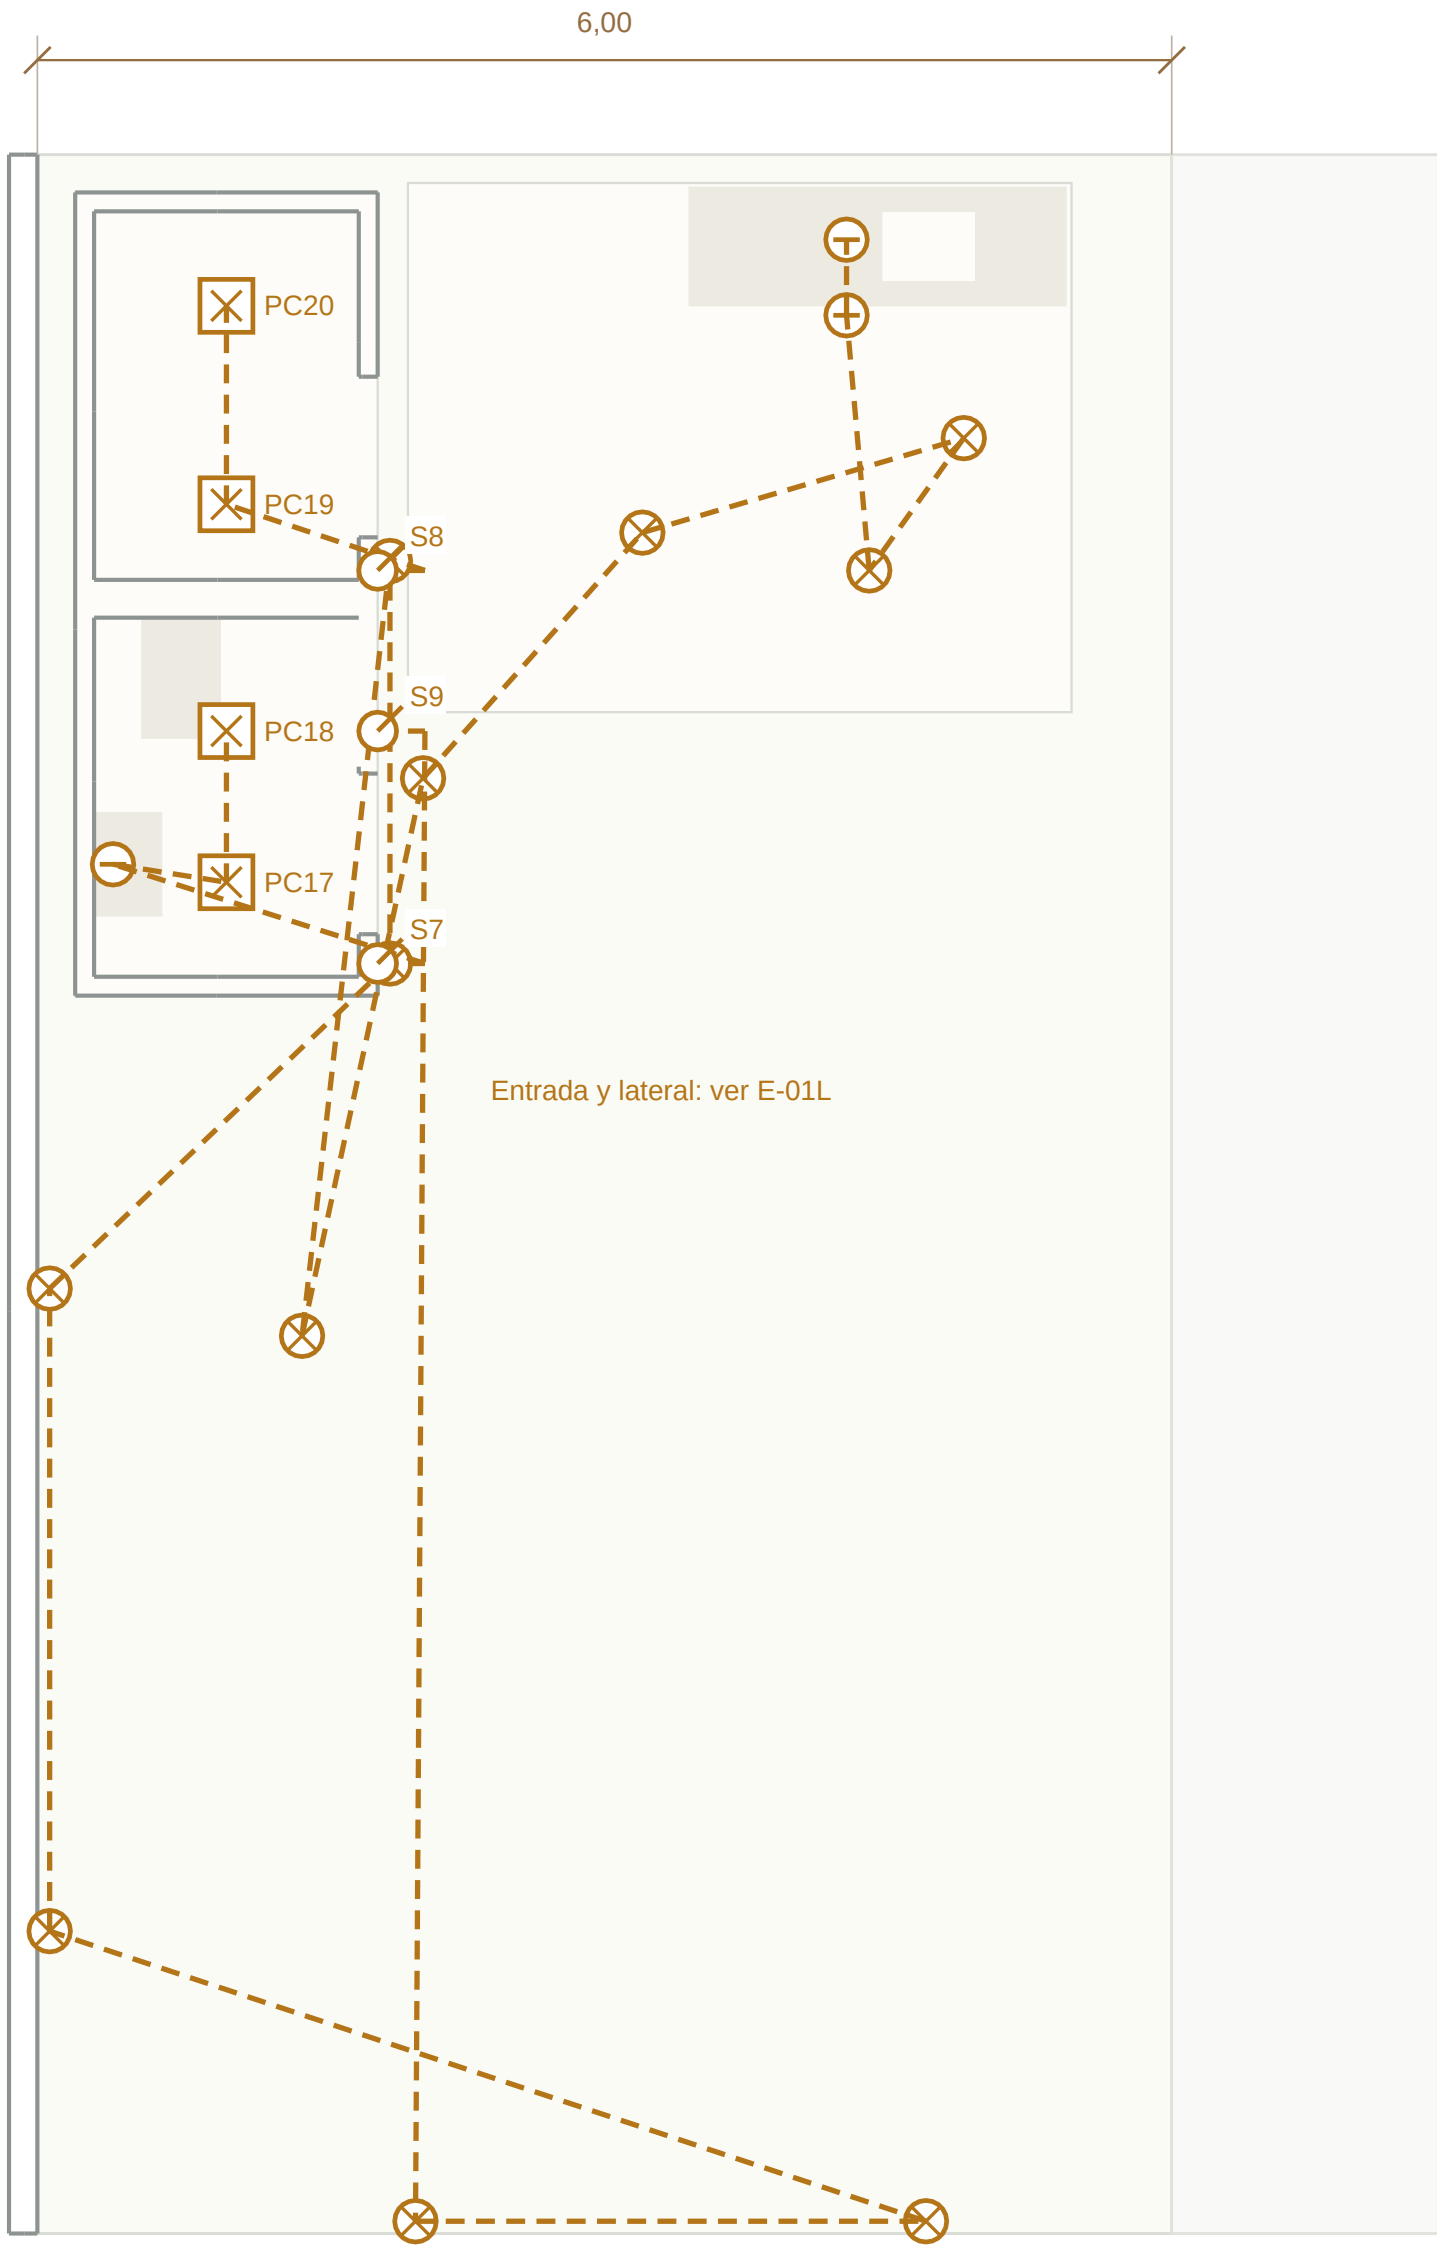

FRENTE ABAJO · RECORRIDOS PROPUESTOS

Simbología y notas en la hoja siguiente.

EXPLICACIÓN · E-03L

Iluminación y mandos · Patio

Casa Lales · Revisión 12/11/2026 · 22dd2a9a

QUÉ SIGNIFICA CADA FIGURA

Cuadrado con X · plafón PC
Lámpara cuadrada de sobreponer. Cada código PC identifica una unidad; potencia y temperatura en el cuadro de esta hoja.

Círculo con X · luz general
Punto de iluminación general del modelo. No equivale siempre a una unidad comercial.

Círculo con raya · luz de apoyo
Referencia de trabajo o ambiente: LED, espejo, mueble, aplique o escalón.

Círculo con trazo · S
Interruptor o caja de teclas. Misma posición y código que el visor; S4/S5 coordinan las gradas.

Línea punteada · relación de mando
Relaciona el mando con sus luces. No fija un cableado, conductores ni trayecto de ejecución.

Líneas grises · muro
Paredes del modelo como referencia para situar los puntos.

Figura beige · mueble o aparato
Huella de referencia; se conservan las posiciones del modelo.

DATOS Y CRITERIOS DEL PLANO

Iluminación general: 4 plafones PC / 11 otros
Cuadrado con X: plafón PC; círculo con X: otra luz general.

Luz de trabajo / ambiente: 3 referencias
Círculo con raya; incluye LED, apliques y apoyos.

Cajas de mandos: S7, S8, S9
S4/S5: coordinar el control de gradas desde ambos niveles.

Plano de tomacorrientes: E-03T
Consultar su mapa independiente; no se representan aquí sus símbolos.

Baño del patio: 2 × 12 W · 4000 K
Sellado para zona húmeda; por confirmar

Bodega: 2 × 12 W · 4000 K
Interior seco

NOTAS PARA REVISIÓN EN OBRA

Mismas tomas y mandos que en imágenes 3D. Alturas propuestas; dormitorio según distribución aplicada.

Líneas punteadas: relación de mando y recorrido conceptual; no son número de conductores.

Grupos C01-C12 funcionales: dividir por planta, cargas y protecciones en cálculo. Tablero y tierra pendientes.

Bajo Eternit: canalización y cajas fijadas a soporte definido, nunca a las planchas.

Las luces de gradas se asignan a PB o PA por cota: cada referencia aparece una sola vez.

PC: plafón cuadrado sobrepuesto. Modelo seco de referencia 28,5 × 28,5 × 2,8 cm, 24 W, 1800 lm, 0,583 kg; 100–240 V. Confirmar equipo y suministro.

Fijar herraje a perfil/refuerzo del cielo; no cargar sólo la placa. Revisar perfilería, anclaje y acceso al driver; no suspender del Eternit.


Baños: variante sellada IP44 mínimo; IP65 si la zona lo exige. Potencia y formato menores orientativos; modelo y protección por elegir.

Plafón de referencia sin dimmer. LED indirecto y tarea separados. Cantidad propuesta; verificar iluminación con fotometría y medidas reales.

H-01 · Agua fría y caliente · PB y patio

CASA LALES · MAPA COMPLETO · ESCALA 1:60 · IMPRIMIR AL 100 %

Revisión 12/11/2026 · 22dd2a9a

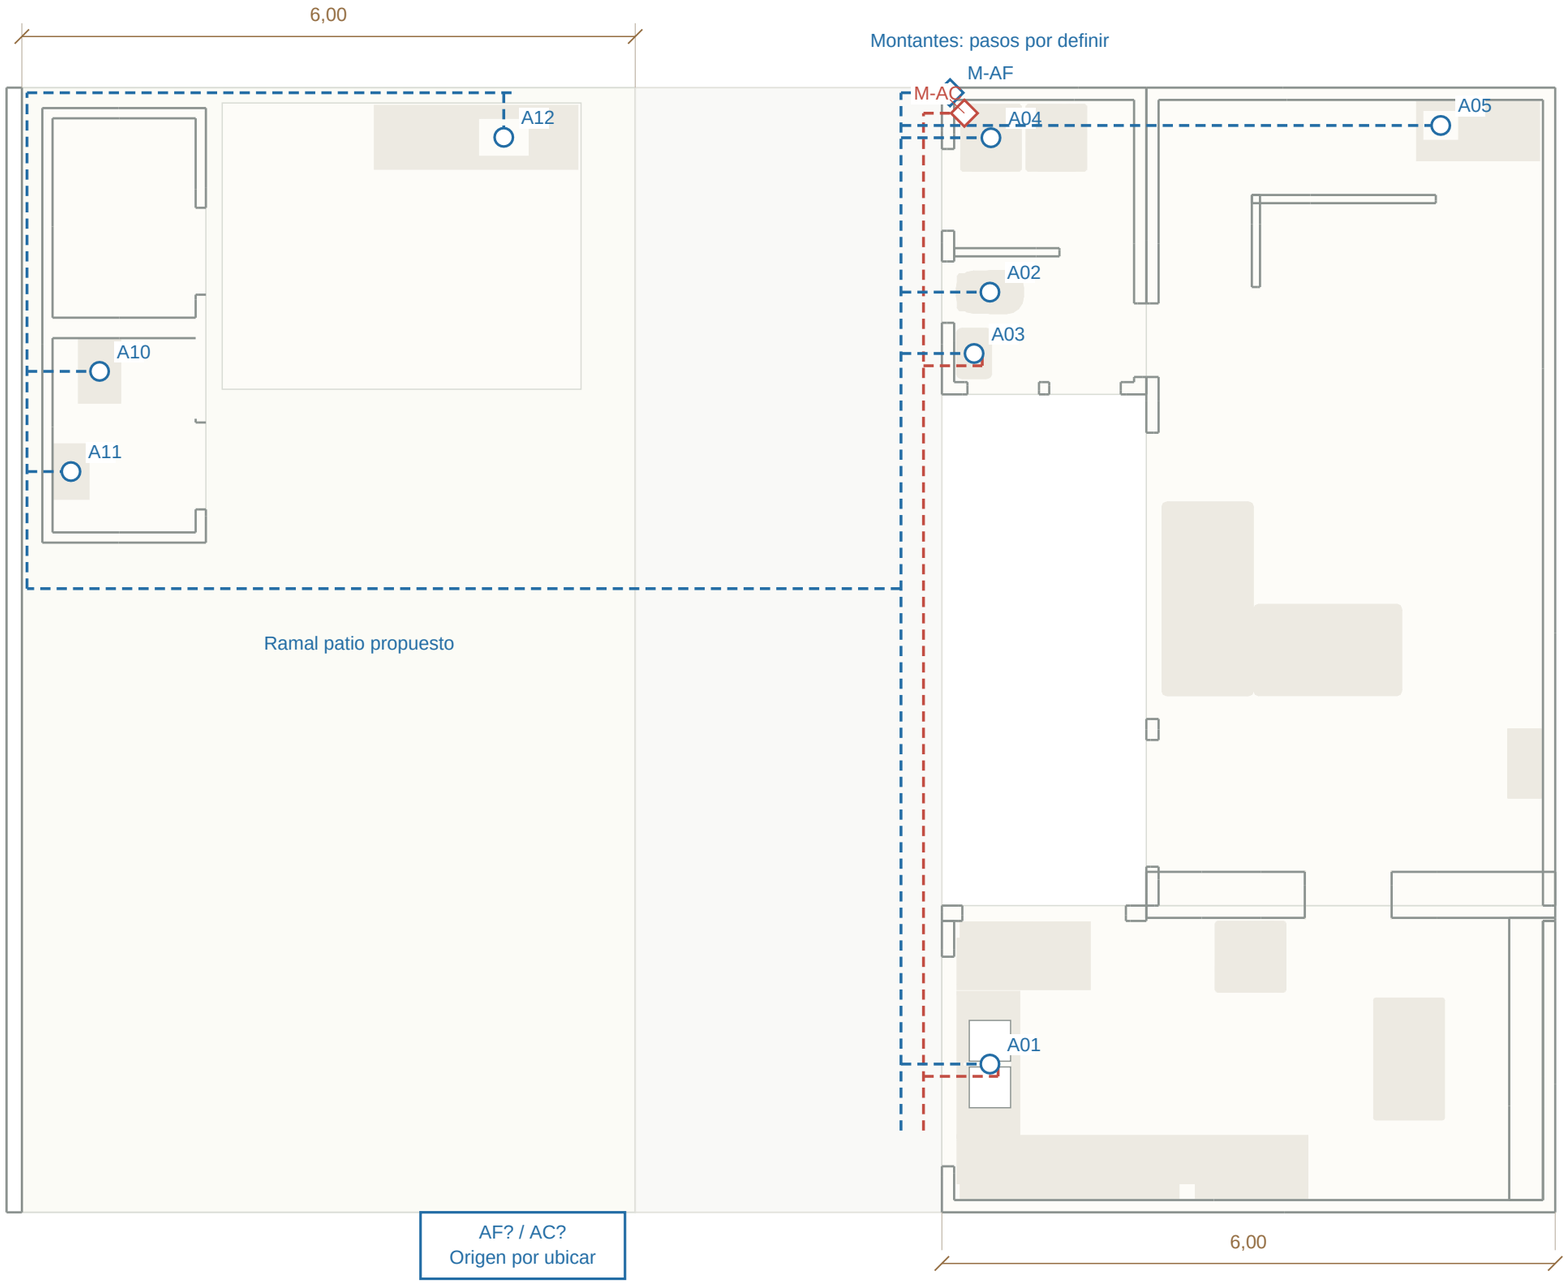


FRENTE ABAJO · RECORRIDOS PROPUESTOS

H-02 · Agua fría y caliente · planta alta

CASA LALES · MAPA COMPLETO · ESCALA 1:40 · IMPRIMIR AL 100 %

Revisión 12/11/2026 · 22dd2a9a

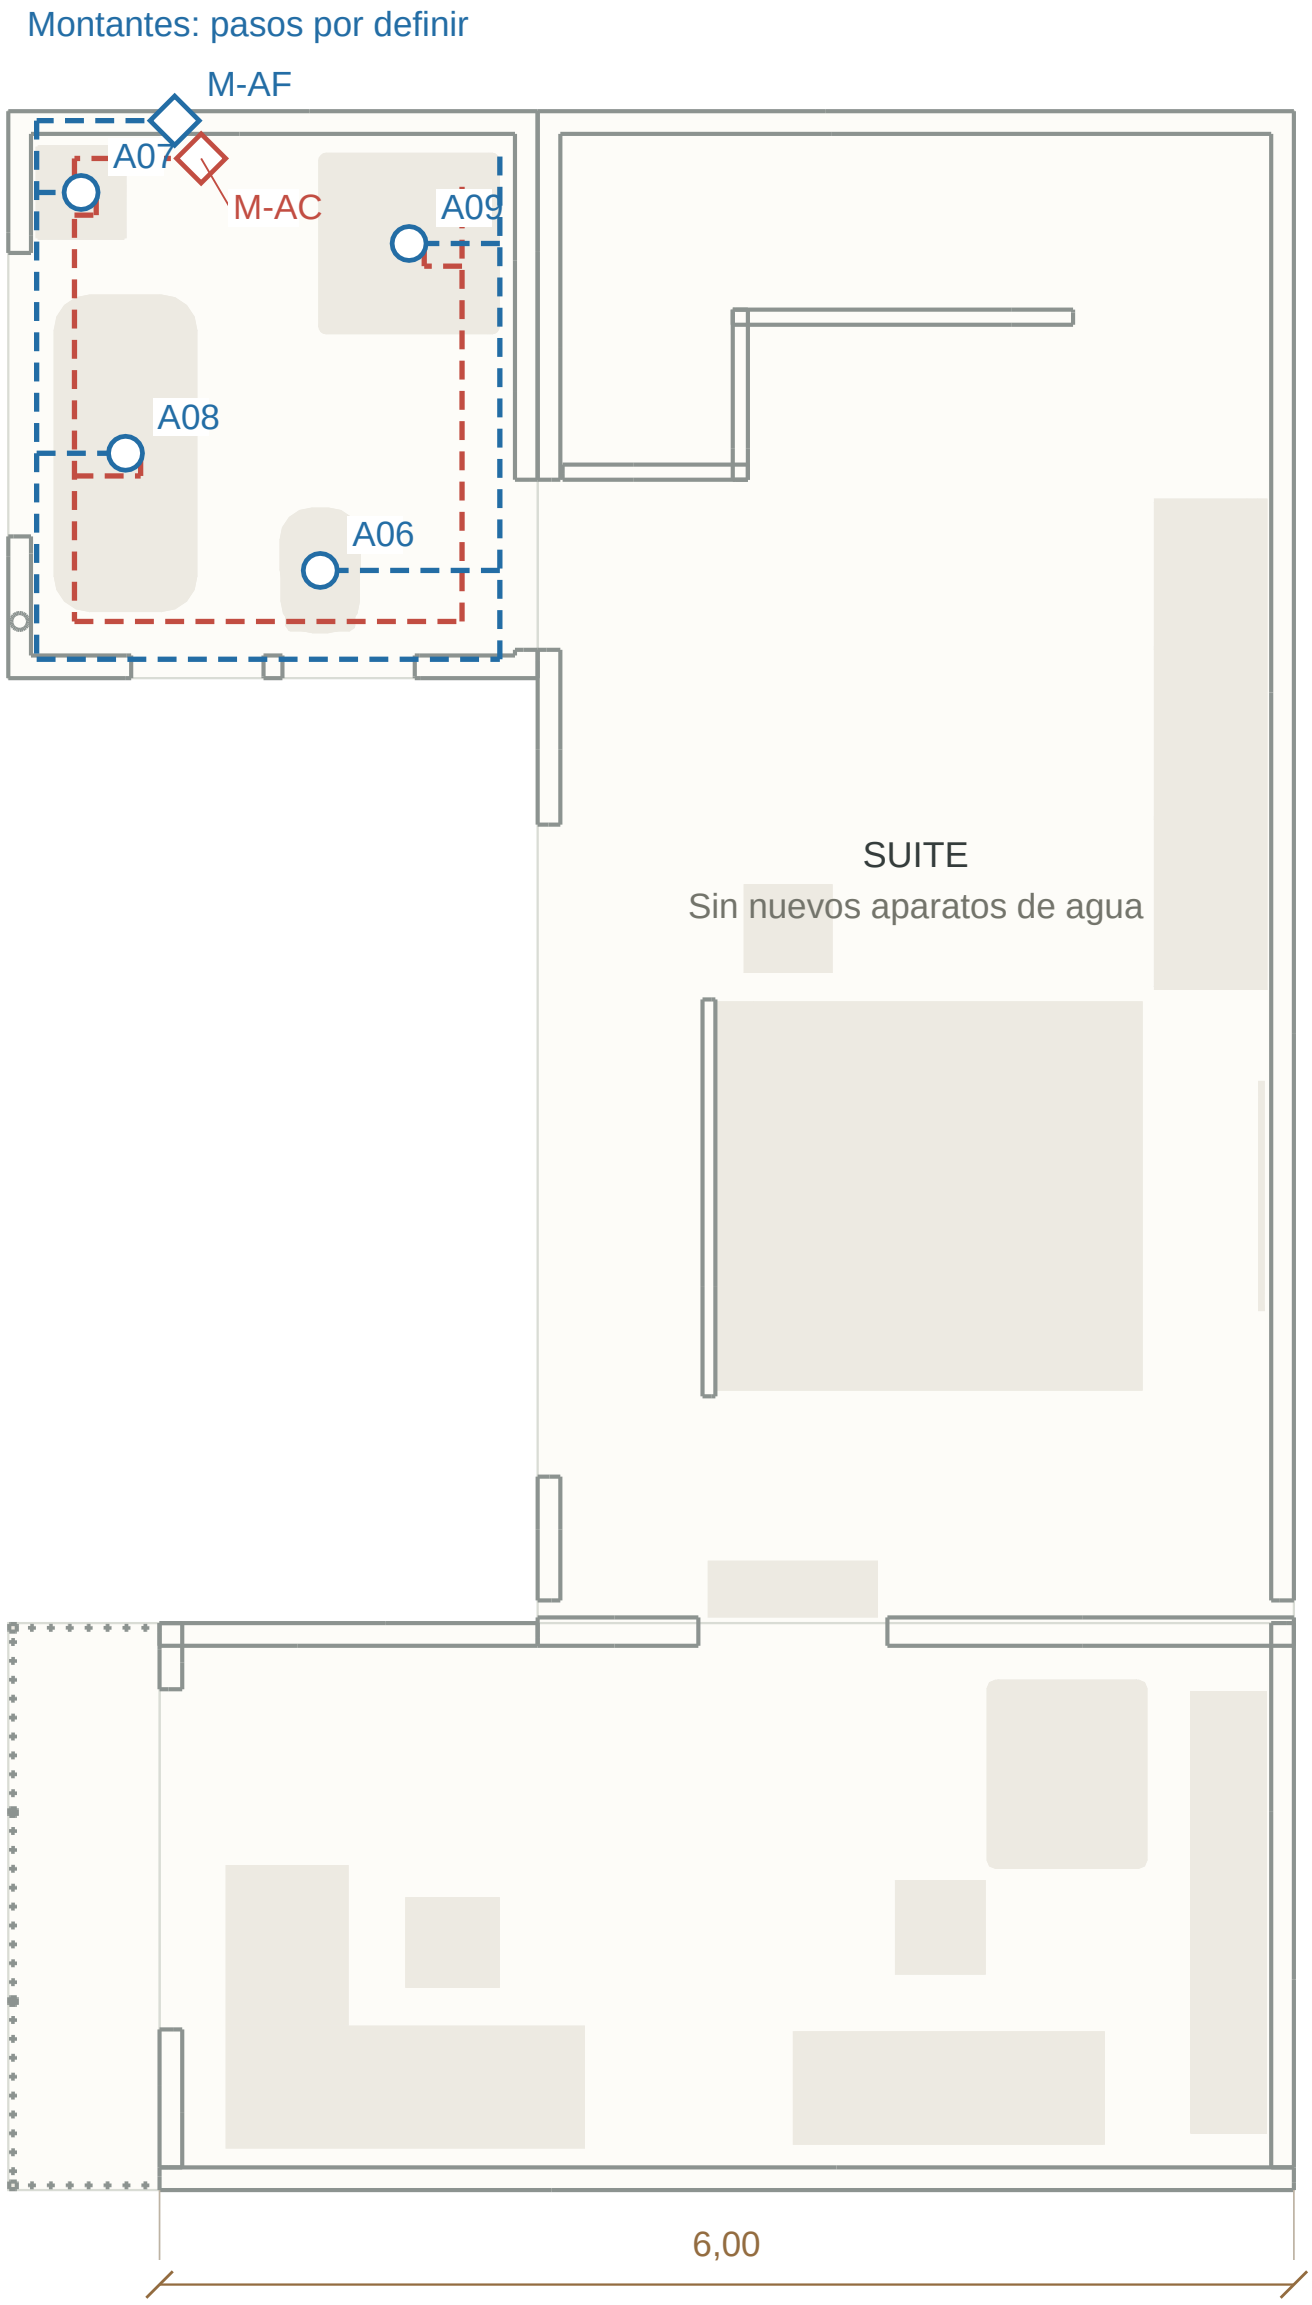


FRENTE ABAJO · RECORRIDOS PROPUESTOS

S-01 · Desagües y ventilación · PB y patio

CASA LALES · MAPA COMPLETO · ESCALA 1:60 · IMPRIMIR AL 100 %

Revisión 12/11/2026 · 22dd2a9a

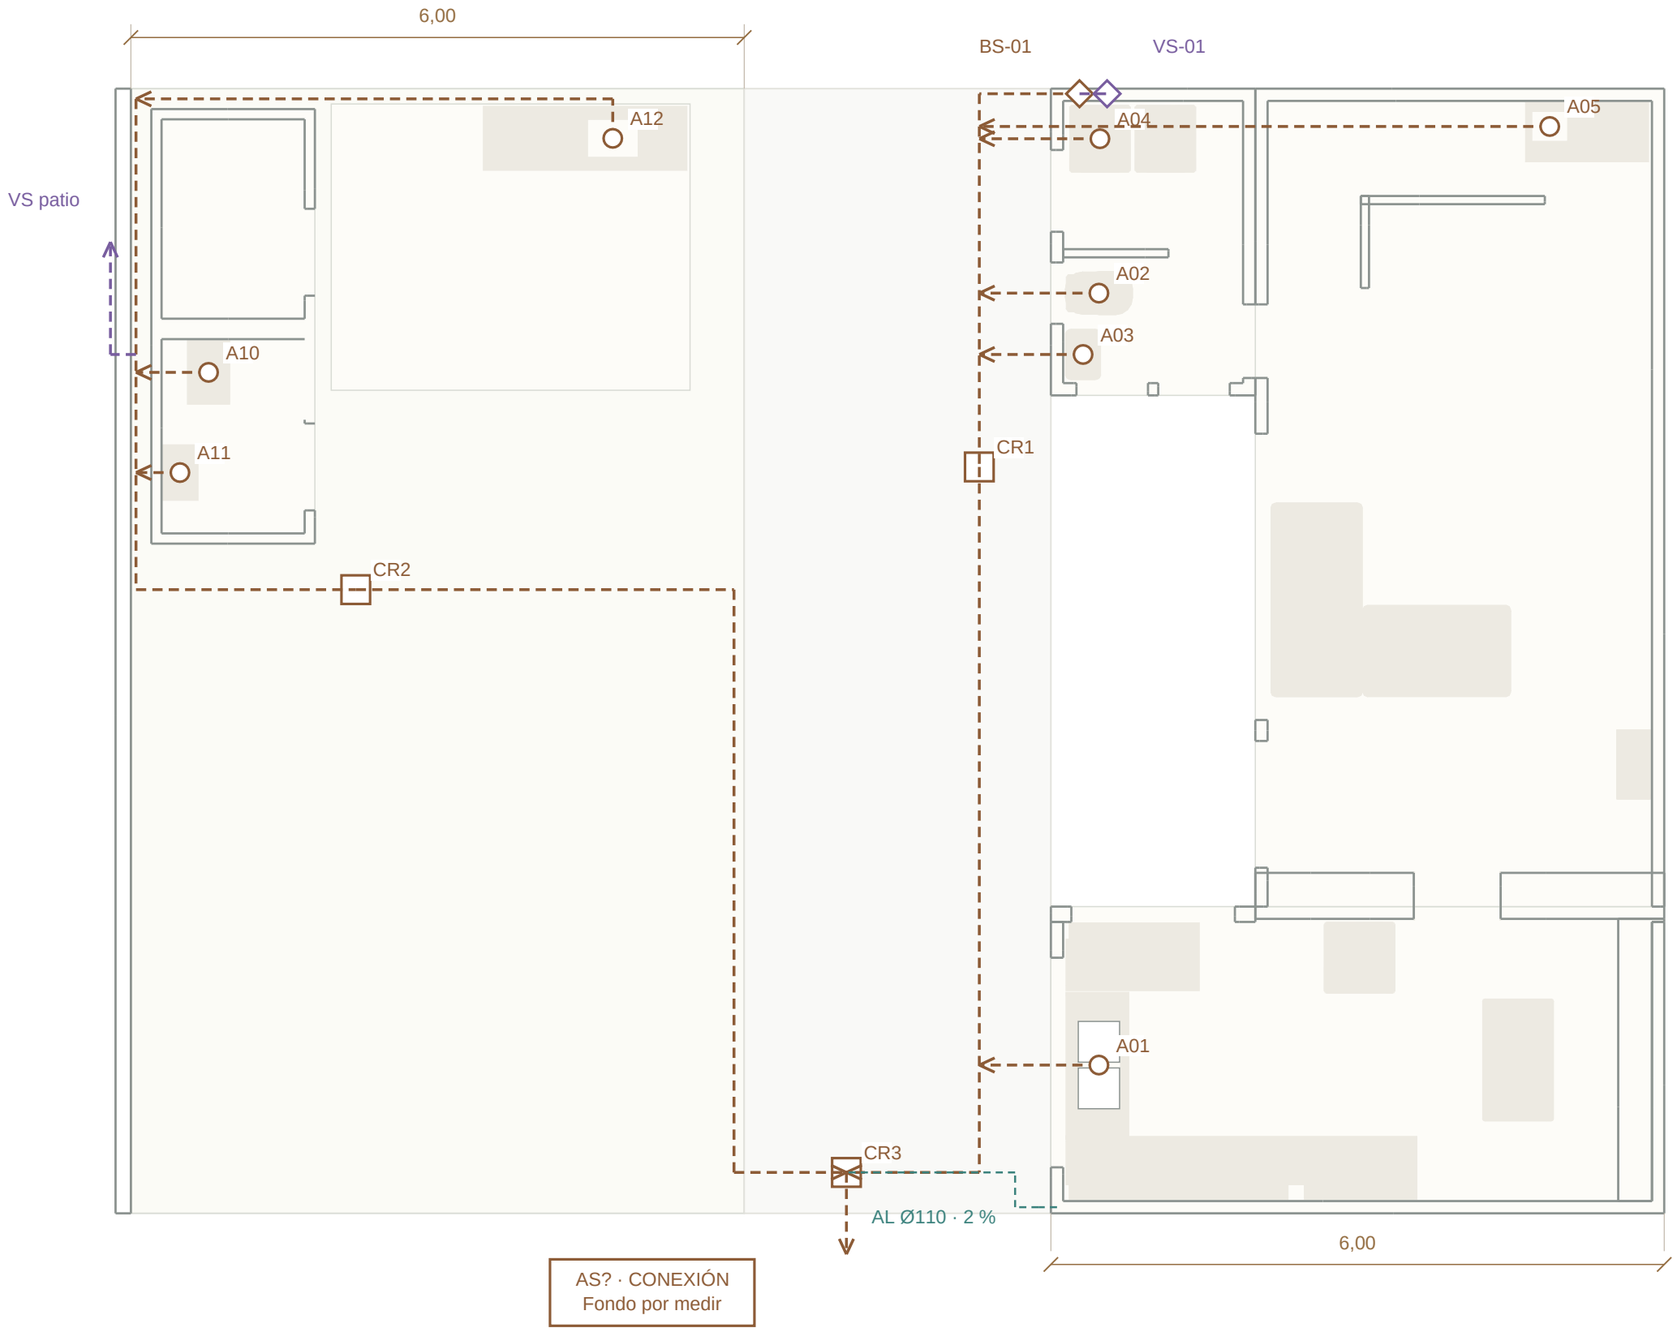


FRENTE ABAJO · RECORRIDOS PROPUESTOS

S-02 · Desagües y ventilación · planta alta

CASA LALES · MAPA COMPLETO · ESCALA 1:40 · IMPRIMIR AL 100 %

Revisión 12/11/2026 · 22dd2a9a

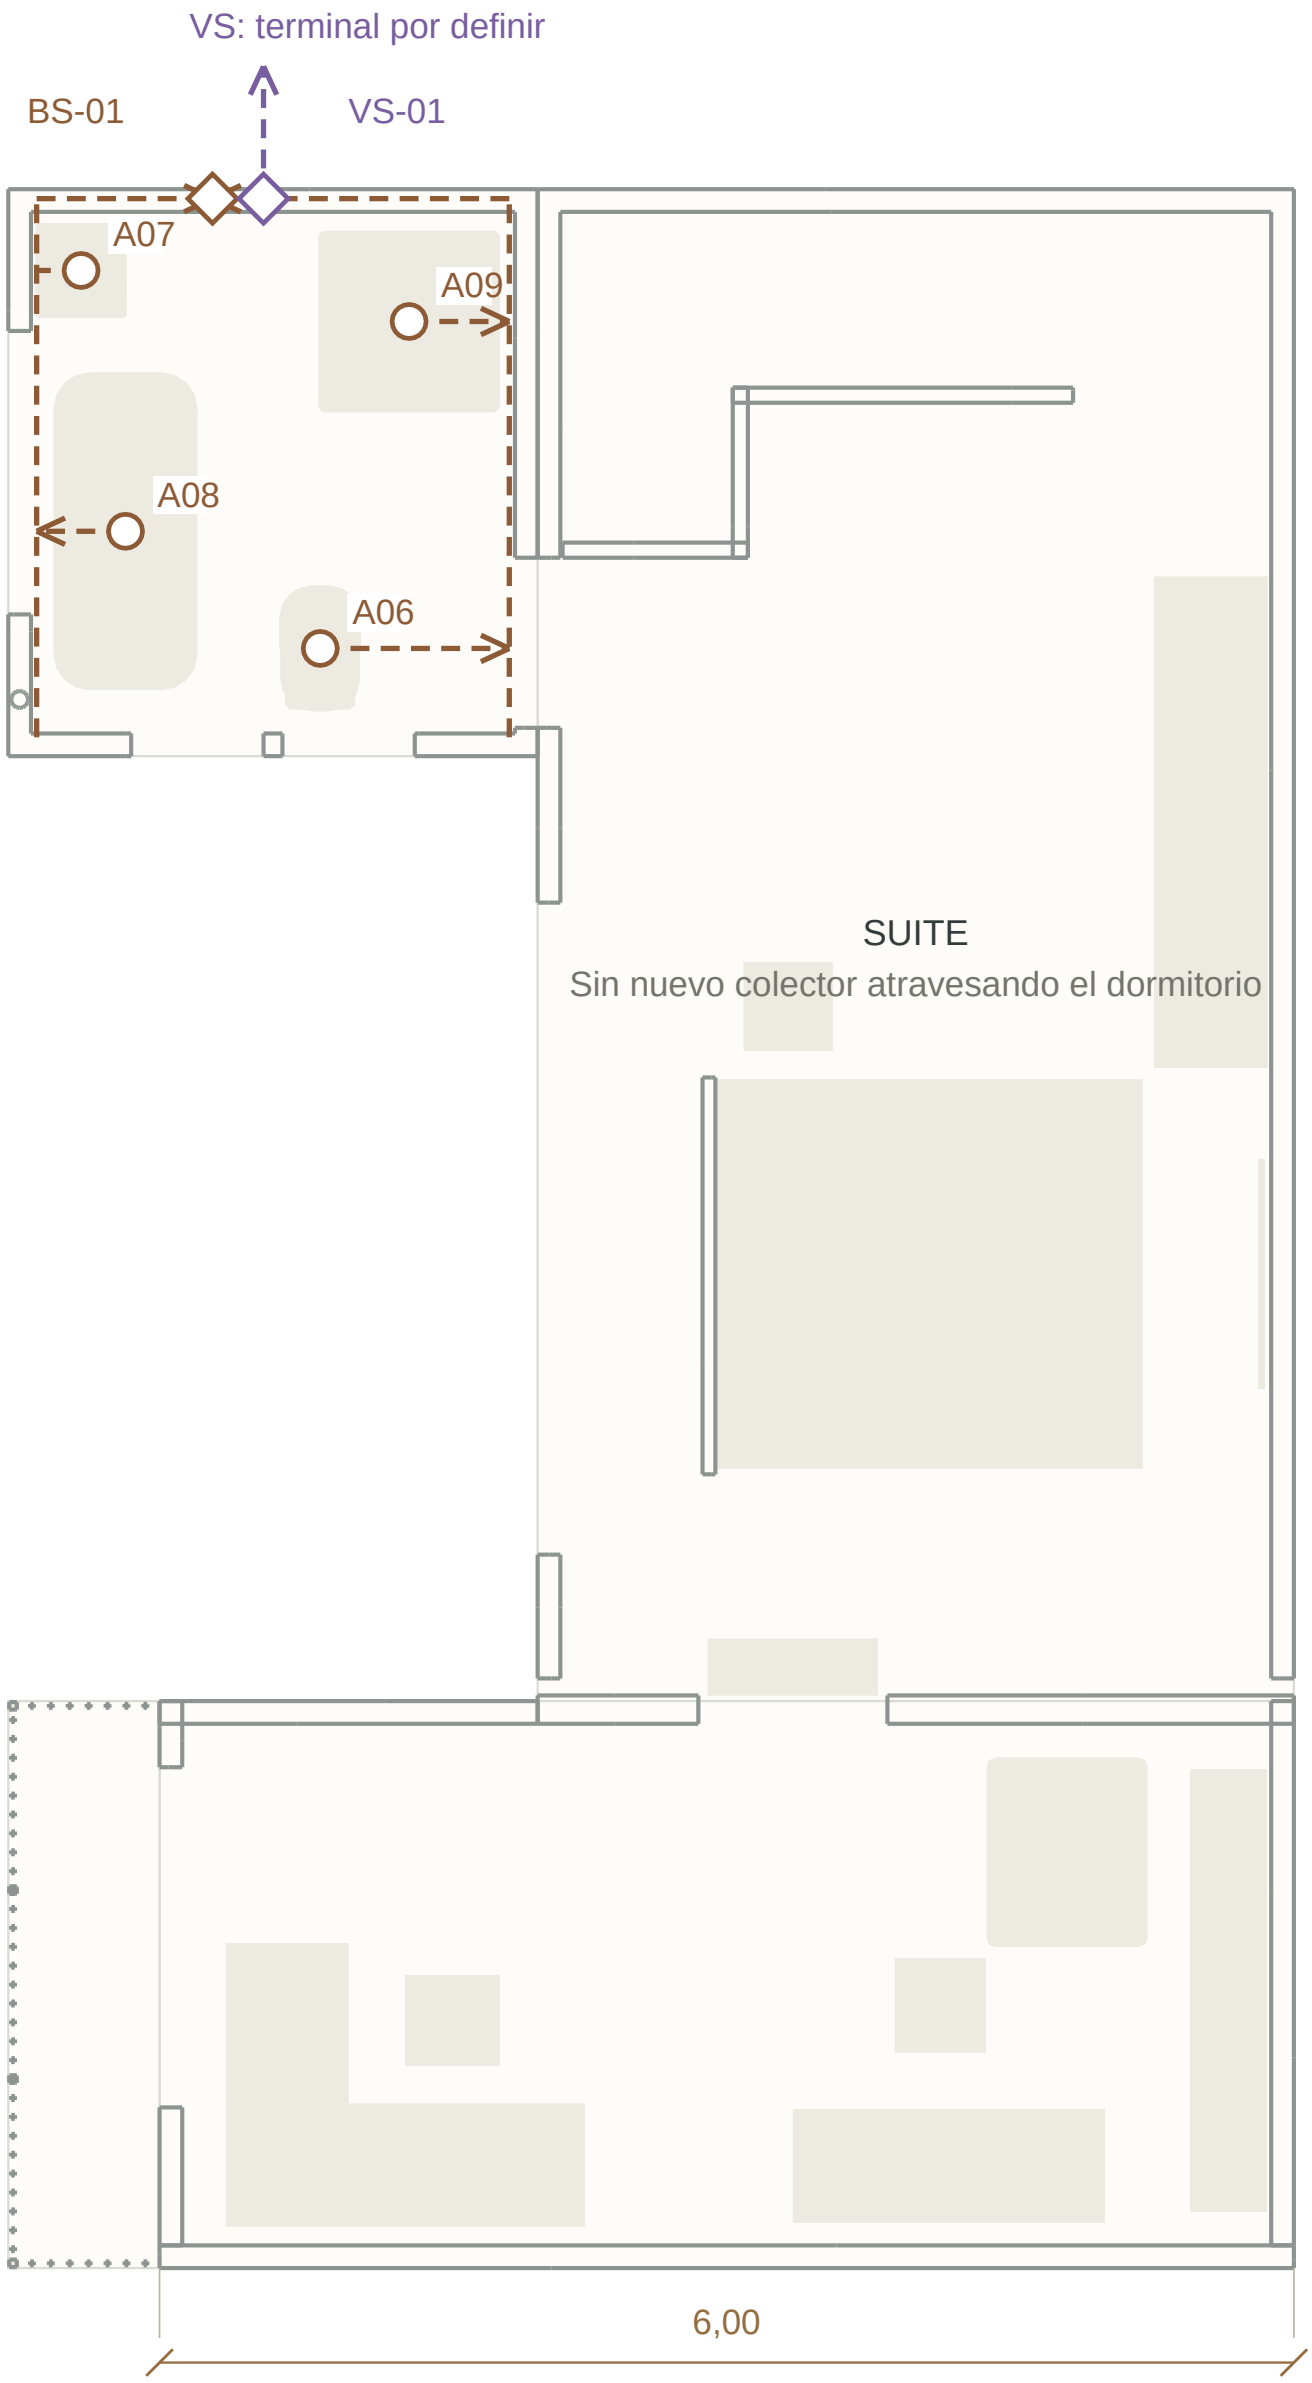

FRENTE ABAJO · RECORRIDOS PROPUESTOS

A-07 · Medidas y alturas confirmadas por el usuario

CASA LALES · MAPA COMPLETO · ESCALA 1:40 · IMPRIMIR AL 100 %


Revisión 12/11/2026 · 22dd2a9a

ESPACIO	MEDIDAS m	ÁREA m²	ALTURA m
Sala, bloque completo	4,00 × 8,00	32,00	2,10
Cocina y comedor	6,00 × 3,00	18,00	2,20
Baño social con lavandería	2,00 × 3,00	6,00	2,10
Dormitorio, bloque completo	4,00 × 8,00	32,00	2,10
Baño principal	2,80 × 3,00	8,40	2,20
Estudio sobre cocina	6,00 × 3,00	18,00	2,20
Balcón del estudio	0,80 × 3,00	2,40	Pretil 1,10
Baño del patio, interior libre	1,40 × 1,90	2,66	3,50 - 3,58
Bodega del patio, interior libre	1,40 × 1,95	2,73	3,50 - 3,60
Área del asadero	3,51 × 2,80	9,83	3,33 - 3,51
Patio completo	6,00 × 11,00	66,00	Abierto

A-09 · Baño principal · Losa propuesta y encuentro de alturas

CASA LALES · MAPA COMPLETO · ESCALA 1:25 · IMPRIMIR AL 100 %

Revisión 12/11/2026 · 22dd2a9a

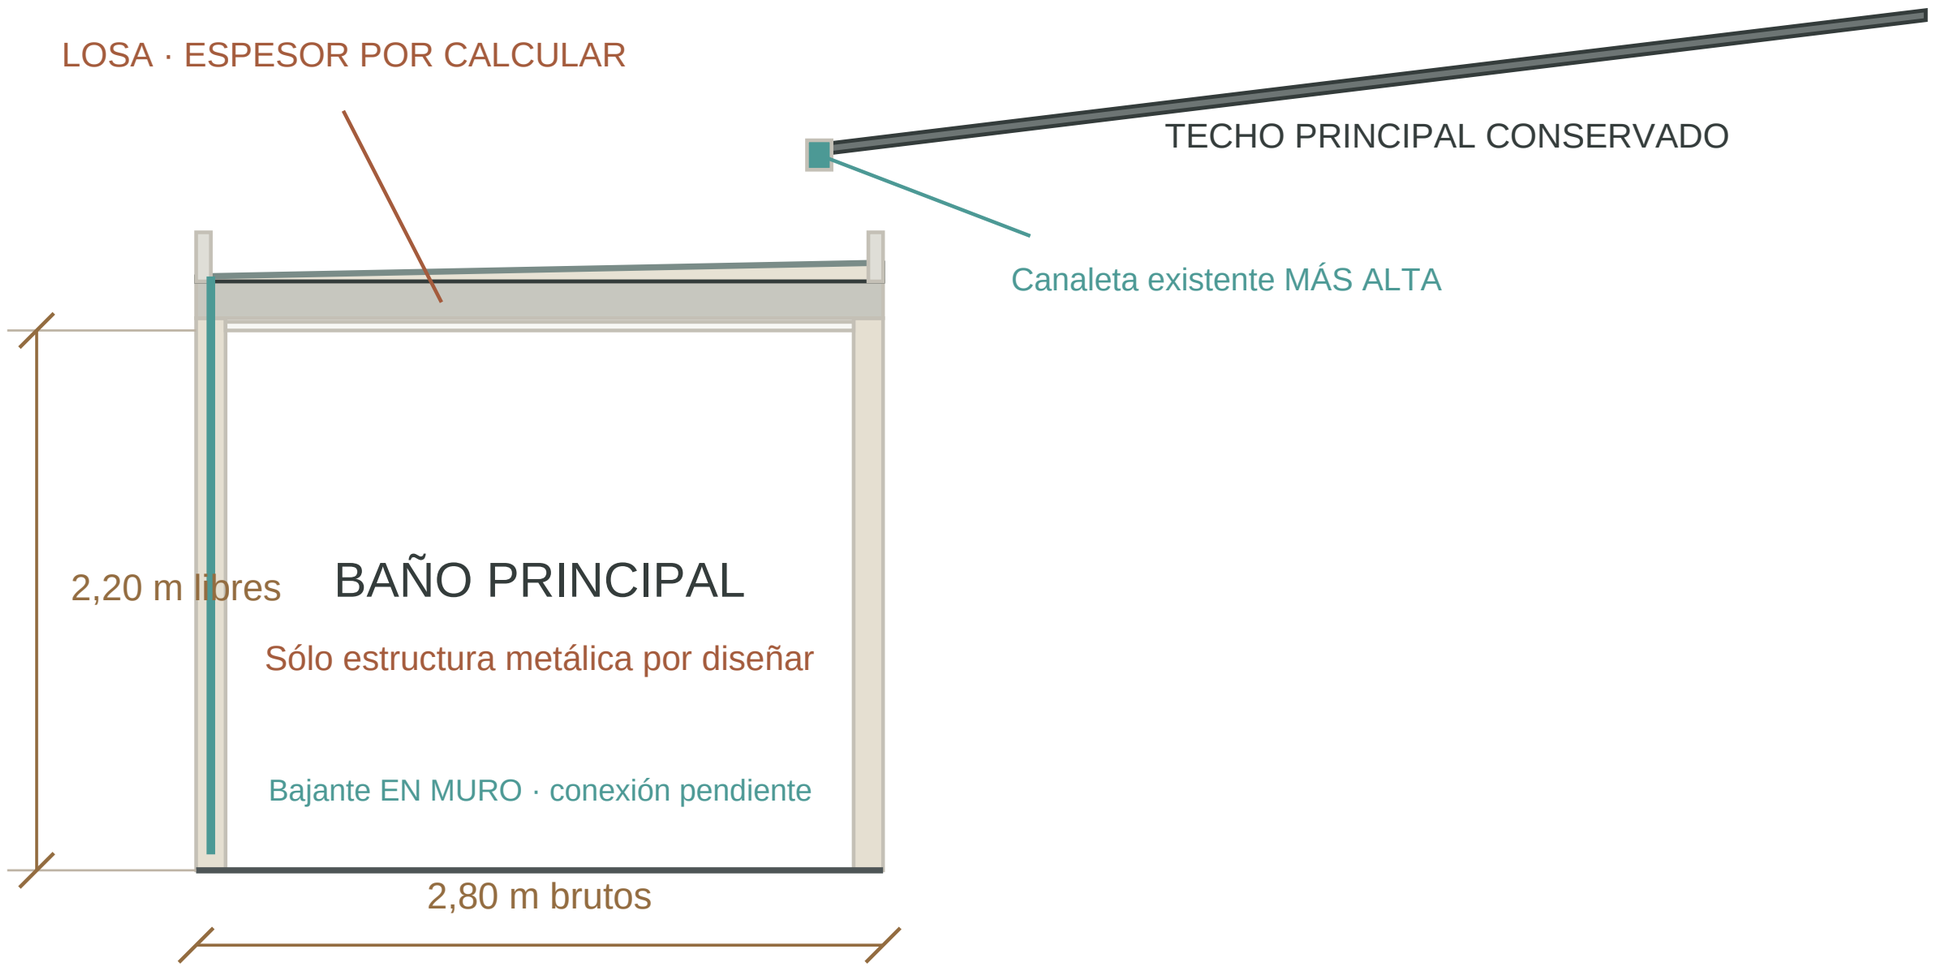

Revisión 12/11/2026 · 22dd2a9a | Modelo y propuesta de coordinación - comprobar en sitio

HUECOS, PUERTAS Y PASOS - MEDIDAS DEL MODELO

IDENTIFICACIÓN	NIVEL	ANCHO m	ALTO m	COTA INFERIOR m
Acceso al baño principal	PA	0,90	2,10	2,30
Entrada · 1,10 libre / hoja 1,15 x 2,10	PB	1,24	2,15	0,00
Sala · ventanal hacia el patio	PB	2,80	1,20	0,65
Social · frente, lado izquierdo	PB	0,70	0,60	1,22
Social · frente, lado derecho	PB	0,70	0,60	1,22
Principal · frente, lado izquierdo	PA	0,70	0,60	3,56
Principal · frente, lado derecho	PA	0,70	0,60	3,56
Principal · ventana hacia calle	PA	1,50	0,75	3,44
Dormitorio · ventanal hacia patio	PA	3,45	1,40	3,00
Cocina · ventana hacia calle	PB	2,05	0,85	1,10
Cocina · ventana de retorno	PB	1,60	0,85	1,10
Baño social (hoja 0,70 x 1,95)	PB	0,72	1,98	0,00
Acceso al estudio · Dos subidas rectas17,5cm	PA	1,00	2,20	2,65
Paso cocina sin hoja · luz útil	PB	0,826	1,935	0,00
Estudio · corredera al balcón	PA	1,80	2,10	2,65
Baño social · ventana a calle	PB	0,60	0,75	1,10
Lavandería · ventana a calle	PB	0,80	0,75	1,10
Puerta baño patio (hoja 0,80 x 1,98)	Patio	0,85	2,05	-0,23
Puerta bodega (hoja 0,80 x 1,98)	Patio	0,85	2,05	-0,23
Ventana bodega	Patio	0,80	0,20	1,85
Ventana baño patio	Patio	0,75	0,60	Por medir

Cotas inferiores referidas al origen común del modelo. En PA no equivalen a antepecho desde su piso.