
Revisión 10/11/2026 · 3cde0d4d | Modelo y propuesta de coordinación - comprobar en sitio

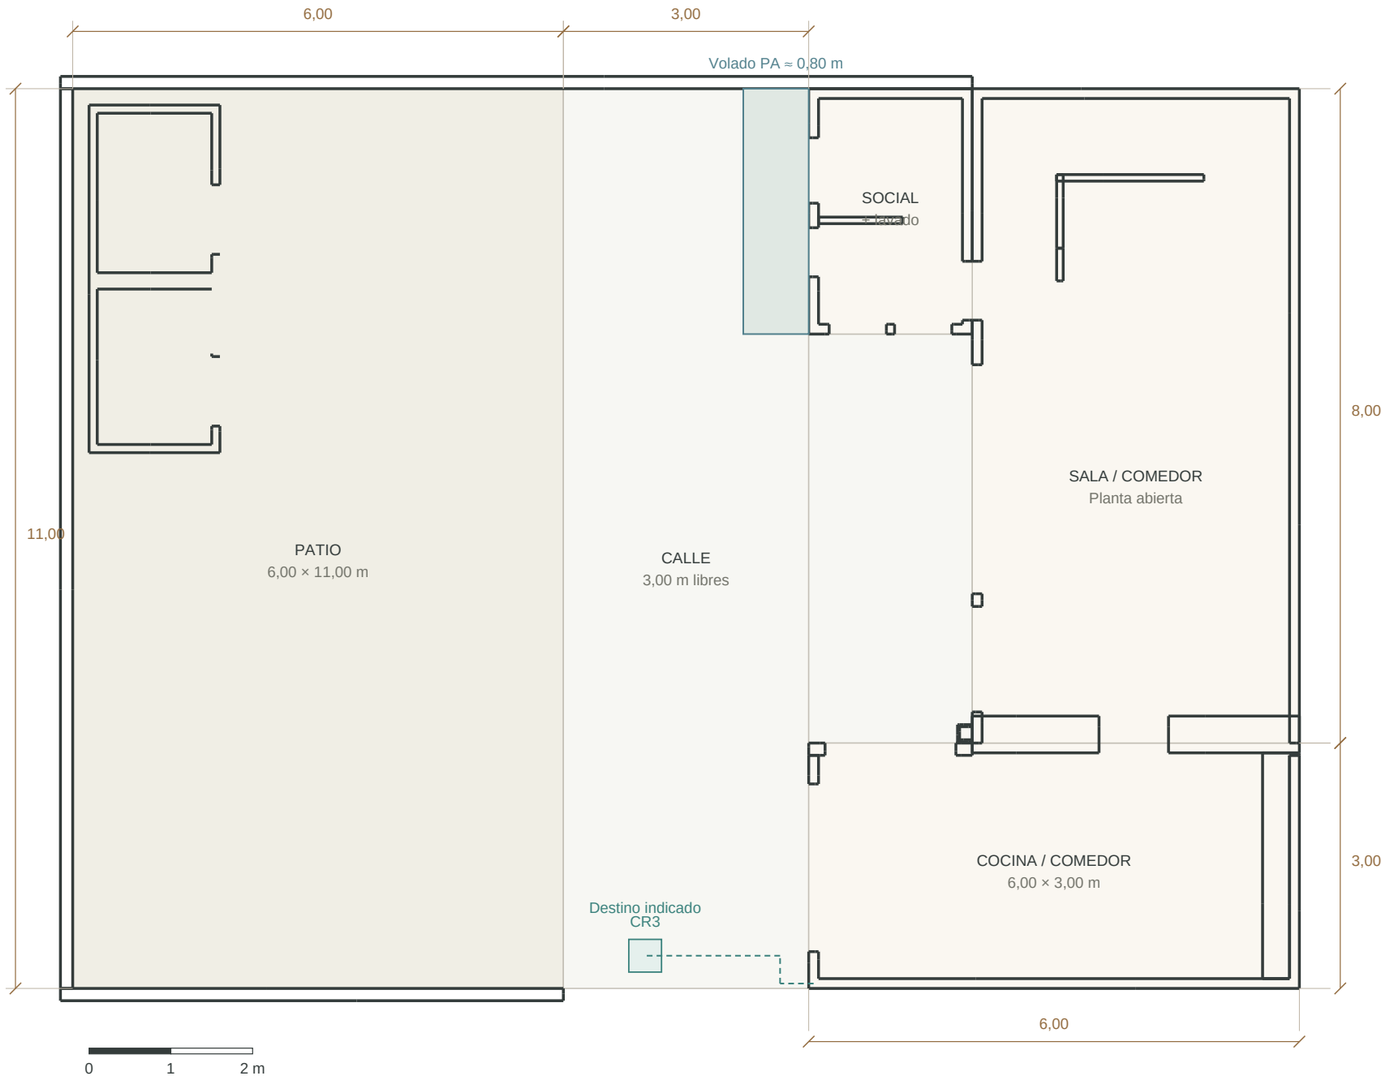

FRENTE / LLEGADA DESDE LA CALLE

ESCALA 1:75 / A3 AL 100 %

No ajustar a página. Comprobar escala gráfica.

Patio
6,00 × 11,00 m
Modelo · verificar en sitio

Calle de acceso
3,00 m de ancho
Confirmado por el usuario; comprobar replanteo.

Cocina / comedor
6,00 × 3,00 m
Modelo · verificar en sitio

Cuerpo de dos pisos
4,00 × 8,00 m
Modelo · verificar en sitio

Baño social / lavado
2,00 × 3,00 m
Modelo · verificar en sitio

Baño principal PA
2,80 × 3,00 m
Modelo · verificar en sitio

NOTAS PARA REPLANTEO

Adobe 45 cm: paso cocina/sala y lateral del comedor. Retorno de bloque 15 cm; contorno exterior conservado.

Baño social: hoja 70 cm; lavabo 50 × 35 cm. Lavandería al fondo, pantalla de gypsum de 1,80 m y paso lateral 73 cm.


Gradas pegadas a baño y fondo: 3 rectas, 3 compensadas y 6 rectas. Subidas 17,69 cm; rectas de 30 cm. Puerta social adelantada 35 cm. Gypsum hasta el techo; puerta social hacia dentro del baño.

Paso cocina: luz útil aproximada 0,826 × 1,935 m; vano existente conservado. Replantear jambas y dintel.

PA: estudio sobre cocina y balcón lateral de 0,80 m; sin pilares nuevos dibujados en el paso de 3 m. Estructura y gálibo reales por verificar.

Piso flotante en sala, estudio y dormitorio. Cocina, baños y asadero conservan porcelanato beige.

Revisión 10/11/2026 · 3cde0d4d | Modelo y propuesta de coordinación - comprobar en sitio

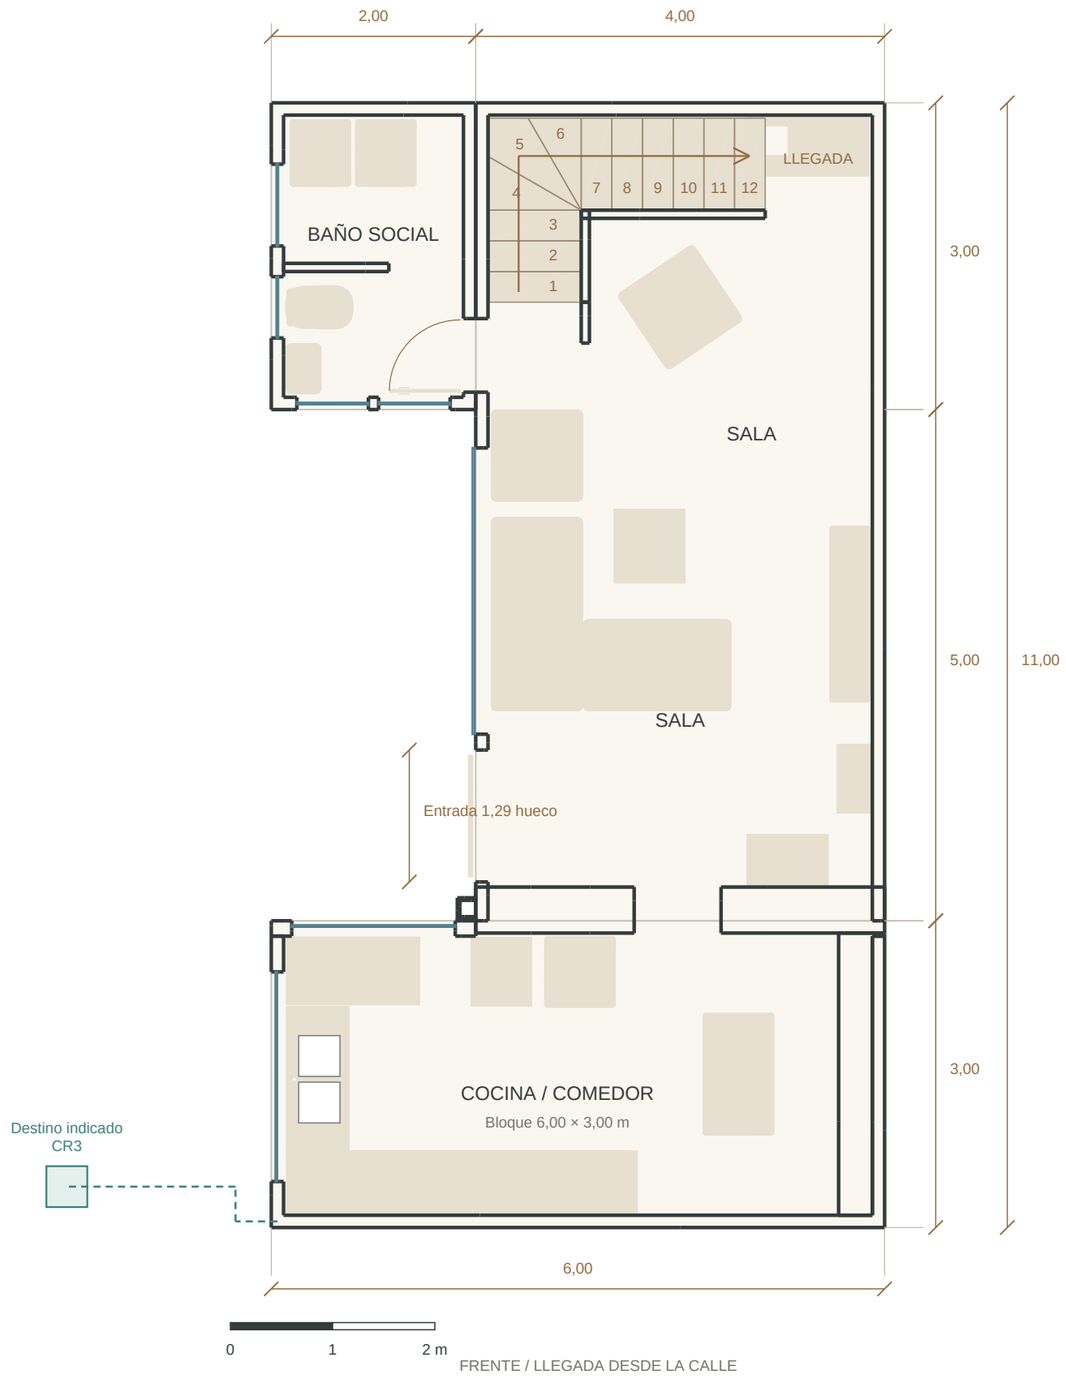

ESCALA 1:60 / A3 AL 100 %

No ajustar a página. Comprobar escala gráfica.

Cocina / comedor
6,00 × 3,00 m

Medida bruta; libre 5,43 × 2,76 m. Último cajonero retirado: mesón 77 cm más corto junto al comedor.

Sala / comedor abierto
4,00 × 8,00 m

Sin tabique entre sala y comedor.

Social con lavado
2,00 × 3,00 m

Máquinas al fondo tras pantalla de gypsum.

Piso cocina
0,00 m

Nivelado con sala; sin grada interior.

Entrada de una hoja
1,20 × 2,10 m objetivo

Apertura exterior. Hueco 1,29 × 2,15 m por verificar: cielo interior aproximado de 2,10 m.

Altura sala
2,10 m aprox.

Cara inferior del cielo modelado; verificar vigas.

NOTAS PARA REPLANTEO

Adobe 45 cm: paso cocina/sala y lateral del comedor. Retorno de bloque 15 cm; contorno exterior conservado.


Social: hoja de 70 cm y lavabo 50 × 35 cm. Ventanas de 60 × 75 y 80 × 75 cm, separadas por el paño donde remata el gypsum.

Gradas: 3 rectas + 3 compensadas + 6 rectas. Subidas 17,69 cm y huellas rectas 30 cm. Gypsum hasta techo; estructura por definir.

Paso cocina: luz aproximada 0,826 × 1,935 m. Conservar vano y replantear jambas y dintel.

Pisos nivelados: flotante en sala y porcelanato en cocina y baños. Verificar equipos, ventilación, placa para humedad y redes antes de fabricar.

Revisión 10/11/2026 · 3cde0d4d | Modelo y propuesta de coordinación - comprobar en sitio

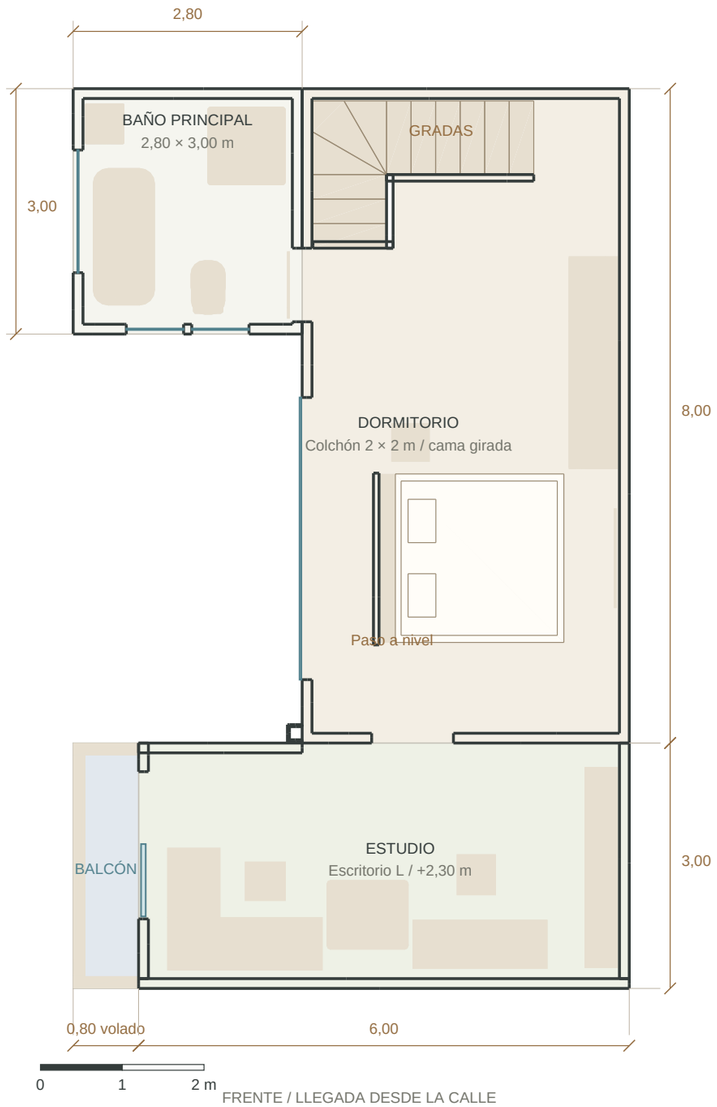

ESCALA 1:75 / A3 AL 100 %

No ajustar a página. Comprobar escala gráfica.

Dormitorio
4,00 × 8,00 m

Cabecero oeste en gypsum independiente; TV este frente a cama. Armario abierto de 2,60 m al noreste.

Estudio sobre cocina
6,00 × 3,00 m / 18,00 m² brutos

L y auxiliar en pared ciega; biblioteca lateral y paso al balcón libre. Altura libre 2,10 m.

Balcón lateral
0,80 × 3,00 m / 2,40 m² brutos

Antepecho revocado de 15 cm; libre aprox. 0,65 × 2,70 m. Carga y protección por calcular.

Piso y acceso al estudio
+2,30 m / sin peldaño

A nivel del dormitorio; cielo a +4,40 m, altura libre 2,10 m.

Baño principal
2,80 × 3,00 m

Eternit hacia casa; inclinación 12,14% en boceto. Cielo libre 2,20 m. Producto y solución de baja pendiente por confirmar.

Vacío de escalera
3,24 m² libres

L perimetral: corto 0,90 m, giro cuadrado 0,90 × 0,90 m y largo 1,80 m. Corte con tabique ≈3,31 m².

NOTAS PARA REPLANTEO


Gradas pegadas a baño y fondo: 3 rectas + 3 compensadas + 6 rectas. Subidas 17,69 cm; rectas 30 cm. Giro y estructura por replantear.

Colchón 2 × 2 m; base 2,06 × 2,06 m provisional. Tomas y lectura sólo en gypsum, nunca en cabezal.

Puertas adelantadas: social 35 cm; alta 75 cm. Lavabo de 50 cm y WC reubicados; tina y ducha conservadas. Adobe: rebaje 15 cm y refuerzo por calcular.

Dormitorio y estudio +2,30 m sin peldaño; cubierta común elevada 15 cm para conservar 2,10 m libres.

Revisión 10/11/2026 · 3cde0d4d | Modelo y propuesta de coordinación - comprobar en sitio

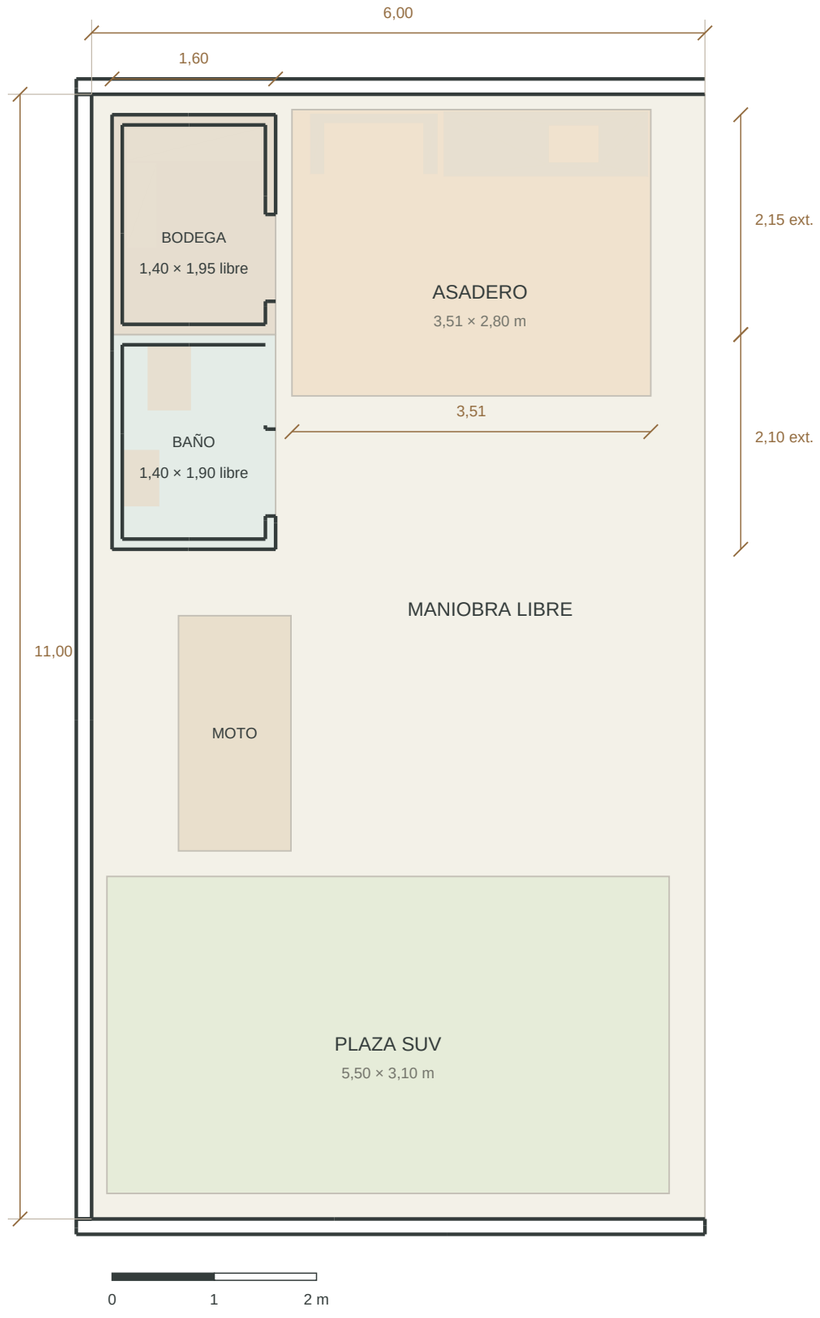

FRENTE / LLEGADA DESDE LA CALLE

ESCALA 1:60 / A3 AL 100 %

No ajustar a página. Comprobar escala gráfica.

Terreno patio
6,00 × 11,00 m
66 m²; las reservas interiores no se suman otra vez.

Servicios exterior
1,60 × 4,25 m
Modelo · verificar en sitio

Baño libre
1,40 × 1,90 m
Libre modelado; medir antes de levantar muros.

Bodega libre
1,40 × 1,95 m
Modelo · verificar en sitio

Asadero
3,51 × 2,80 m
Modelo · verificar en sitio

SUV / moto
5,50 × 3,10 / 1,10 × 2,30 m
Reservas de parqueo; mantener libre el giro.

NOTAS PARA REPLANTEO

Baño y asadero con porcelanato beige. Bodega con adoquín del patio.

Ventana de baño patio ampliada a 0,75 × 0,60 m, vidrio de privacidad.


Una sola cubierta en L para moto, baño, bodega y asadero.

Ventilación, agua, desagües y separación de chimenea por definir en sitio.

E-01T · Tomacorrientes y equipos · Planta baja

CASA LALES · MAPA COMPLETO · ESCALA 1:40 · IMPRIMIR AL 100 %

Revisión 10/11/2026 · 3cde0d4d

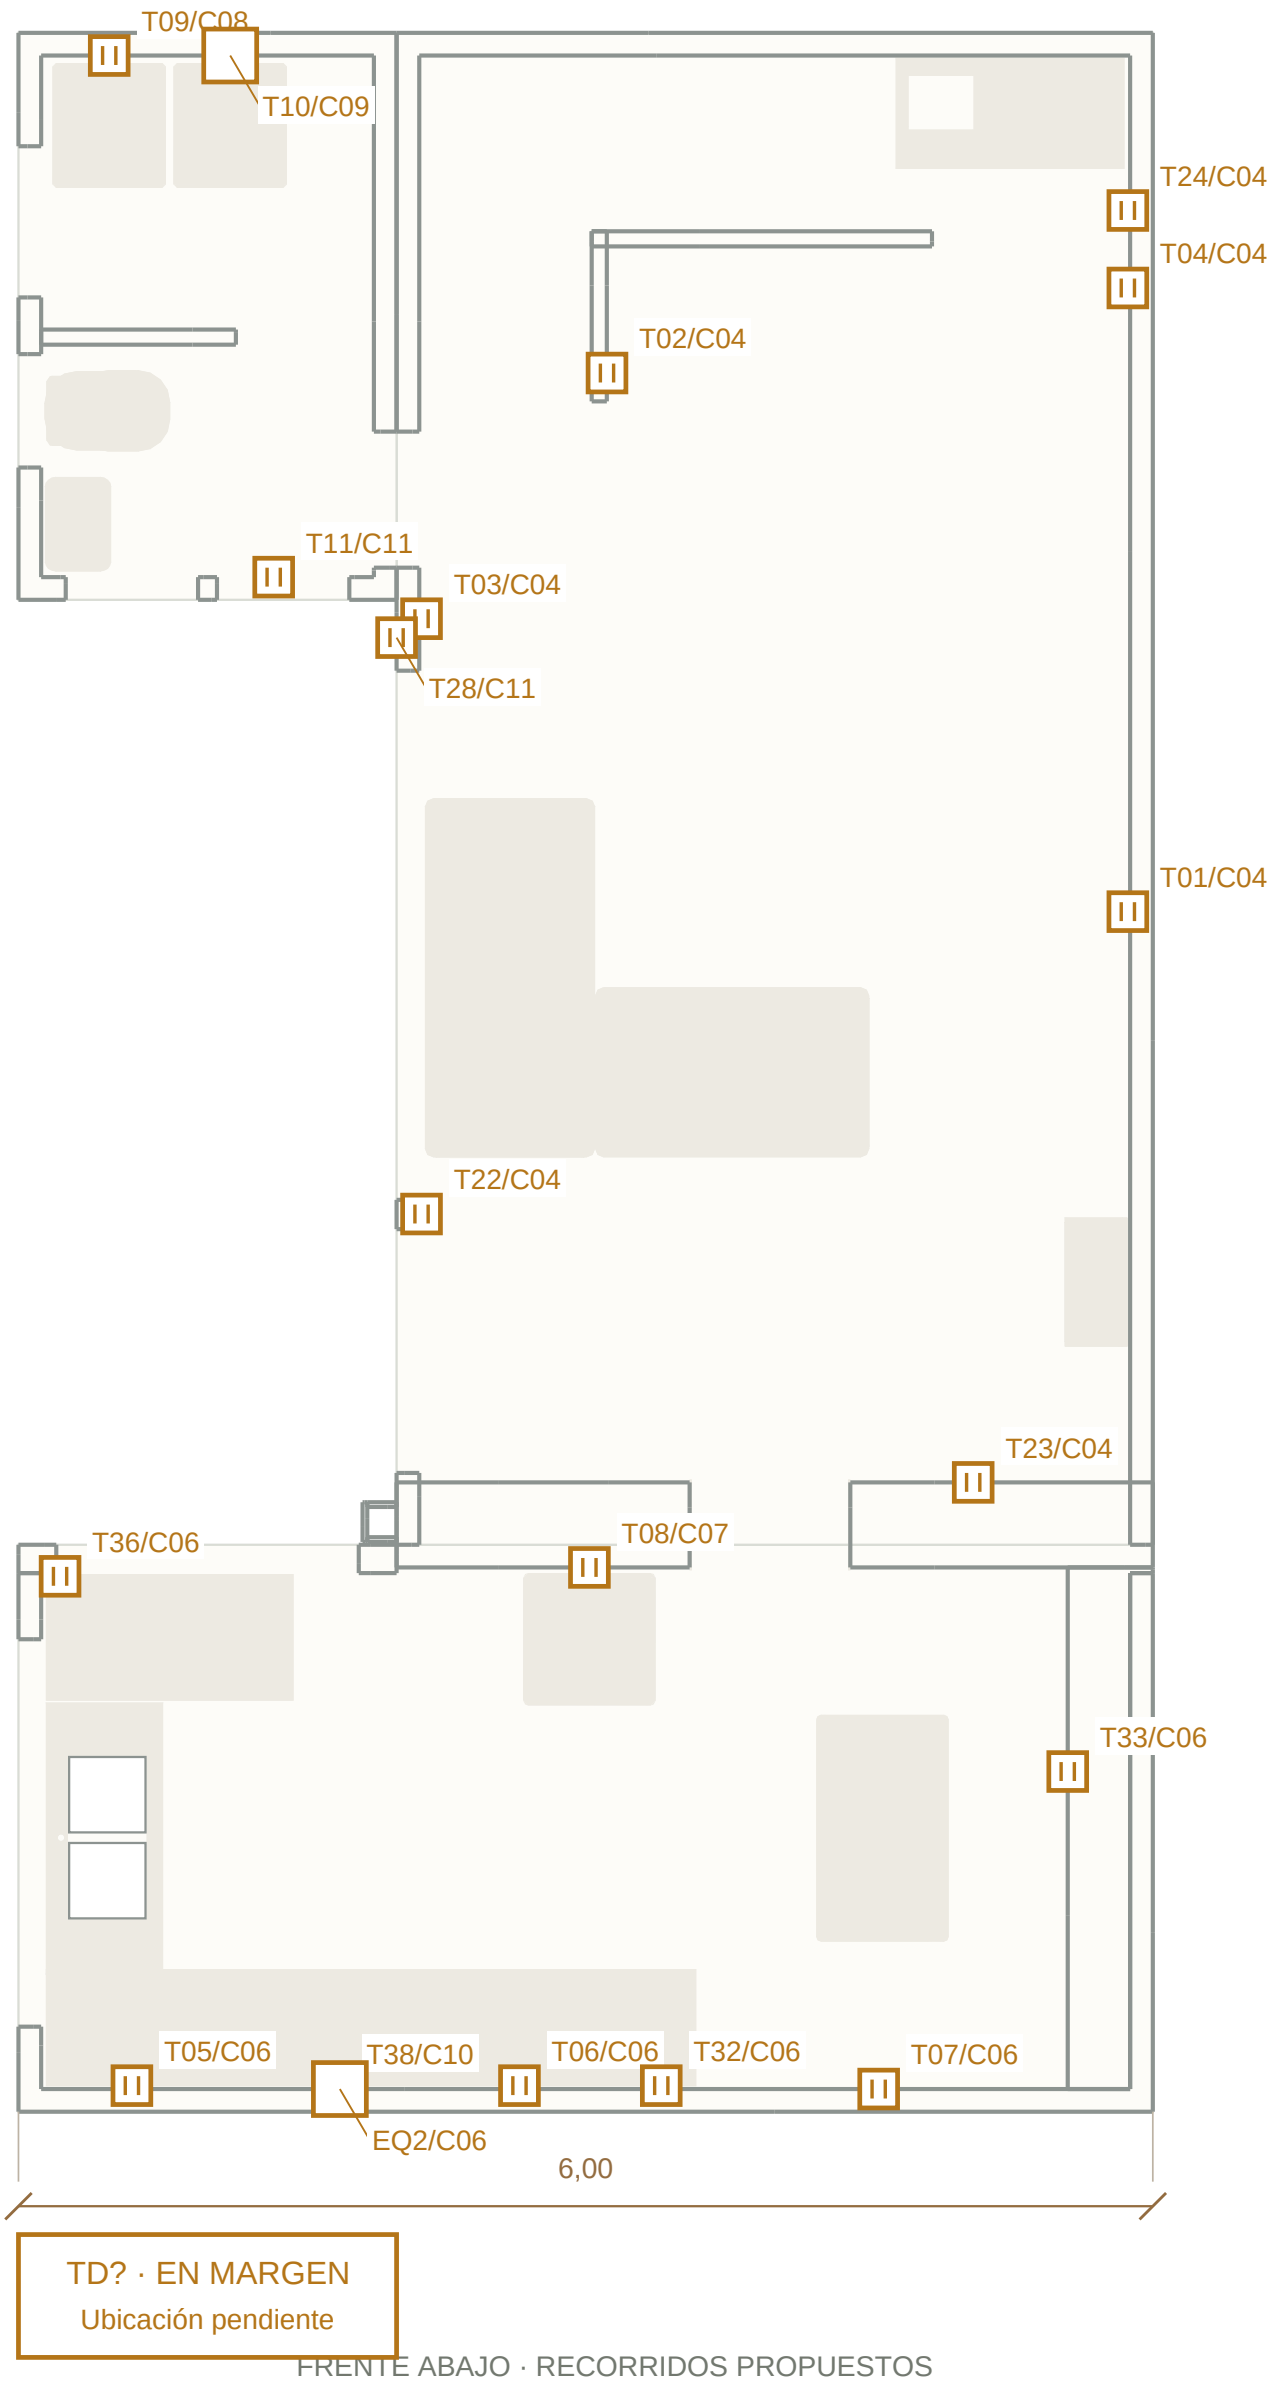

Simbología y notas en la hoja siguiente.

EXPLICACIÓN · E-01T

Tomacorrientes y equipos · Planta baja

Casa Lales · Revisión 10/11/2026 · 3cde0d4d

QUÉ SIGNIFICA CADA FIGURA



Cuadrado con dos rayas · T

Tomacorriente. Código T y grupo C coinciden con el visor 3D; no indican voltaje ni amperaje.



Cuadrado vacío · reserva

EQ1: cocción; EQ2: campana. T10: conexión de secadora por definir según equipo.



Líneas grises · muro

Paredes del modelo como referencia para situar los puntos.



C04-C11 · grupo funcional

El sufijo /C identifica un uso propuesto, sujeto al cálculo de cargas y protecciones.



Rectángulo TD? · tablero

Se dibuja al margen. La ubicación y las protecciones siguen pendientes.



Figura beige · mueble o aparato

Huella de referencia; se conservan las posiciones del modelo.

DATOS Y CRITERIOS DEL PLANO

Tomacorrientes: 19 puntos

Códigos T conservados. /C identifica grupo funcional; no es voltaje ni capacidad.

Reservas de equipos: 1 cajas

EQ: conexión de equipo por definir. T10 sigue identificado como reserva para secadora.

Plano de luces y mandos: E-01L

Consultar su mapa independiente; no se representan aquí sus símbolos.

NOTAS PARA REVISIÓN EN OBRA

Mismas posiciones y códigos que en imágenes 3D; alturas propuestas. Cabezal sin instalaciones.

Dimensiones y capacidades de conductores, protecciones y puesta a tierra pendientes de cálculo.


T10 es caja de conexión por definir según secadora; no se asigna tensión.

Baños y exterior: posición, protección y equipo apropiado por validar.

E-01L · Iluminación y mandos · Planta baja

CASA LALES · MAPA COMPLETO · ESCALA 1:40 · IMPRIMIR AL 100 %

Revisión 10/11/2026 · 3cde0d4d

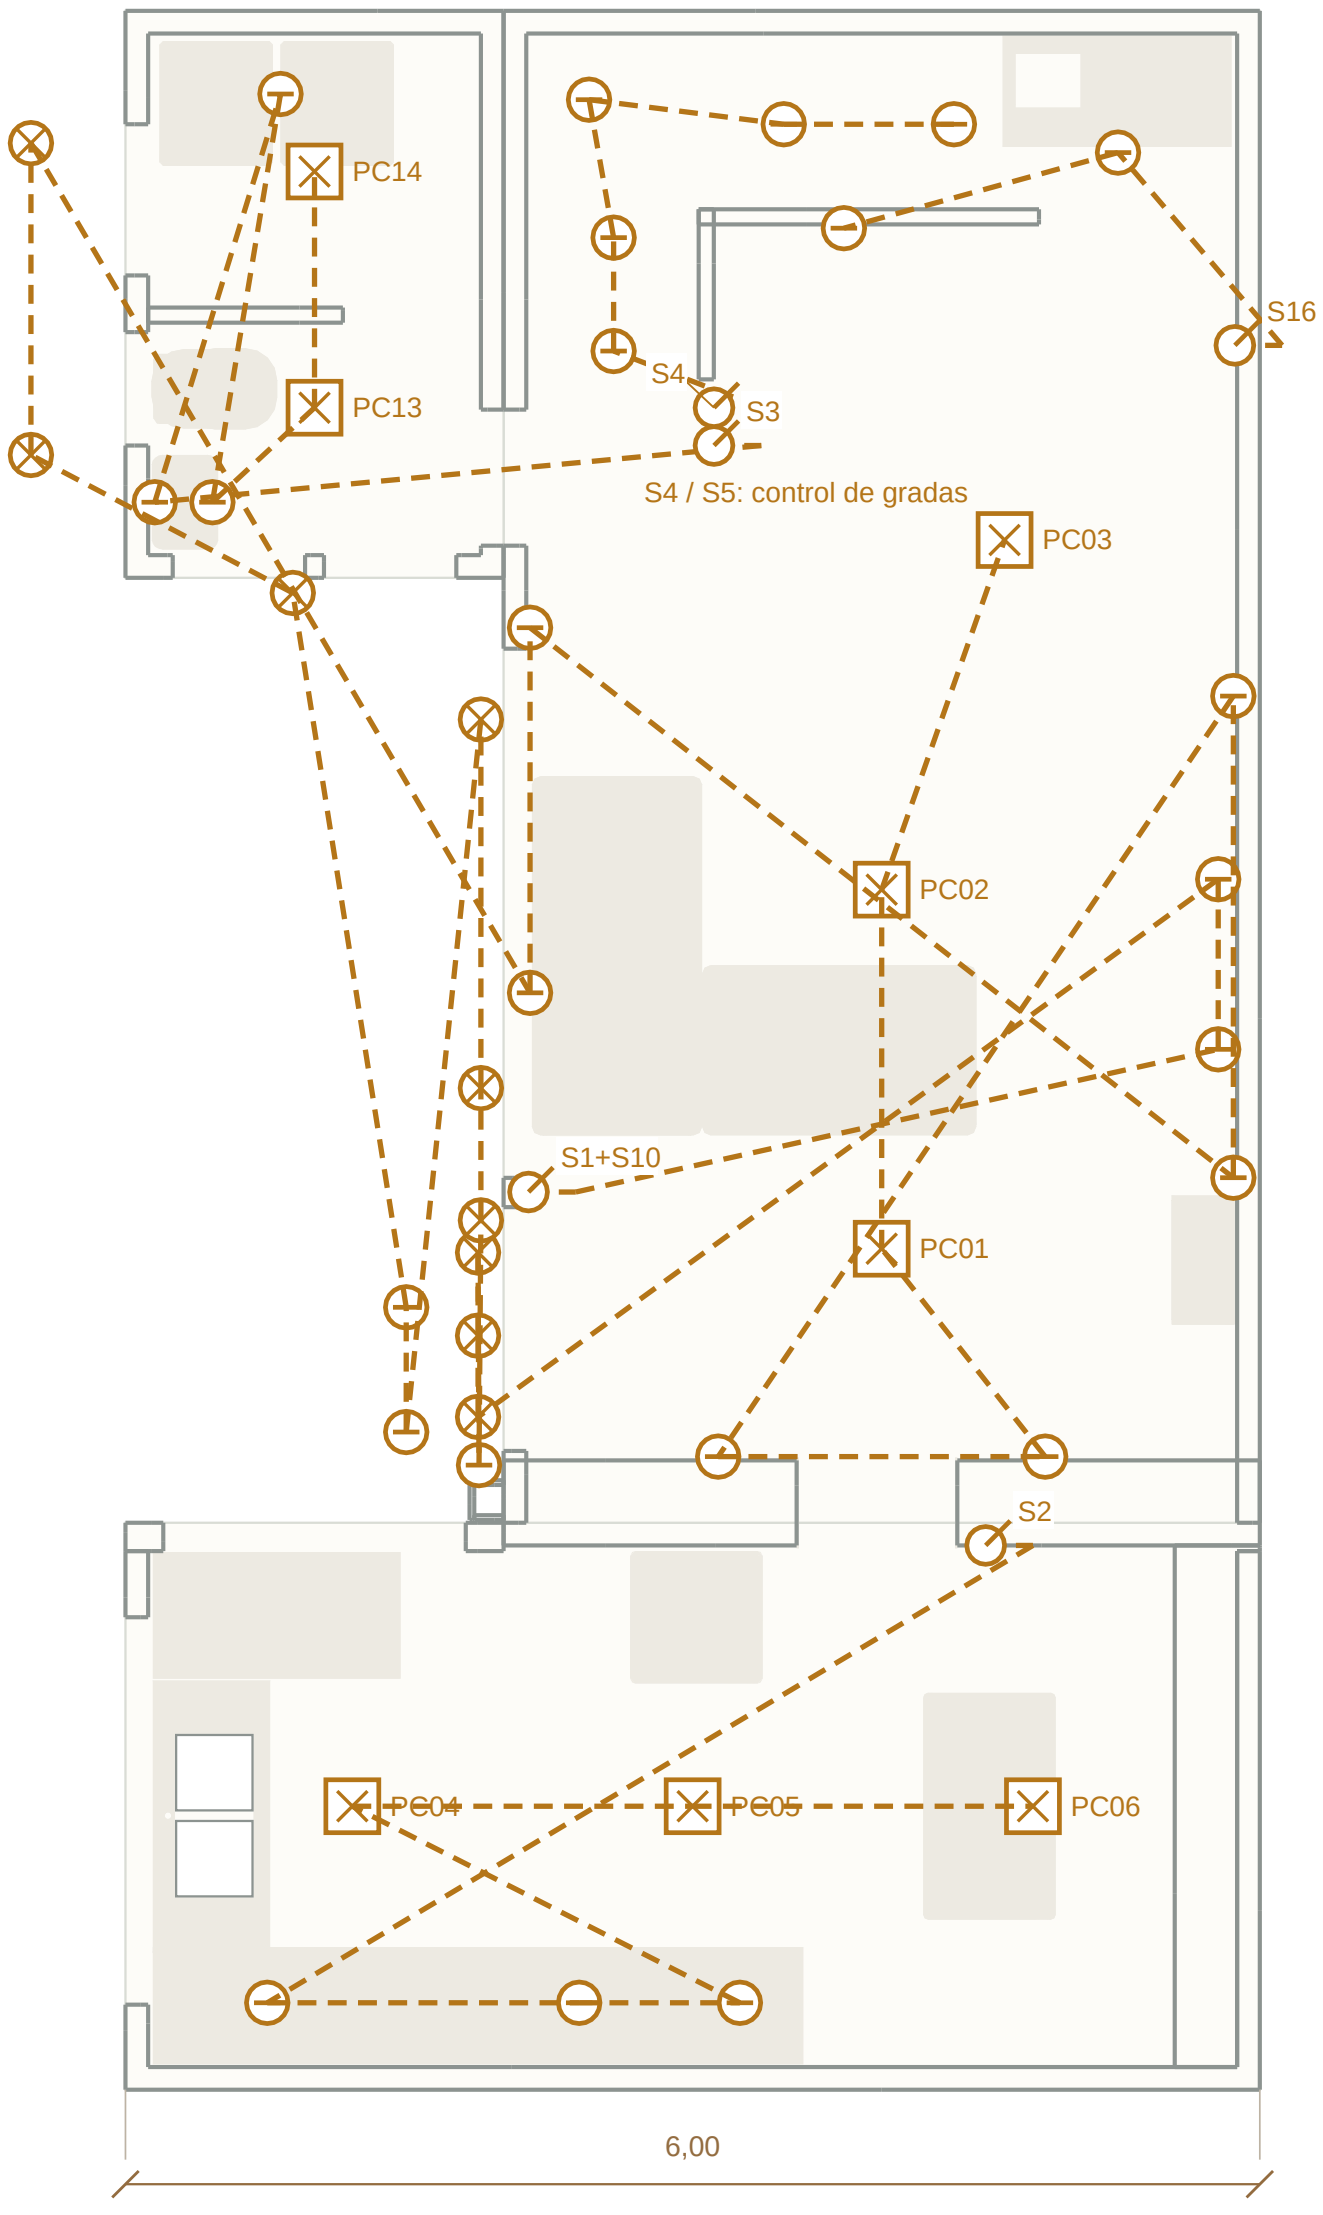

FRENTE ABAJO · RECORRIDOS PROPUESTOS

Simbología y notas en la hoja siguiente.

EXPLICACIÓN · E-01L

Iluminación y mandos · Planta baja

Casa Lales · Revisión 10/11/2026 · 3cde0d4d

QUÉ SIGNIFICA CADA FIGURA

Cuadrado con X · plafón PC
Lámpara cuadrada de sobreponer. Cada código PC identifica una unidad; potencia y temperatura en el cuadro de esta hoja.

Círculo con X · luz general
Punto de iluminación general del modelo. No equivale siempre a una unidad comercial.

Círculo con raya · luz de apoyo
Referencia de trabajo o ambiente: LED, espejo, mueble, aplique o escalón.

Círculo con trazo · S
Interruptor o caja de teclas. Misma posición y código que el visor; S4/S5 coordinan las gradas.

Línea punteada · relación de mando
Relaciona el mando con sus luces. No fija un cableado, conductores ni trayecto de ejecución.

Líneas grises · muro
Paredes del modelo como referencia para situar los puntos.

Figura beige · mueble o aparato
Huella de referencia; se conservan las posiciones del modelo.

DATOS Y CRITERIOS DEL PLANO

Iluminación general: 8 plafones PC / 9 otros
Cuadrado con X: plafón PC; círculo con X: otra luz general.

Luz de trabajo / ambiente: 24 referencias
Círculo con raya; incluye LED, apliques y apoyos.

Cajas de mandos: S1+S10, S2, S3, S4, S16
S4/S5: coordinar el control de gradas desde ambos niveles.

Plano de tomacorrientes: E-01T
Consultar su mapa independiente; no se representan aquí sus símbolos.

Sala: 3 × 24 W · 3000 K
Interior seco

Cocina y comedor: 3 × 24 W · 4000 K
Interior seco

Baño social y lavandería: 2 × 12 W · 4000 K
Sellado para zona húmeda; por confirmar

NOTAS PARA REVISIÓN EN OBRA

Mismas tomas y mandos que en imágenes 3D. Alturas propuestas; dormitorio según distribución aplicada.

Líneas punteadas: relación de mando y recorrido conceptual; no son número de conductores.

Grupos C01-C12 funcionales: dividir por planta, cargas y protecciones en cálculo. Tablero y tierra pendientes.

Bajo Eternit: canalización y cajas fijadas a soporte definido, nunca a las planchas.

Las luces de gradas se asignan a PB o PA por cota: cada referencia aparece una sola vez.

PC: plafón cuadrado sobrepuesto. Modelo seco de referencia 28,5 × 28,5 × 2,8 cm, 24 W, 1800 lm, 0,583 kg; 100–240 V. Confirmar equipo y suministro.

Fijar herraje a perfil/refuerzo del cielo; no cargar sólo la placa. Revisar perfilería, anclaje y acceso al driver; no suspender del Eternit.


Baños: variante sellada IP44 mínimo; IP65 si la zona lo exige. Potencia y formato menores orientativos; modelo y protección por elegir.

Plafón de referencia sin dimmer. LED indirecto y tarea separados. Cantidad propuesta; verificar iluminación con fotometría y medidas reales.

E-02T · Tomacorrientes y equipos · Planta alta

CASA LALES · MAPA COMPLETO · ESCALA 1:40 · IMPRIMIR AL 100 %

Revisión 10/11/2026 · 3cde0d4d

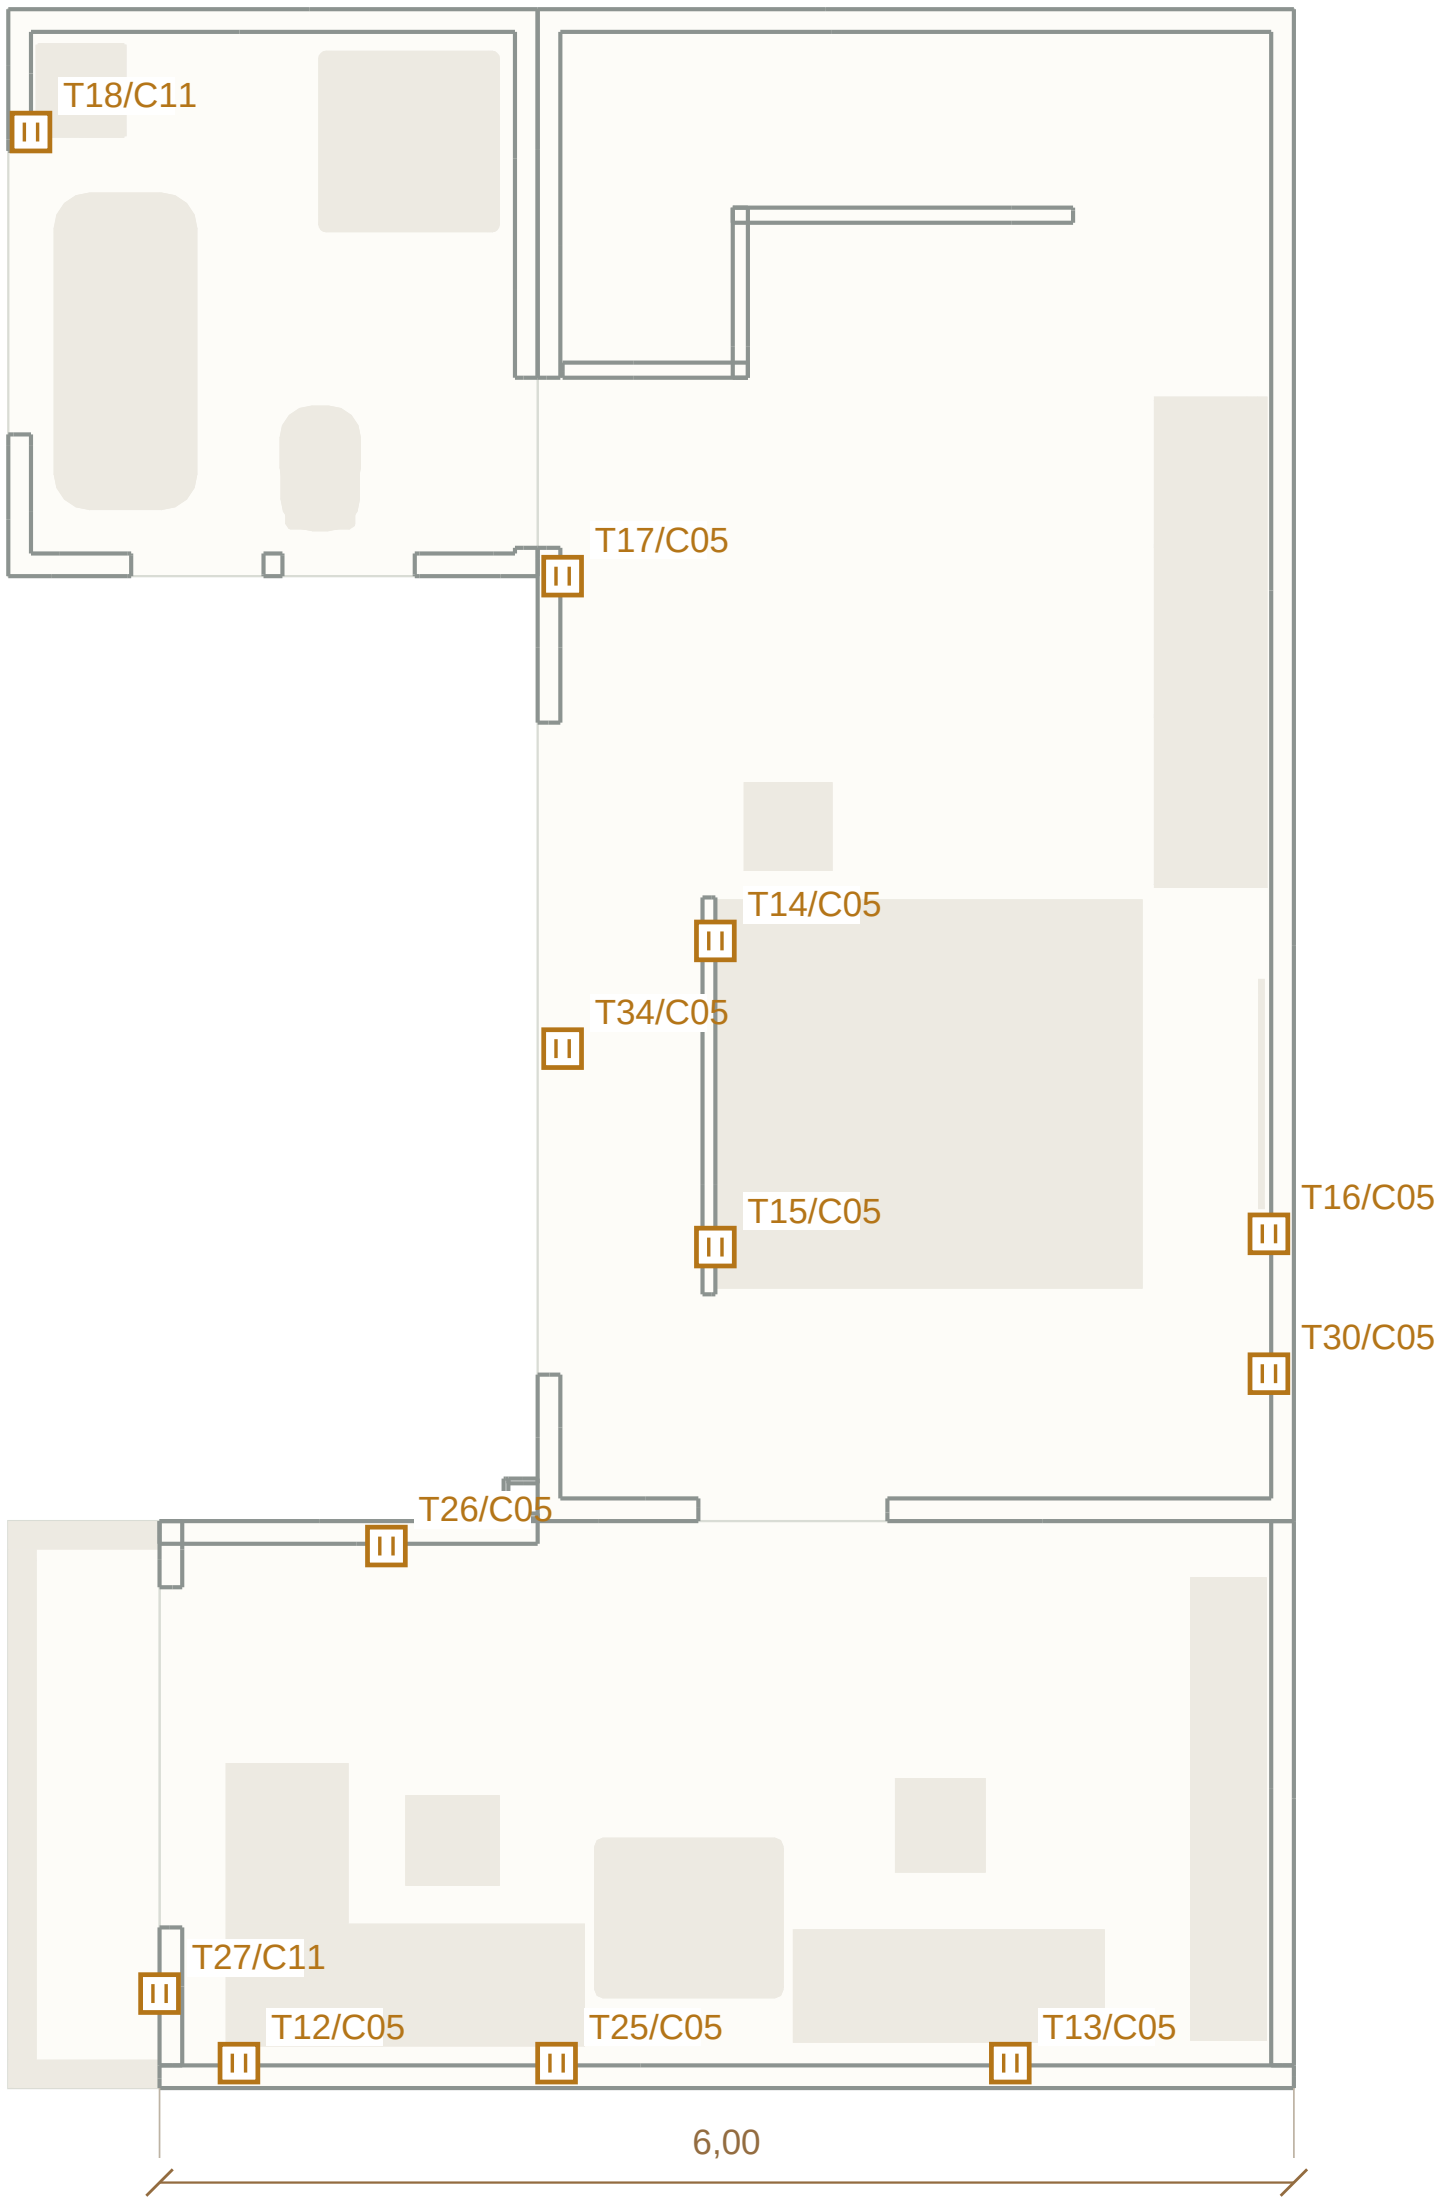

FRENTE ABAJO · RECORRIDOS PROPUESTOS

Simbología y notas en la hoja siguiente.

EXPLICACIÓN · E-02T

Tomacorrientes y equipos · Planta alta

Casa Lales · Revisión 10/11/2026 · 3cde0d4d

QUÉ SIGNIFICA CADA FIGURA



Cuadrado con dos rayas · T

Tomacorriente. Código T y grupo C coinciden con el visor 3D; no indican voltaje ni amperaje.

C01

C04-C11 · grupo funcional

El sufijo /C identifica un uso propuesto, sujeto al cálculo de cargas y protecciones.



Líneas grises · muro

Paredes del modelo como referencia para situar los puntos.



Figura beige · mueble o aparato

Huella de referencia; se conservan las posiciones del modelo.

DATOS Y CRITERIOS DEL PLANO

Tomacorrientes: 12 puntos

Códigos T conservados. /C identifica grupo funcional; no es voltaje ni capacidad.

Reservas de equipos: 0 cajas

No hay cajas EQ adicionales en este nivel.

Plano de luces y mandos: E-02L

Consultar su mapa independiente; no se representan aquí sus símbolos.

NOTAS PARA REVISIÓN EN OBRA

Mismas posiciones y códigos que en imágenes 3D; alturas propuestas. Cabezal sin instalaciones.


Dimensiones y capacidades de conductores, protecciones y puesta a tierra pendientes de cálculo.

Baños y exterior: posición, protección y equipo apropiado por validar.

E-02L · Iluminación y mandos · Planta alta

CASA LALES · MAPA COMPLETO · ESCALA 1:40 · IMPRIMIR AL 100 %

Revisión 10/11/2026 · 3cde0d4d

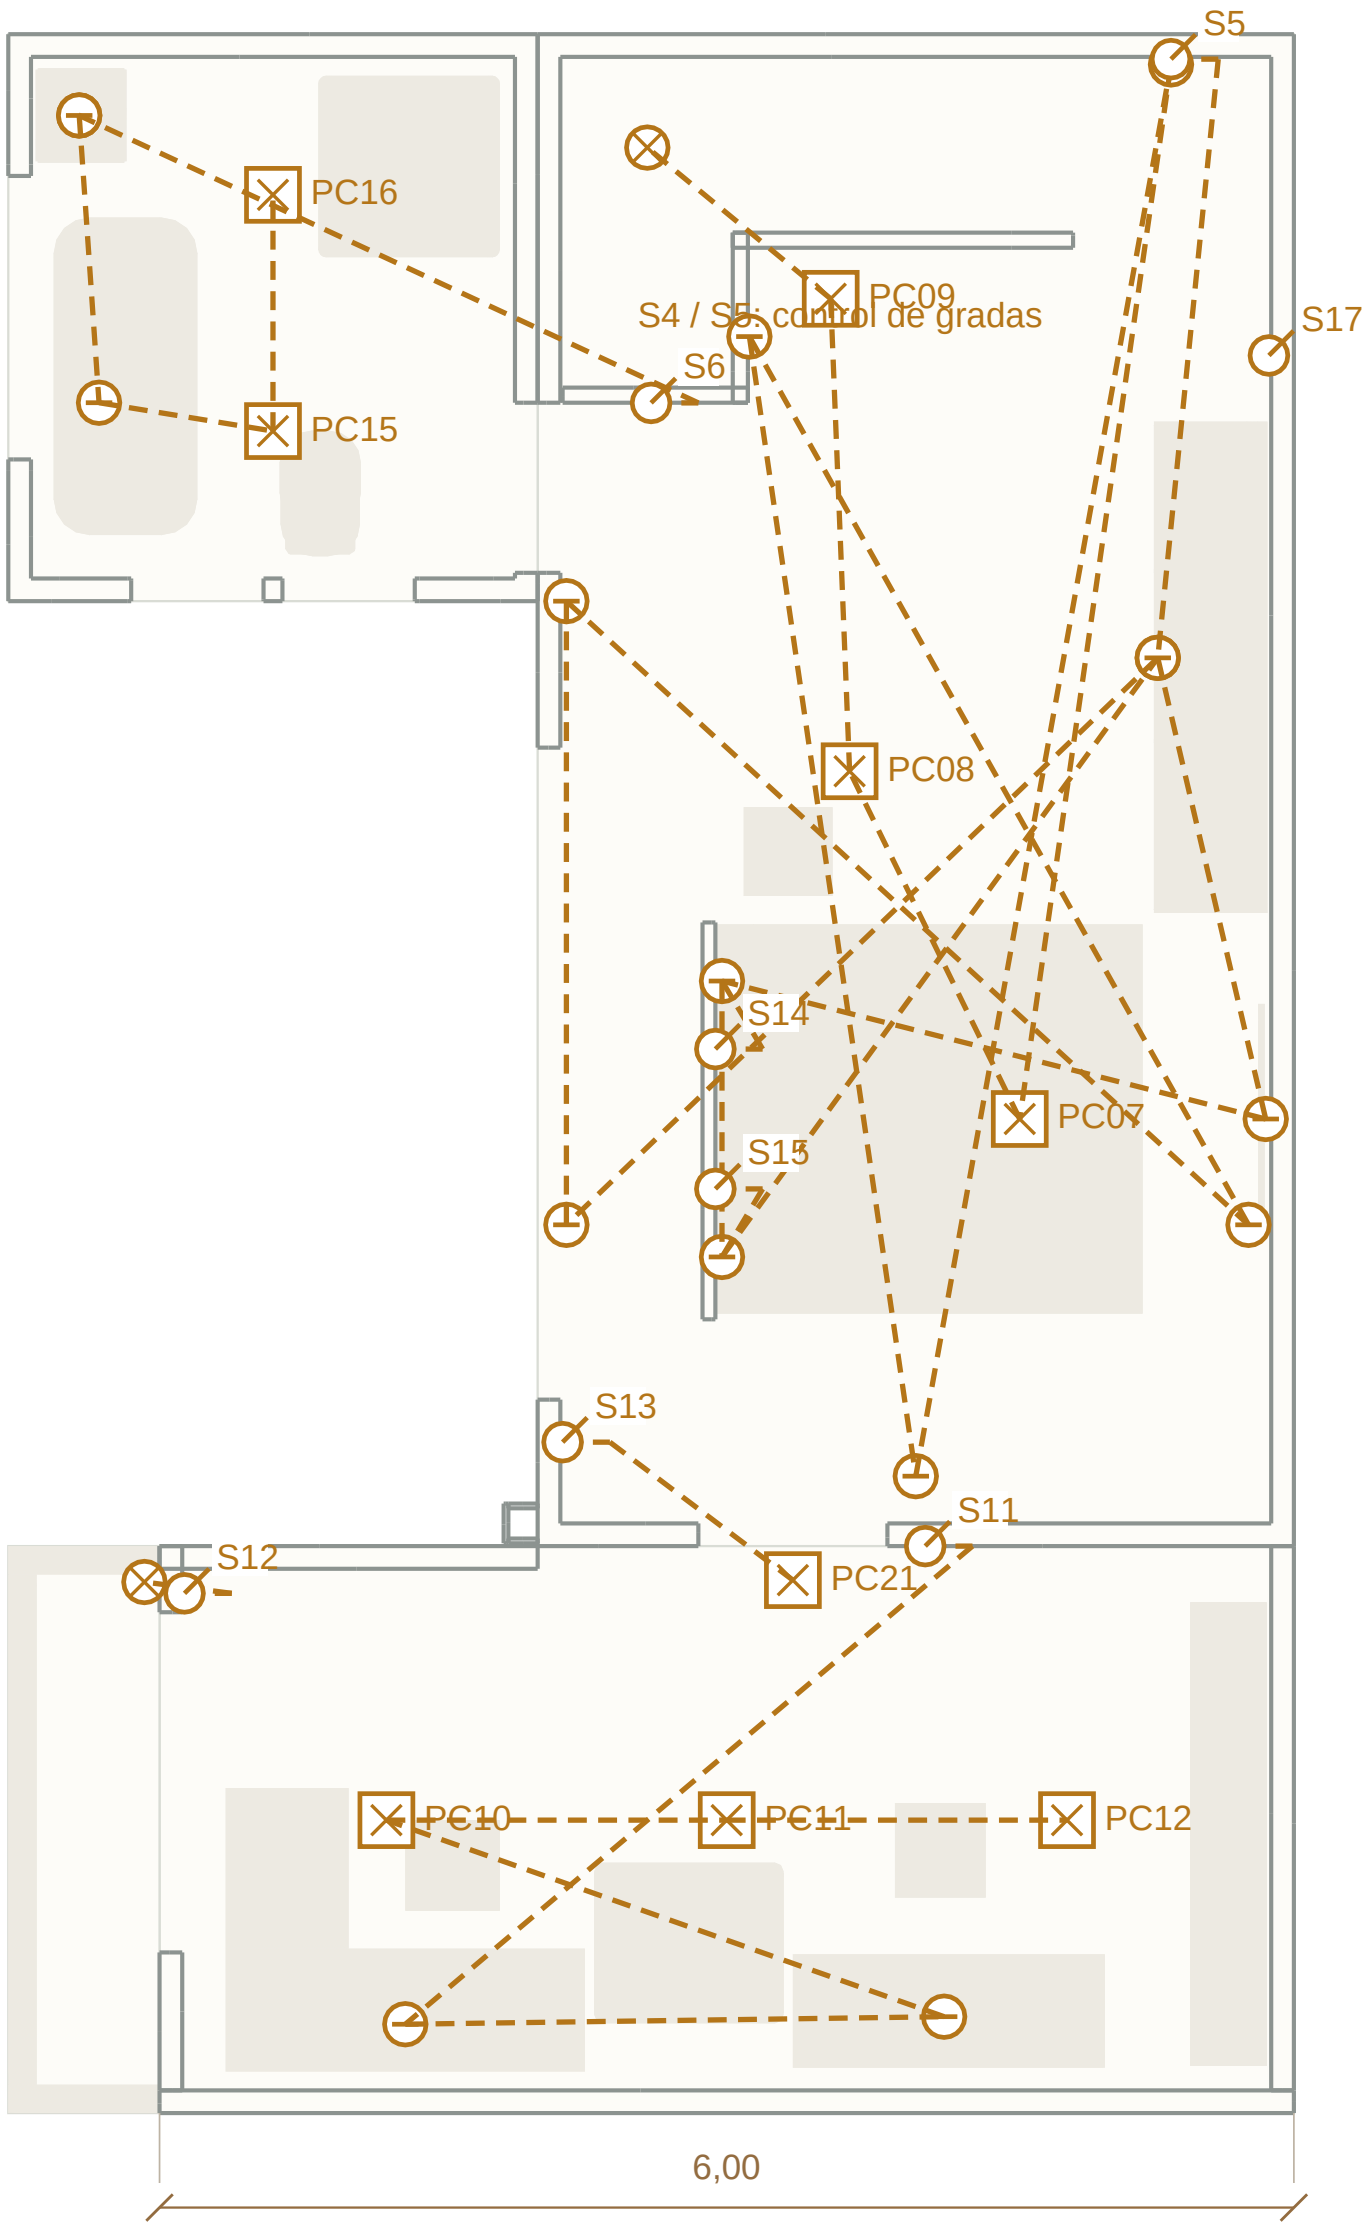

FRENTE ABAJO · RECORRIDOS PROPUESTOS

Simbología y notas en la hoja siguiente.

EXPLICACIÓN · E-02L

Iluminación y mandos · Planta alta

Casa Lales · Revisión 10/11/2026 · 3cde0d4d

QUÉ SIGNIFICA CADA FIGURA

Cuadrado con X · plafón PC
Lámpara cuadrada de sobreponer. Cada código PC identifica una unidad; potencia y temperatura en el cuadro de esta hoja.

Círculo con X · luz general
Punto de iluminación general del modelo. No equivale siempre a una unidad comercial.

Círculo con raya · luz de apoyo
Referencia de trabajo o ambiente: LED, espejo, mueble, aplique o escalón.

Círculo con trazo · S
Interruptor o caja de teclas. Misma posición y código que el visor; S4/S5 coordinan las gradas.

Línea punteada · relación de mando
Relaciona el mando con sus luces. No fija un cableado, conductores ni trayecto de ejecución.

Líneas grises · muro
Paredes del modelo como referencia para situar los puntos.

Figura beige · mueble o aparato
Huella de referencia; se conservan las posiciones del modelo.

DATOS Y CRITERIOS DEL PLANO

Iluminación general: 9 plafones PC / 2 otros
Cuadrado con X: plafón PC; círculo con X: otra luz general.

Luz de trabajo / ambiente: 16 referencias
Círculo con raya; incluye LED, apliques y apoyos.

Cajas de mandos: S5, S17, S6, S13, S14, S15, S11, S12
S4/S5: coordinar el control de gradas desde ambos niveles.

Plano de tomacorrientes: E-02T
Consultar su mapa independiente; no se representan aquí sus símbolos.

Dormitorio y armarios: 3 × 24 W · 3000 K
Interior seco

Estudio: 3 × 24 W · 4000 K
Interior seco

Baño principal: 2 × 18 W · 4000 K
Eternit hacia casa; inclinación 12,14% en boceto. Cielo libre 2,20 m. Producto y solución de baja pendiente por confirmar.

Acceso al estudio: 1 × 12 W · 3000 K
Interior seco

NOTAS PARA REVISIÓN EN OBRA

Mismas tomas y mandos que en imágenes 3D. Alturas propuestas; dormitorio según distribución aplicada.

Líneas punteadas: relación de mando y recorrido conceptual; no son número de conductores.

Grupos C01-C12 funcionales: dividir por planta, cargas y protecciones en cálculo. Tablero y tierra pendientes.

Bajo Eternit: canalización y cajas fijadas a soporte definido, nunca a las planchas.

Las luces de gradas se asignan a PB o PA por cota: cada referencia aparece una sola vez.

PC: plafón cuadrado sobrepuesto. Modelo seco de referencia 28,5 × 28,5 × 2,8 cm, 24 W, 1800 lm, 0,583 kg; 100–240 V. Confirmar equipo y suministro.

Fijar herraje a perfil/refuerzo del cielo; no cargar sólo la placa. Revisar perfilería, anclaje y acceso al driver; no suspender del Eternit.


Baños: variante sellada IP44 mínimo; IP65 si la zona lo exige. Potencia y formato menores orientativos; modelo y protección por elegir.

Plafón de referencia sin dimmer. LED indirecto y tarea separados. Cantidad propuesta; verificar iluminación con fotometría y medidas reales.

E-03T · Tomacorrientes y equipos · Patio

CASA LALES · MAPA COMPLETO · ESCALA 1:40 · IMPRIMIR AL 100 %

Revisión 10/11/2026 · 3cde0d4d

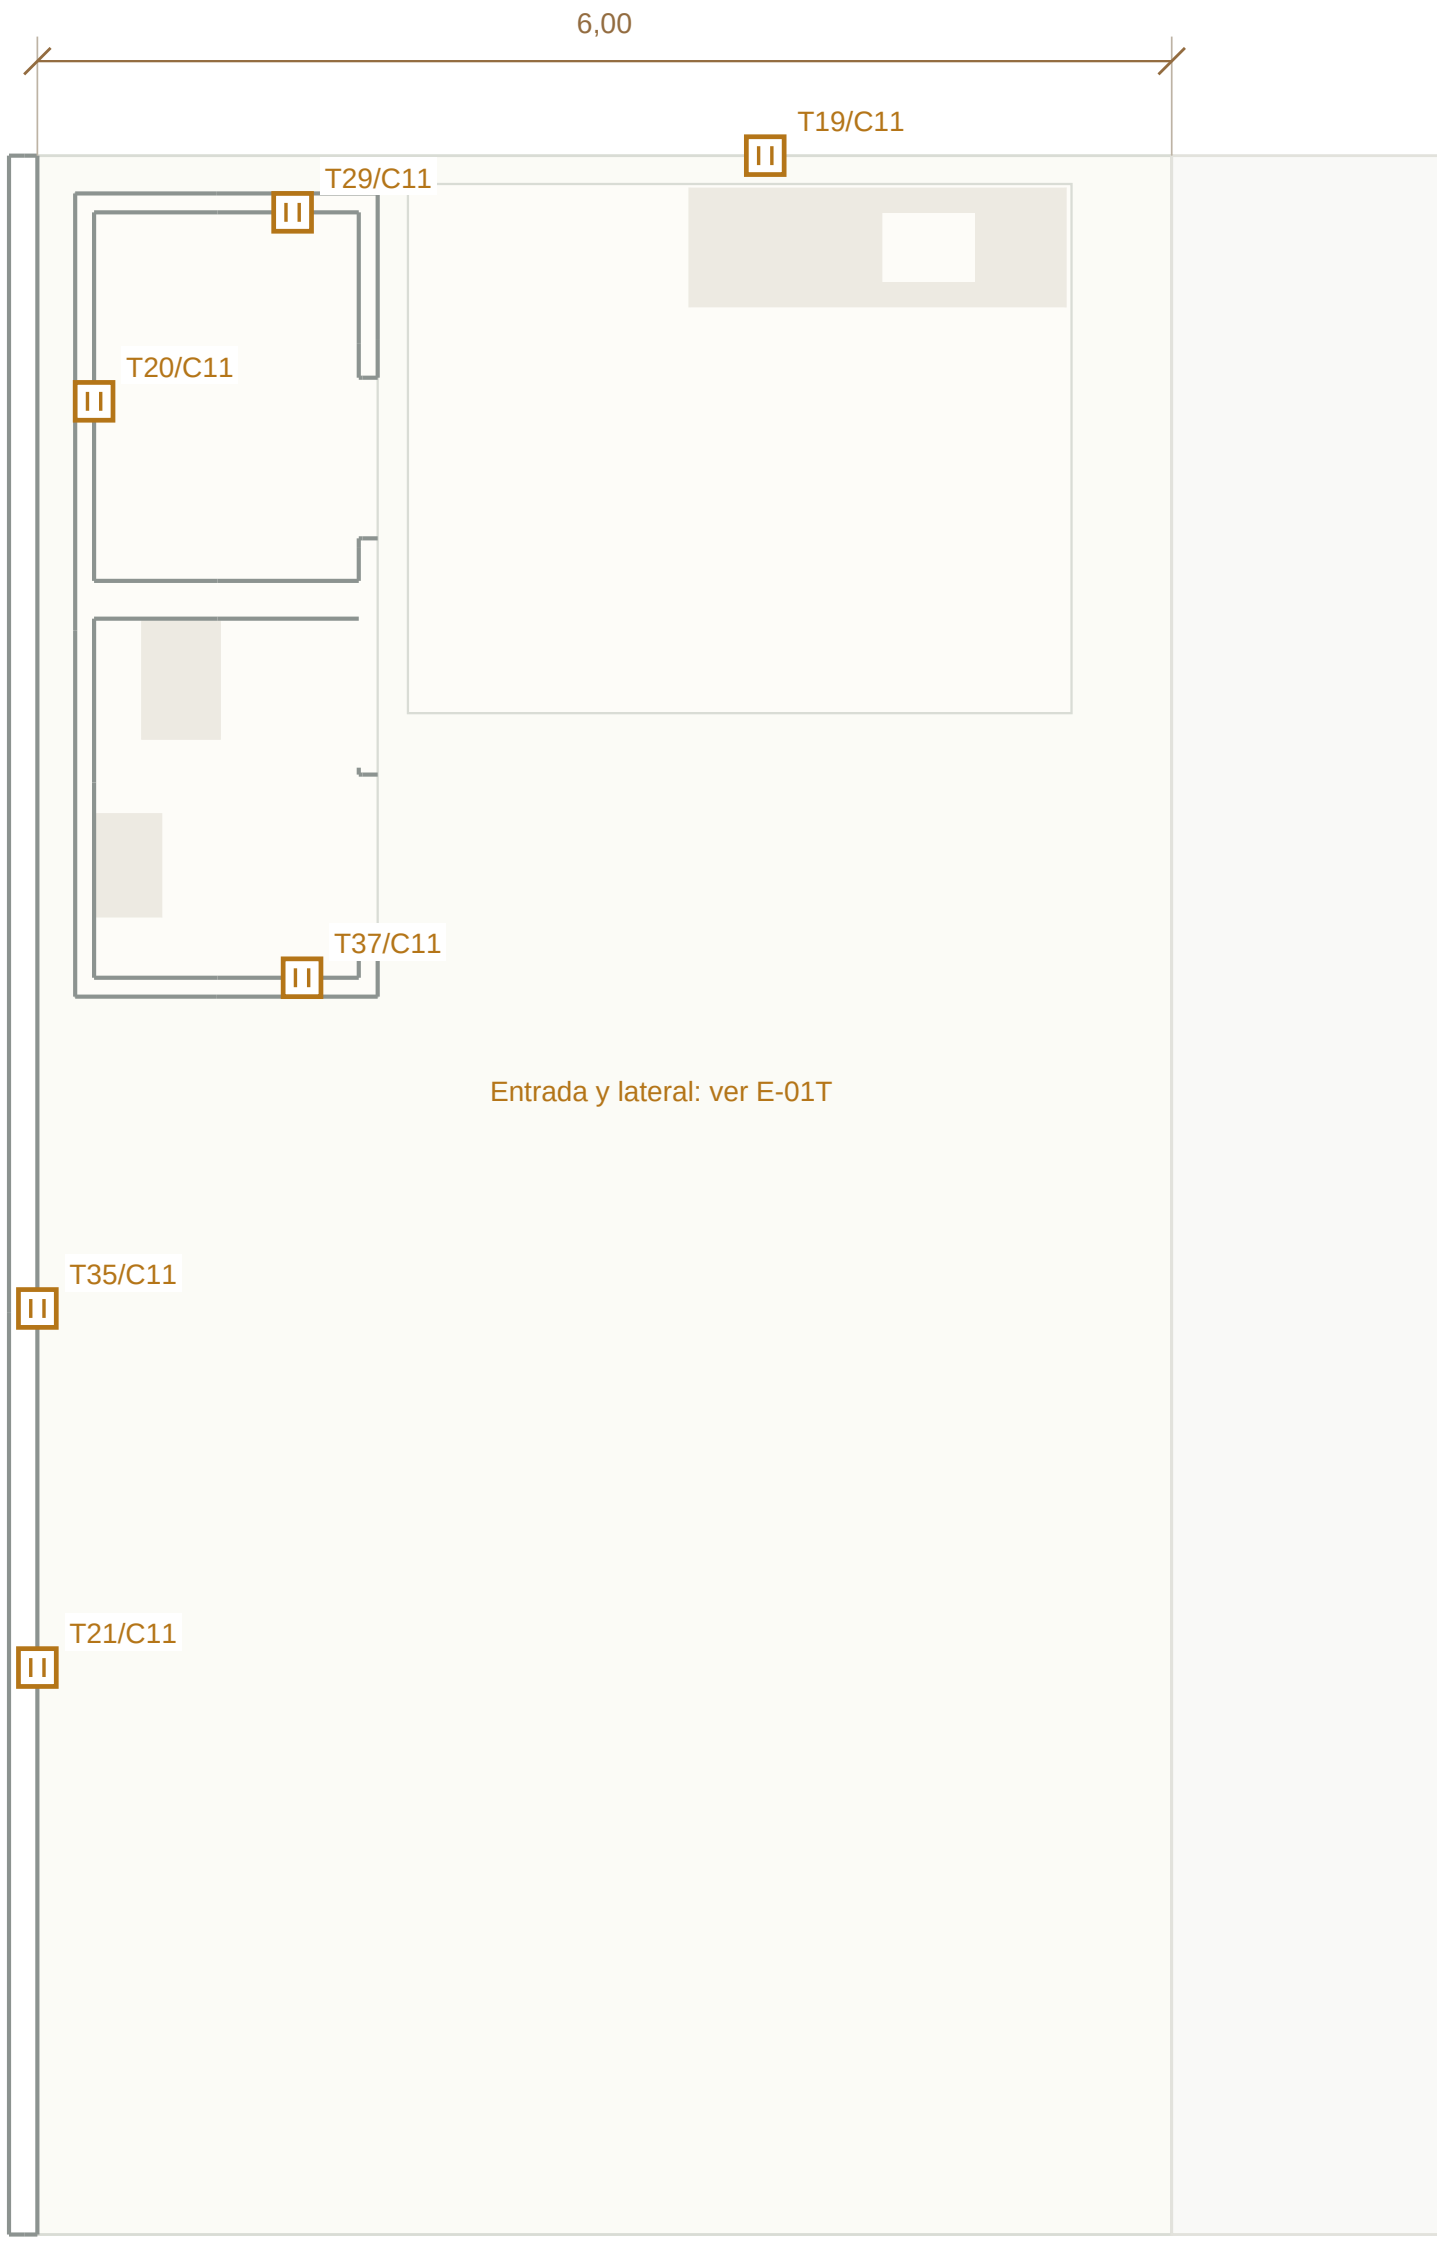

FRENTE ABAJO · RECORRIDOS PROPUESTOS

Simbología y notas en la hoja siguiente.

EXPLICACIÓN · E-03T

Tomacorrientes y equipos · Patio

Casa Lales · Revisión 10/11/2026 · 3cde0d4d

QUÉ SIGNIFICA CADA FIGURA



Cuadrado con dos rayas · T

Tomacorriente. Código T y grupo C coinciden con el visor 3D; no indican voltaje ni amperaje.

C01

C04-C11 · grupo funcional

El sufijo /C identifica un uso propuesto, sujeto al cálculo de cargas y protecciones.



Líneas grises · muro

Paredes del modelo como referencia para situar los puntos.



Figura beige · mueble o aparato

Huella de referencia; se conservan las posiciones del modelo.

DATOS Y CRITERIOS DEL PLANO

Tomacorrientes: 6 puntos

Códigos T conservados. /C identifica grupo funcional; no es voltaje ni capacidad.

Reservas de equipos: 0 cajas

No hay cajas EQ adicionales en este nivel.

Plano de luces y mandos: E-03L

Consultar su mapa independiente; no se representan aquí sus símbolos.

NOTAS PARA REVISIÓN EN OBRA

Mismas posiciones y códigos que en imágenes 3D; alturas propuestas. Cabezal sin instalaciones.


Dimensiones y capacidades de conductores, protecciones y puesta a tierra pendientes de cálculo.

Baños y exterior: posición, protección y equipo apropiado por validar.

E-03L · Iluminación y mandos · Patio

CASA LALES · MAPA COMPLETO · ESCALA 1:40 · IMPRIMIR AL 100 %

Revisión 10/11/2026 · 3cde0d4d

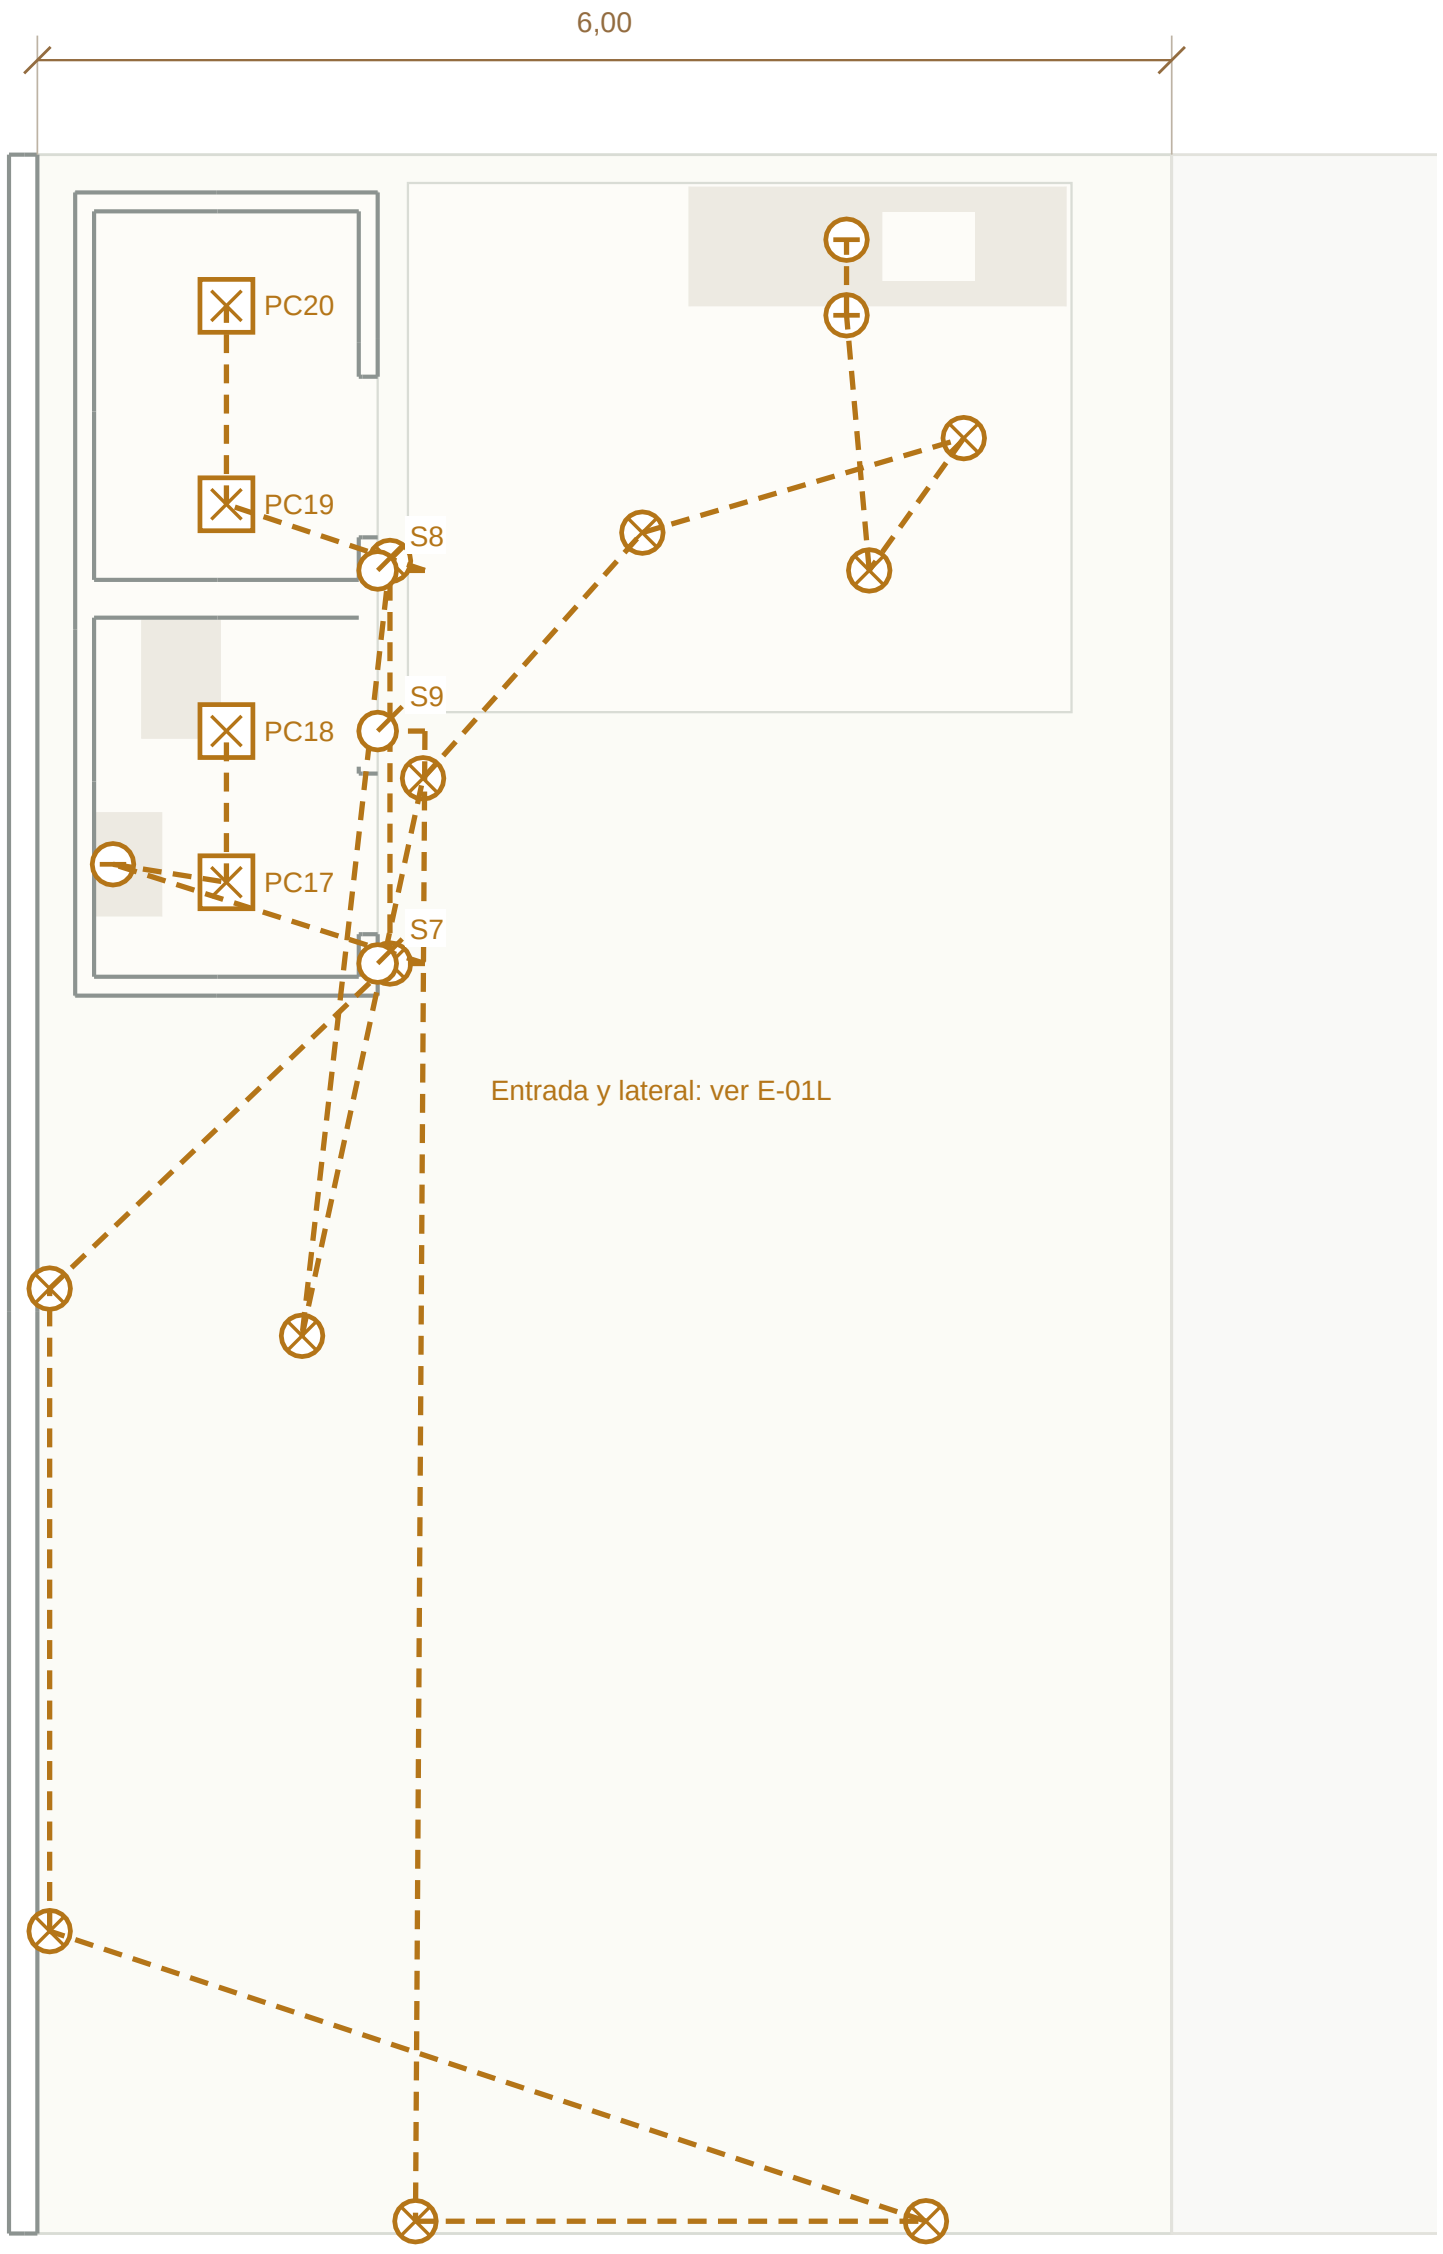

FRENTE ABAJO · RECORRIDOS PROPUESTOS

Simbología y notas en la hoja siguiente.

EXPLICACIÓN · E-03L

Iluminación y mandos · Patio

Casa Lales · Revisión 10/11/2026 · 3cde0d4d

QUÉ SIGNIFICA CADA FIGURA

Cuadrado con X · plafón PC
Lámpara cuadrada de sobreponer. Cada código PC identifica una unidad; potencia y temperatura en el cuadro de esta hoja.

Círculo con X · luz general
Punto de iluminación general del modelo. No equivale siempre a una unidad comercial.

Círculo con raya · luz de apoyo
Referencia de trabajo o ambiente: LED, espejo, mueble, aplique o escalón.

Círculo con trazo · S
Interruptor o caja de teclas. Misma posición y código que el visor; S4/S5 coordinan las gradas.

Línea punteada · relación de mando
Relaciona el mando con sus luces. No fija un cableado, conductores ni trayecto de ejecución.

Líneas grises · muro
Paredes del modelo como referencia para situar los puntos.

Figura beige · mueble o aparato
Huella de referencia; se conservan las posiciones del modelo.

DATOS Y CRITERIOS DEL PLANO

Iluminación general: 4 plafones PC / 11 otros
Cuadrado con X: plafón PC; círculo con X: otra luz general.

Luz de trabajo / ambiente: 3 referencias
Círculo con raya; incluye LED, apliques y apoyos.

Cajas de mandos: S7, S8, S9
S4/S5: coordinar el control de gradas desde ambos niveles.

Plano de tomacorrientes: E-03T
Consultar su mapa independiente; no se representan aquí sus símbolos.

Baño del patio: 2 × 12 W · 4000 K
Sellado para zona húmeda; por confirmar

Bodega: 2 × 12 W · 4000 K
Interior seco

NOTAS PARA REVISIÓN EN OBRA

Mismas tomas y mandos que en imágenes 3D. Alturas propuestas; dormitorio según distribución aplicada.

Líneas punteadas: relación de mando y recorrido conceptual; no son número de conductores.

Grupos C01-C12 funcionales: dividir por planta, cargas y protecciones en cálculo. Tablero y tierra pendientes.

Bajo Eternit: canalización y cajas fijadas a soporte definido, nunca a las planchas.

Las luces de gradas se asignan a PB o PA por cota: cada referencia aparece una sola vez.


PC: plafón cuadrado sobrepuesto. Modelo seco de referencia 28,5 × 28,5 × 2,8 cm, 24 W, 1800 lm, 0,583 kg; 100–240 V. Confirmar equipo y suministro.

Fijar herraje a perfil/refuerzo del cielo; no cargar sólo la placa. Revisar perfilería, anclaje y acceso al driver; no suspender del Eternit.

Baños: variante sellada IP44 mínimo; IP65 si la zona lo exige. Potencia y formato menores orientativos; modelo y protección por elegir.

Plafón de referencia sin dimmer. LED indirecto y tarea separados. Cantidad propuesta; verificar iluminación con fotometría y medidas reales.

Revisión 10/11/2026 · 3cde0d4d | Modelo y propuesta de coordinación - comprobar en sitio

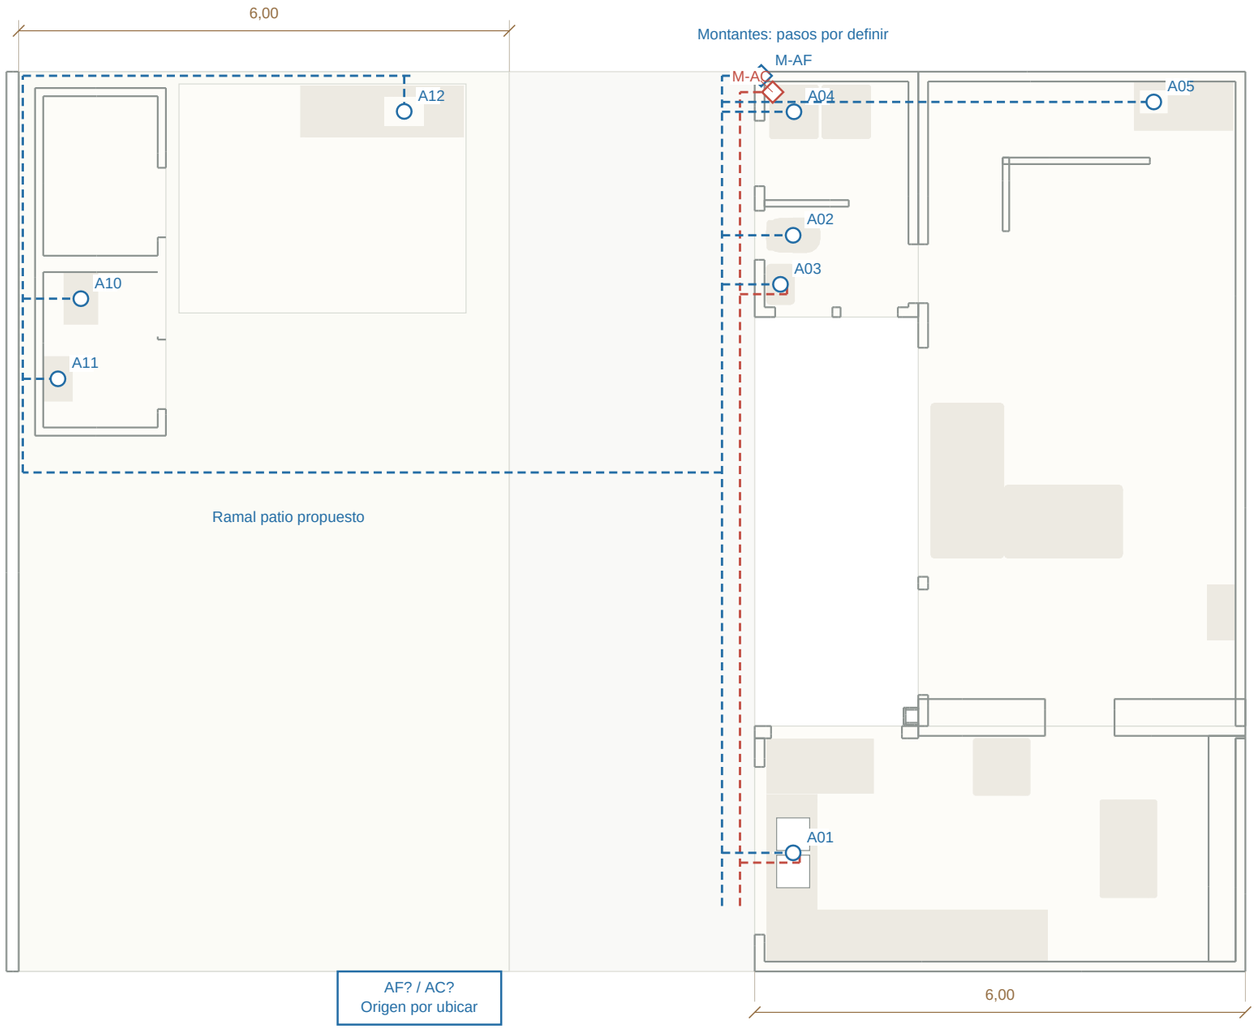

FRENTE ABAJO · RECORRIDOS PROPUESTOS

ESCALA 1:75 / A3 AL 100 %

Propuesta de coordinación; diseño pendiente.

Puntos de agua

8 aparatos

A01-A12: detalle en cuadro de instalaciones.

Agua caliente propuesta

A01, A03

Confirmar alcance y tipo de calentador.

M-AF / M-AC

Montantes propuestos

Coinciden entre H-01 y H-02; huecos no definidos.

Diámetros / presión

Por calcular

No comprar tubería por el grosor del dibujo.

NOTAS PARA REPLANTEO

Azul: agua fría. Rojo: reserva propuesta de agua caliente. Trazos punteados: recorridos por confirmar.


A01: fregadero doble bajo ventana; unir ambas pozas. Salidas ajustadas al equipo real.

Medidor y calentador no se ubican físicamente. Conexiones AF? / AC? son referencias de margen.

Medir presión y caudal; calcular diámetros, llaves y pruebas antes de instalar.

No ranurar vigas ni perforar el entrepiso o volado sin definir el paso con el responsable técnico.

Revisión 10/11/2026 · 3cde0d4d | Modelo y propuesta de coordinación - comprobar en sitio

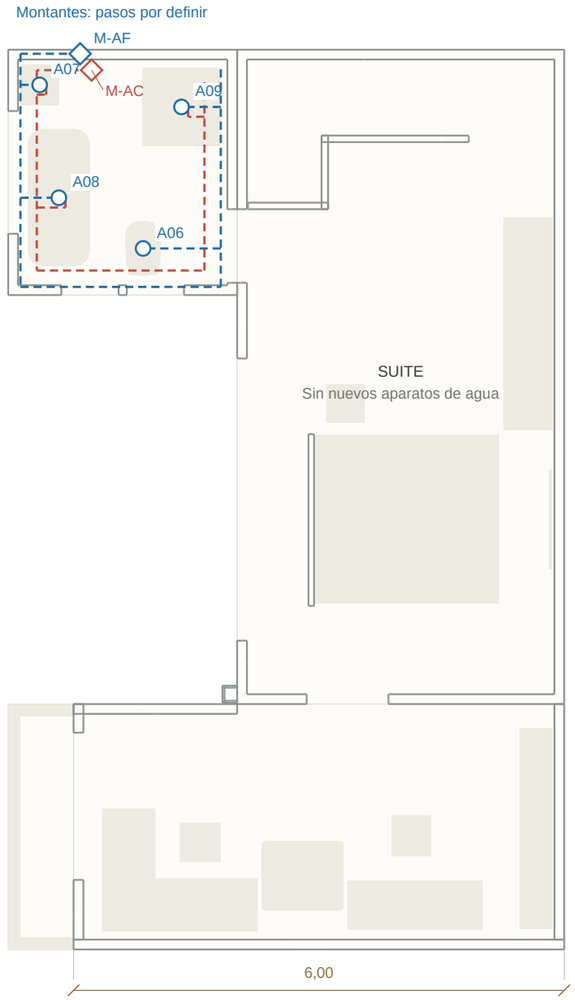

FRENTE ABAJO · RECORRIDOS PROPUESTOS

ESCALA 1:75 / A3 AL 100 %

Propuesta de coordinación; diseño pendiente.

Puntos de agua

4 aparatos

A01-A12: detalle en cuadro de instalaciones.

Agua caliente propuesta

A07, A08, A09

Confirmar alcance y tipo de calentador.

M-AF / M-AC

Montantes propuestos

Coinciden entre H-01 y H-02; huecos no definidos.

Diámetros / presión

Por calcular

No comprar tubería por el grosor del dibujo.

NOTAS PARA REPLANTEO

Azul: agua fría. Rojo: reserva propuesta de agua caliente. Trazos punteados: recorridos por confirmar.


A01: fregadero doble bajo ventana; unir ambas pozas. Salidas ajustadas al equipo real.

Medidor y calentador no se ubican físicamente. Conexiones AF? / AC? son referencias de margen.

Medir presión y caudal; calcular diámetros, llaves y pruebas antes de instalar.

No ranurar vigas ni perforar el entrepiso o volado sin definir el paso con el responsable técnico.

Revisión 10/11/2026 · 3cde0d4d | Modelo y propuesta de coordinación - comprobar en sitio

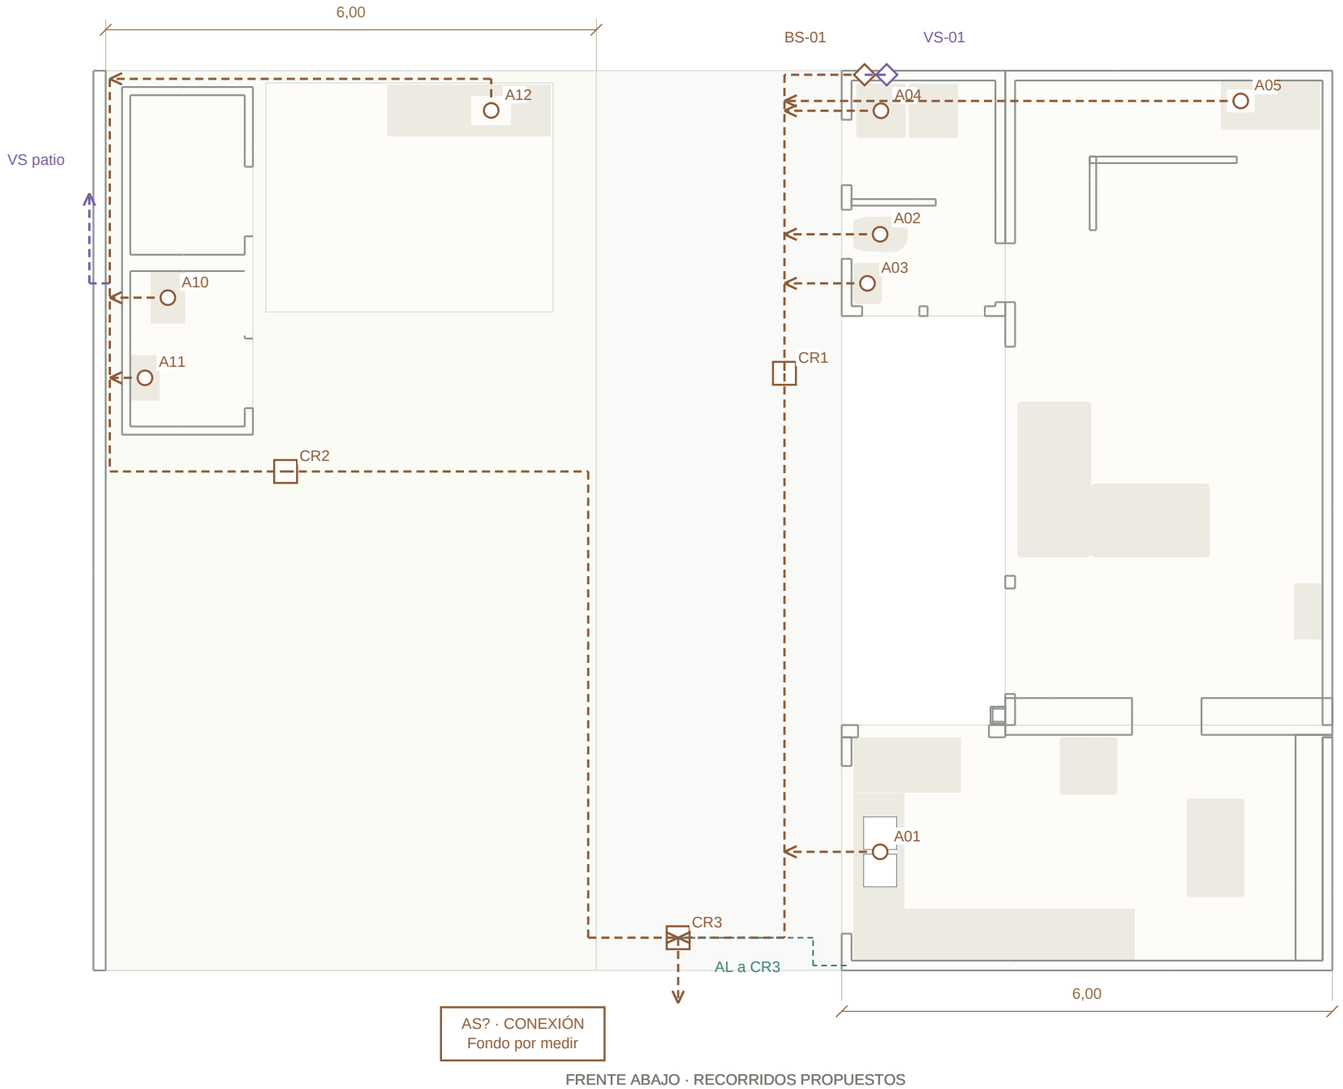

FRENTE ABAJO · RECORRIDOS PROPUESTOS

ESCALA 1:75 / A3 AL 100 %

Propuesta de coordinación; diseño pendiente.

Aparatos conectados

8 puntos sanitarios

Identificación A01-A12 igual a la red de agua.

BS-01 / VS-01

Bajante / ventilación

Trazo propuesto, sin perforación definida.

CR-01 / CR-02 / CR-03

CR3 indicada; CR1 / CR2 propuestas

CR3 conserva la posición del plano; levantar tamaño, cotas y red existente.

Diámetros / pendientes

Por calcular

Dependen de carga y cota real de descarga.

NOTAS PARA REPLANTEO

Marrón: aguas servidas. Violeta: ventilación sanitaria a resolver hasta cubierta.


Flechas indican destino conceptual; no fijan pendiente ni profundidad.

Salida sanitaria, cotas de fondo y red existente: levantar antes de zanjas o cortes.

Prever sifones y registros accesibles; dimensionar ramales, bajantes y ventilación.

Verde azulado: bajante del estudio por pared ciega y ramal bajo adoquín hasta CR3 indicada. Verificar cotas y admisión de lluvia en su red.

Revisión 10/11/2026 · 3cde0d4d | Modelo y propuesta de coordinación - comprobar en sitio

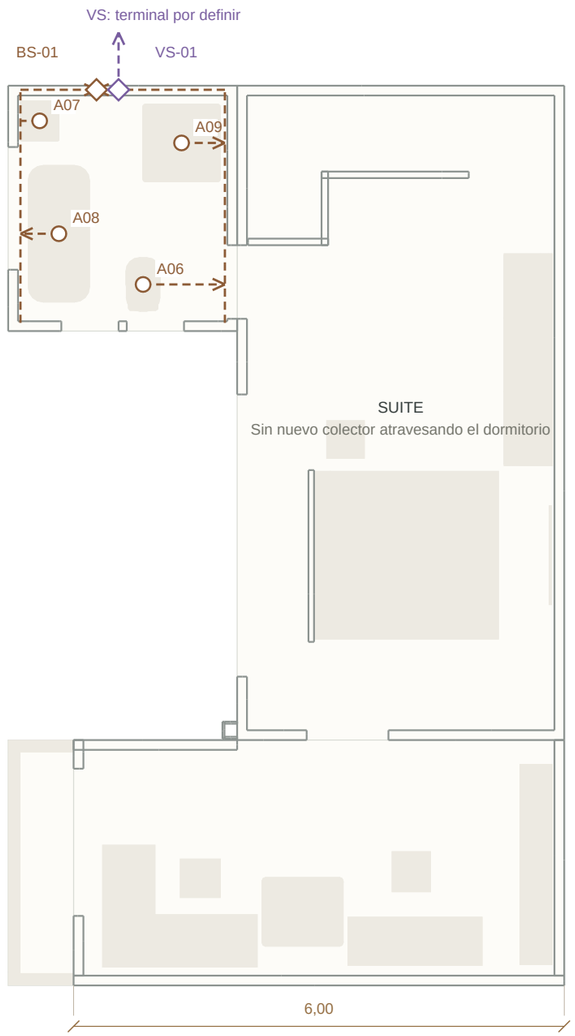

FRENTE ABAJO · RECORRIDOS PROPUESTOS

ESCALA 1:75 / A3 AL 100 %

Propuesta de coordinación; diseño pendiente.

Aparatos conectados

4 puntos sanitarios

Identificación A01-A12 igual a la red de agua.

BS-01 / VS-01

Bajante / ventilación

Trazo propuesto, sin perforación definida.

CR-01 / CR-02 / CR-03

Registros propuestos

En PB: accesos y niveles por comprobar.

Diámetros / pendientes

Por calcular

Dependen de carga y cota real de descarga.

NOTAS PARA REPLANTEO

Marrón: aguas servidas. Violeta: ventilación sanitaria a resolver hasta cubierta.

Flechas indican destino conceptual; no fijan pendiente ni profundidad.

Salida sanitaria, cotas de fondo y red existente: levantar antes de zanjas o cortes.

Prever sifones y registros accesibles; dimensionar ramales, bajantes y ventilación.

Las aguas lluvias tienen red separada en P-01; su destino final se comprueba con la red del predio.

Revisión 10/11/2026 · 3cde0d4d | Modelo y propuesta de coordinación - comprobar en sitio

ESPACIO	MEDIDAS m	ÁREA m²	ALTURA m
Sala, bloque completo	4,00 × 8,00	32,00	2,10
Cocina y comedor	6,00 × 3,00	18,00	2,10
Baño social con lavandería	2,00 × 3,00	6,00	2,10
Dormitorio, bloque completo	4,00 × 8,00	32,00	2,10
Baño principal	2,80 × 3,00	8,40	2,20
Estudio sobre cocina	6,00 × 3,00	18,00	2,10
Balcón del estudio	0,80 × 3,00	2,40	Pretil 1,10
Baño del patio, interior libre	1,40 × 1,90	2,66	3,50 - 3,58
Bodega del patio, interior libre	1,40 × 1,95	2,73	3,50 - 3,60
Área del asadero	3,51 × 2,80	9,83	3,33 - 3,51
Patio completo	6,00 × 11,00	66,00	Abierto

ESCALA 1:45 / A3 AL 100 %

No ajustar a página. Comprobar escala gráfica.

NOTAS PARA REPLANTEO

Tabla aportada el 08/11/2026. Bloques completos: el área incluye paredes, gradas o guardado según su huella.

Baño y bodega del patio: medidas interiores libres. Asadero: área 9,83 m² redondeada.

Estudio y dormitorio: piso +2,30 m, sin peldaño. Cocina y sala: piso 0,00 m. Alturas libres 2,10 m.

Cubierta del estudio: mismo plano, pendiente y sentido de planchas que la cubierta principal. Canal exterior al oeste.

Las alturas se miden desde el piso terminado hasta el cielo. Plafones sobresalen 2,8 cm bajo el cielo.

Replantear estructura de losa, acceso y cubierta con medidas reales antes de ejecutar.

Revisión 10/11/2026 · 3cde0d4d | Modelo y propuesta de coordinación - comprobar en sitio

HUECOS, PUERTAS Y PASOS - MEDIDAS DEL MODELO

IDENTIFICACIÓN	NIVEL	ANCHO m	ALTO m	COTA INFERIOR m
Acceso al baño principal	PA	0,90	2,10	2,30
Entrada 1,20 x 2,10 (altura por verificar)	PB	1,29	2,15	0,00
Sala · ventanal hacia el patio	PB	2,80	1,20	0,65
Social · frente, lado izquierdo	PB	0,70	0,60	1,22
Social · frente, lado derecho	PB	0,70	0,60	1,22
Principal · frente, lado izquierdo	PA	0,70	0,60	3,56
Principal · frente, lado derecho	PA	0,70	0,60	3,56
Principal · ventana hacia calle	PA	1,50	0,75	3,44
Dormitorio · ventanal hacia patio	PA	3,45	1,40	3,00
Cocina · ventana hacia calle	PB	2,05	0,85	1,10
Cocina · ventana de retorno	PB	1,60	0,85	1,10
Baño social (hoja 0,70 x 1,95)	PB	0,72	1,98	0,00
Acceso a nivel del estudio	PA	1,00	2,10	2,30
Paso cocina sin hoja · luz útil	PB	0,826	1,935	0,00
Estudio · corredera al balcón	PA	1,80	2,10	2,30
Baño social · ventana a calle	PB	0,60	0,75	1,10
Lavandería · ventana a calle	PB	0,80	0,75	1,10
Puerta baño patio (hoja 0,80 x 1,98)	Patio	0,85	2,05	-0,23
Puerta bodega (hoja 0,80 x 1,98)	Patio	0,85	2,05	-0,23
Ventana bodega	Patio	0,80	0,20	1,85
Ventana baño patio	Patio	0,75	0,60	Por medir

Cotas inferiores referidas al origen común del modelo. En PA no equivalen a antepecho desde su piso.

PENDIENTES DE MEDICIÓN

Replantear anchos libres, espesores de muro y posición real de cada hueco.

Medir niveles de piso, entrepiso, vigas y altura libre antes de definir las gradas.

Verificar hojas, marcos y giro real de puertas. Diferenciar hueco de obra y paso útil.

Cubiertas: definir ficha del producto, pendiente, traslapes, anclajes y drenajes.

Confirmar ubicación de agua, desagües, ventilación, luminarias, mandos y tomas.

Dimensionar volado, gradas, barandas, refuerzos y cimentaciones con el responsable técnico.

Entrada objetivo: 1,20 x 2,10 m, apertura exterior. Cielo de sala a 2,10 m aprox.: replantear altura y dintel. Descanso exterior y giro por medir.