
Revisión 05/11/2026 · 338f2d42 | Modelo y propuesta de coordinación - comprobar en sitio

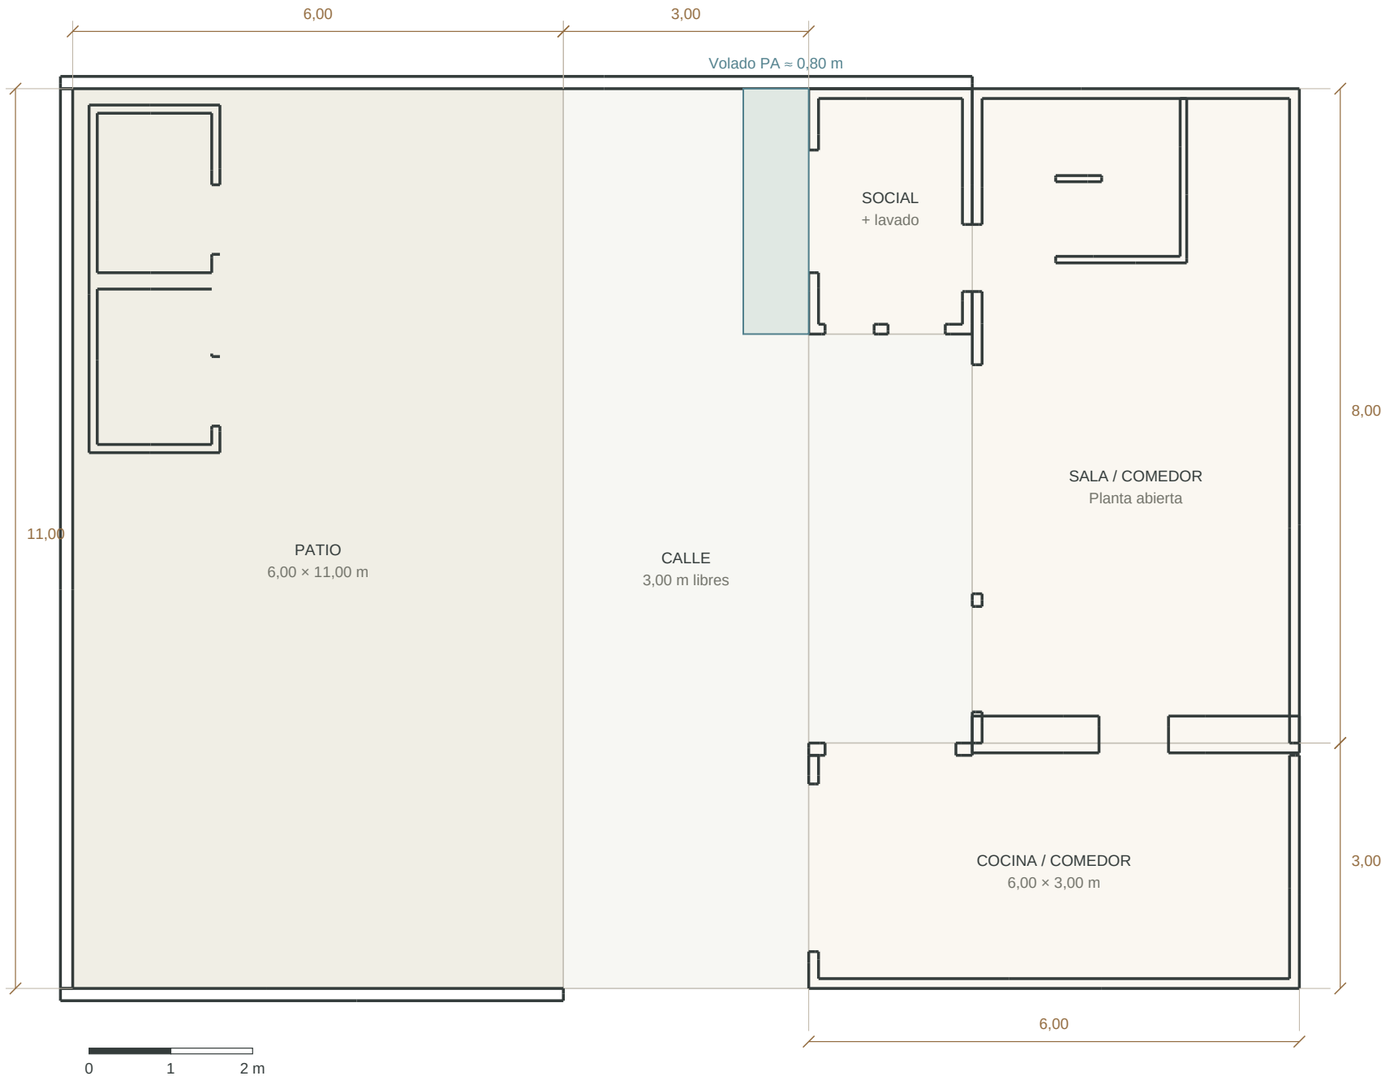

FRENTE / LLEGADA DESDE LA CALLE

ESCALA 1:75 / A3 AL 100 %

No ajustar a página. Comprobar escala gráfica.

Patio
6,00 × 11,00 m
Modelo · verificar en sitio

Calle de acceso
3,00 m de ancho
Confirmado por el usuario; comprobar replanteo.

Cocina / comedor
6,00 × 3,00 m
Modelo · verificar en sitio

Cuerpo de dos pisos
4,00 × 8,00 m
Modelo · verificar en sitio

Baño social / lavado
2,00 × 3,00 m
Modelo · verificar en sitio

Baño principal PA
2,80 × 3,00 m
Modelo · verificar en sitio

NOTAS PARA REPLANTEO

Conexión cocina/sala: adobe de 45,00 cm; retorno en bloque de 15,00 cm. Paso sin hoja, revestido en madera.

Lavandería dentro del baño social. El frente de 6 × 3 m es cocina y comedor.


Gradas cuadradas junto al baño: 13 subidas. Gypsum hasta el techo; puerta social hacia dentro del baño.

Paso cocina: luz útil aproximada 0,826 × 1,985 m; vano existente conservado. Replantear jambas y dintel.

PA: estudio sobre cocina y balcón lateral de 0,80 m; sin pilares nuevos dibujados en el paso de 3 m. Estructura y gálibo reales por verificar.

Piso flotante en sala, estudio y dormitorio. Cocina, baños y asadero conservan porcelanato beige.

Revisión 05/11/2026 · 338f2d42 | Modelo y propuesta de coordinación - comprobar en sitio

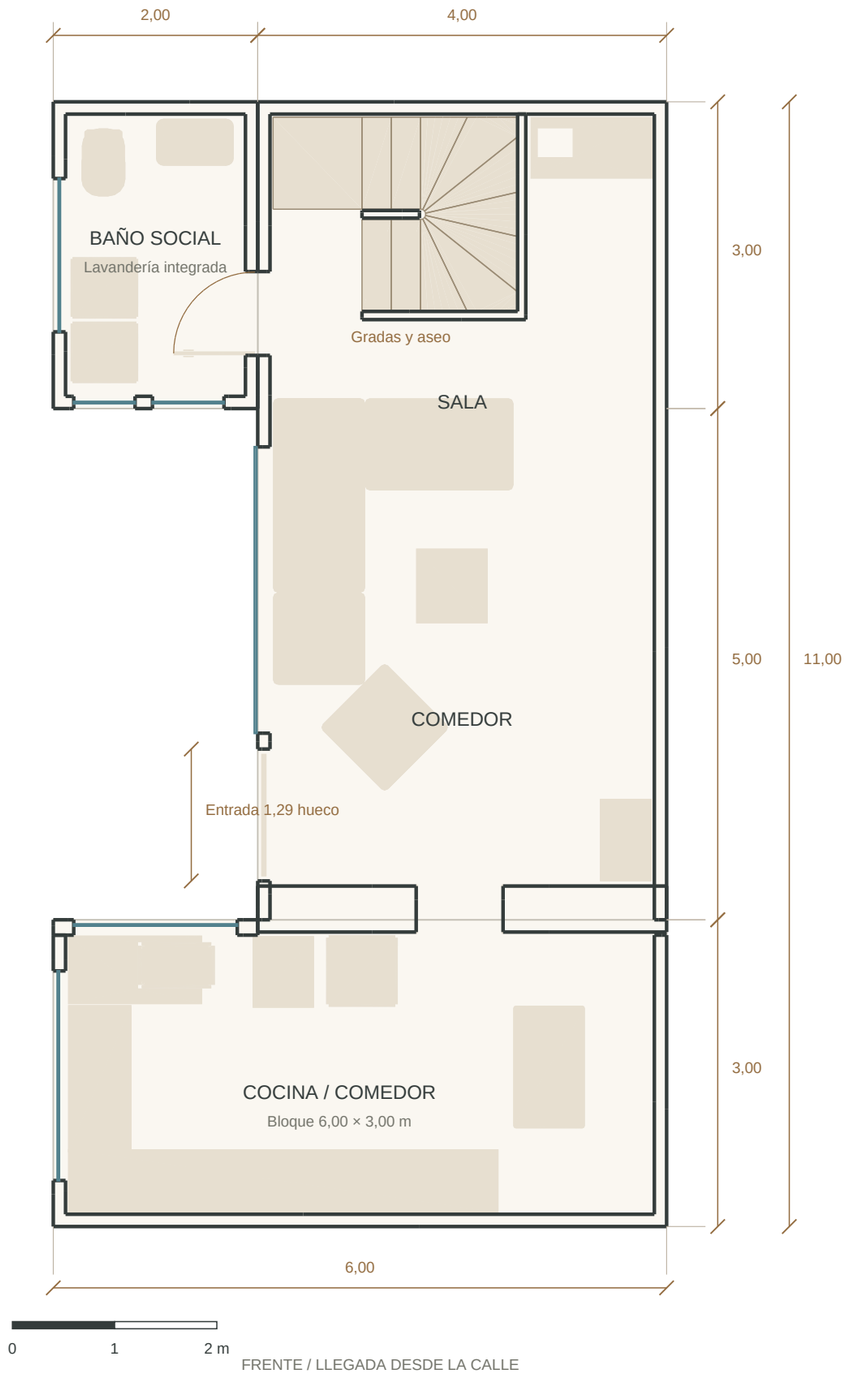

FRENTE / LLEGADA DESDE LA CALLE

ESCALA 1:60 / A3 AL 100 %

No ajustar a página. Comprobar escala gráfica.

Cocina / comedor

6,00 × 3,00 m

Dimensión exterior, sin antigua división de lavandería.

Sala / comedor abierto

4,00 × 8,00 m

Sin tabique entre sala y comedor.

Social con lavado

2,00 × 3,00 m

Lavadora y secadora lado a lado.

Piso cocina

-0,15 m

Desnivel respecto a sala; verificar nivel real.

Entrada de una hoja

1,20 × 2,10 m objetivo

Apertura exterior. Hueco 1,29 × 2,15 m por verificar: cielo interior aproximado de 2,10 m.

Altura sala

2,10 m aprox.

Cara inferior del cielo modelado; verificar vigas.

NOTAS PARA REPLANTEO

Conexión cocina/sala: adobe de 45,00 cm; retorno en bloque de 15,00 cm. Paso sin hoja, revestido en madera.

Lavandería dentro del baño social. El frente de 6 × 3 m es cocina y comedor.


Gradas cuadradas junto al baño: 13 subidas. Gypsum hasta el techo; puerta social hacia dentro del baño.

Paso cocina: luz útil aproximada 0,826 × 1,985 m; vano existente conservado. Replantear jambas y dintel.

PA: estudio sobre cocina y balcón lateral de 0,80 m; sin pilares nuevos dibujados en el paso de 3 m. Estructura y gálibo reales por verificar.

Piso flotante en sala, estudio y dormitorio. Cocina, baños y asadero conservan porcelanato beige.

Revisión 05/11/2026 · 338f2d42 | Modelo y propuesta de coordinación - comprobar en sitio

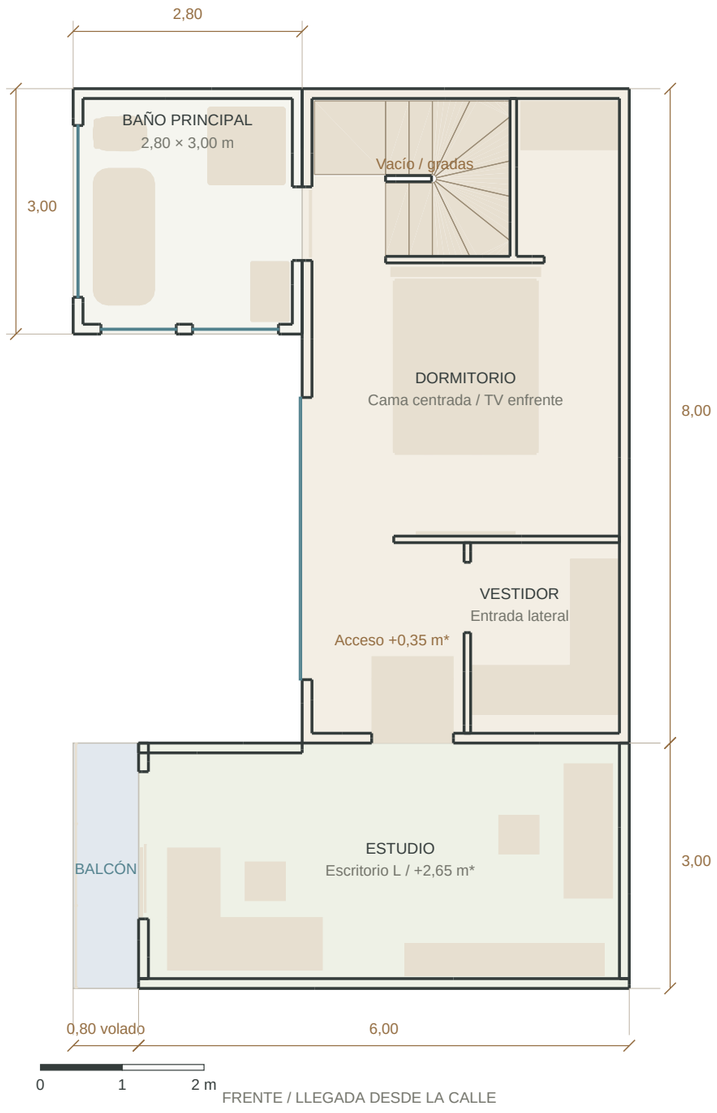

ESCALA 1:75 / A3 AL 100 %

No ajustar a página. Comprobar escala gráfica.

Dormitorio
4,00 × 8,00 m

Cama centrada y girada; vestidor de 1,90 × 2,40 m brutos.

Estudio sobre cocina
6,00 × 3,00 m / 18,00 m² brutos

Escritorio L 1,90 × 1,50 m y auxiliar 1,65 × 0,60 m.

Balcón lateral
0,80 × 3,00 m / 2,40 m² brutos

Proyección total; baranda y ancho útil pendientes.

Piso y acceso al estudio
+2,65 m / dos subidas de 17,5 cm

Desde dormitorio, llegada elevada y cielo local alto; no es acceso independiente.

Baño principal
2,80 × 3,00 m

Losa superior impermeabilizada; volado aproximado 0,80 m.

Vacío de escalera
3,81 m²

Hueco trasladado al lado del baño; no es superficie habitable.

NOTAS PARA REPLANTEO

Cama centrada y TV en pared lisa. Vestidor en L con acceso lateral de 86 cm; pasos conservados.


Dormitorio a +2,30 m y estudio a +2,65 m provisionales. Replantear acceso y altura libre del cielo local.

Losas, continuidad del volado de 80 cm, apoyos, baranda y cimentación requieren cálculo. El paso inferior de 3 m se conserva gráficamente.

Estudio: lateral al patio cerrado por adosamiento; luz natural desde balcón y ventilación por definir.

Dormitorio y estudio con piso flotante oscuro; baño con porcelanato. Acabados y espesores finales por elegir.

Revisión 05/11/2026 · 338f2d42 | Modelo y propuesta de coordinación - comprobar en sitio

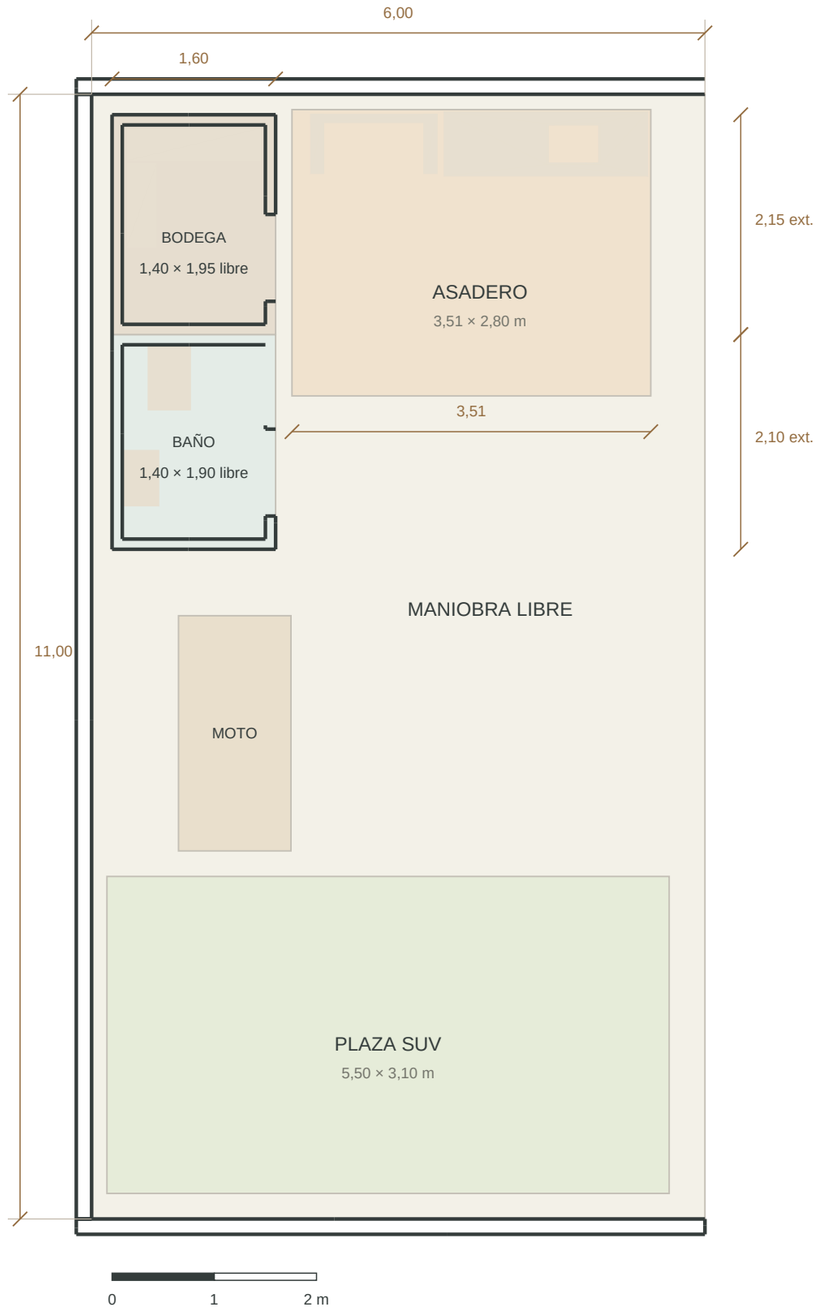

FRENTE / LLEGADA DESDE LA CALLE

ESCALA 1:60 / A3 AL 100 %

No ajustar a página. Comprobar escala gráfica.

Terreno patio
6,00 × 11,00 m
66 m²; las reservas interiores no se suman otra vez.

Servicios exterior
1,60 × 4,25 m
Modelo · verificar en sitio

Baño libre
1,40 × 1,90 m
Libre modelado; medir antes de levantar muros.

Bodega libre
1,40 × 1,95 m
Modelo · verificar en sitio

Asadero
3,51 × 2,80 m
Modelo · verificar en sitio

SUV / moto
5,50 × 3,10 / 1,10 × 2,30 m
Reservas de parqueo; mantener libre el giro.

NOTAS PARA REPLANTEO

Baño y asadero con porcelanato beige. Bodega con adoquín del patio.

Ventana de baño patio ampliada a 0,75 × 0,60 m, vidrio de privacidad.


Una sola cubierta en L para moto, baño, bodega y asadero.

Ventilación, agua, desagües y separación de chimenea por definir en sitio.

E-01 · Electricidad · planta baja

CASA LALES · MAPA COMPLETO · ESCALA 1:40 · IMPRIMIR AL 100 %

Revisión 05/11/2026 · 338f2d42

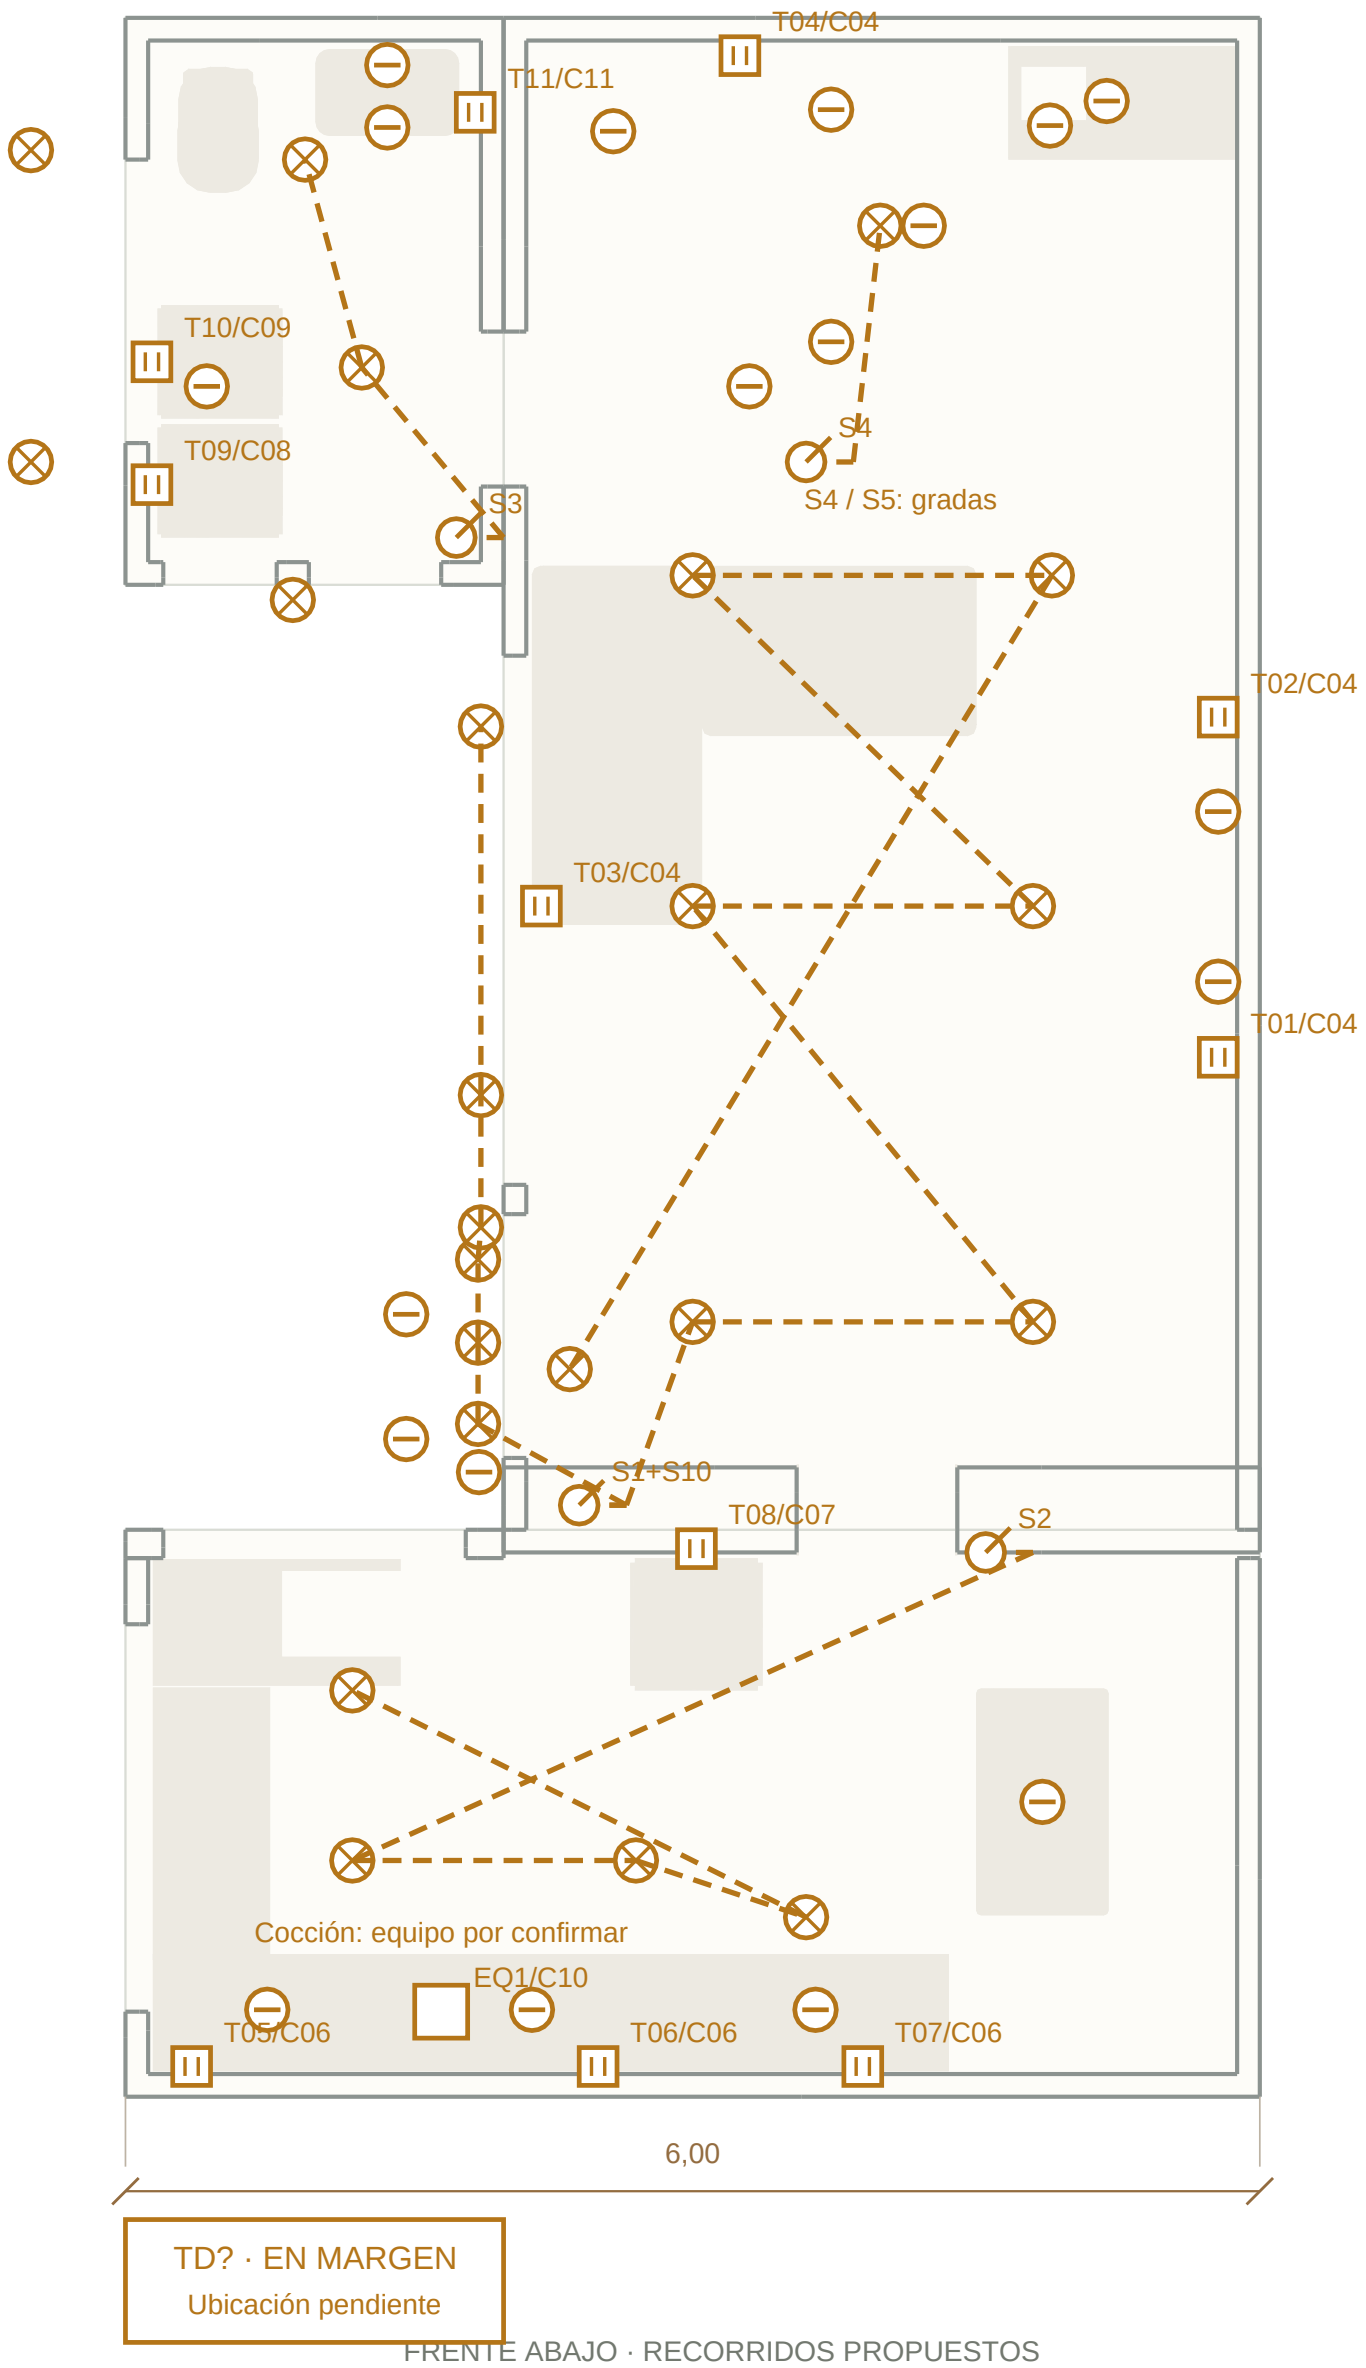

FRENTE ABAJO · RECORRIDOS PROPUESTOS

Simbología y notas en la hoja siguiente.

EXPLICACIÓN · E-01

Electricidad · planta baja

Casa Lales · Revisión 05/11/2026 · 338f2d42

QUÉ SIGNIFICA CADA FIGURA



Círculo con X · luz general

Punto de iluminación general: foco o plafón que ilumina el ambiente.



Círculo con raya · luz de apoyo

Luz de trabajo o ambiente: aplique, tira LED o apoyo de espejo, mueble o escalón.



Círculo con trazo inclinado · S

Interruptor o teclas de encendido. S1+S10 comparte caja; S4/S5 controla gradas desde ambos niveles.



Cuadrado con dos rayas · T

Tomacorriente propuesto. T09/C08 significa toma T09 del grupo C08.



Cuadrado vacío · EQ

Conexión de equipo: EQ1/C10 corresponde a cocción; alimentación por definir.

Línea punteada · mando

Relaciona un mando con sus luces. Es conceptual; no indica cableado ni número de hilos.



Rectángulo TD? · tablero

Tablero eléctrico sin ubicación confirmada. Se dibuja al margen, no en un sitio de obra.



Líneas grises · muro

Contorno de las paredes del modelo; sirve para ubicar los puntos.



Figura beige · mueble o aparato

Huella de muebles y equipos como referencia para orientar las instalaciones.



C01-C12 · grupo eléctrico

Identificador del grupo eléctrico propuesto; no indica amperaje ni cantidad de cables.

DATOS Y CRITERIOS DEL PLANO

Luz general del modelo: 23 puntos

Círculo con cruz. Los puntos del visor no equivalen siempre a luminarias comerciales.

Apoyo / trabajo: 19 referencias

Círculo con barra; LED y apliques del modelo.

Tomas propuestas: 11 puntos

T01-T21: ubicación y altura por revisar.

Mandos propuestos: S1, S2, S3, S4, S10

S4 / S5: prever control de gradas desde ambos niveles.

NOTAS PARA REVISIÓN EN OBRA

Luminarias desde el modelo; tomas y mandos son nuevos puntos propuestos.

Líneas punteadas: relación de mando y recorrido conceptual; no son número de conductores.

Tablero, suministro, cargas, calibres, protecciones y tierra: levantar y calcular antes de tender.


Bajo Eternit: canalización y cajas fijadas a soporte definido, nunca a las planchas.

Verificar zonas húmedas y protección de tomas del baño.

E-02 · Electricidad · planta alta

CASA LALES · MAPA COMPLETO · ESCALA 1:40 · IMPRIMIR AL 100 %

Revisión 05/11/2026 · 338f2d42

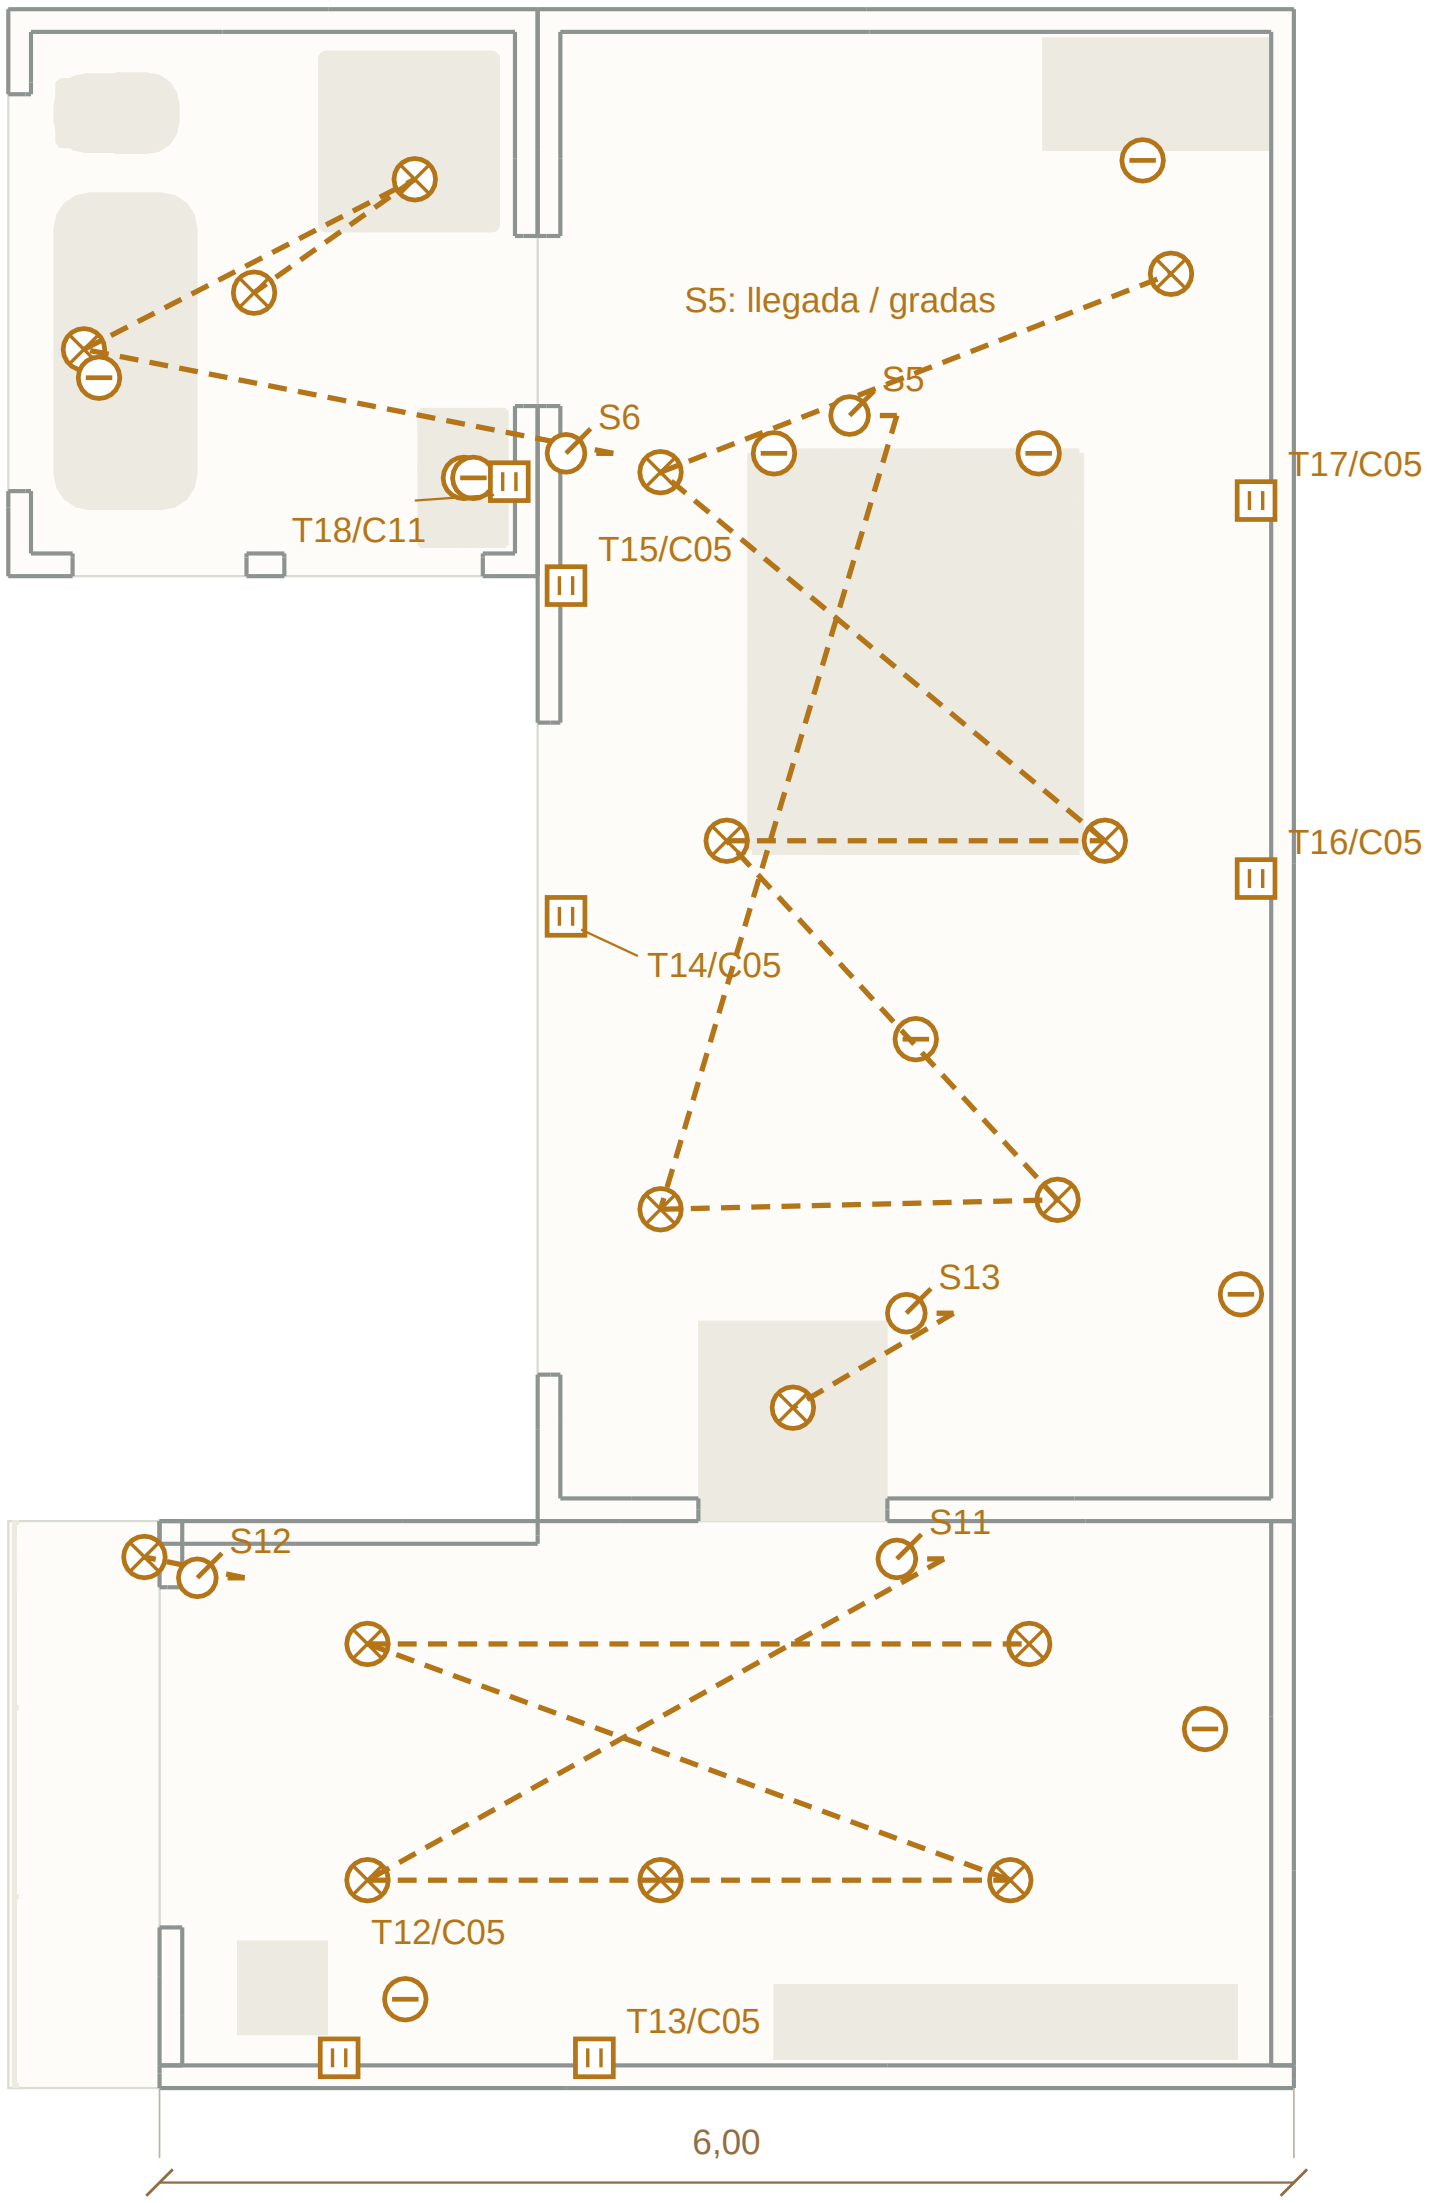

FRENTE ABAJO · RECORRIDOS PROPUESTOS

Simbología y notas en la hoja siguiente.

EXPLICACIÓN · E-02

Electricidad · planta alta

Casa Lales · Revisión 05/11/2026 · 338f2d42

QUÉ SIGNIFICA CADA FIGURA



Círculo con X · luz general

Punto de iluminación general: foco o plafón que ilumina el ambiente.



Círculo con raya · luz de apoyo

Luz de trabajo o ambiente: aplique, tira LED o apoyo de espejo, mueble o escalón.



Círculo con trazo inclinado · S

S5: llegada/gradas; S6: baño; S11: estudio; S12: balcón; S13: acceso elevado. Coordinar las gradas con S4 en PB.



Cuadrado con dos rayas · T

T12 y T13 del grupo C05 se trasladan a los dos puestos del estudio. Alturas, cargas y protección por definir.

Línea punteada · mando

Relaciona un mando con sus luces. Es conceptual; no indica cableado ni número de hilos.



Líneas grises · muro

Contorno de las paredes del modelo; sirve para ubicar los puntos.



Figura beige · mueble o aparato

Huella de muebles y equipos como referencia para orientar las instalaciones.

C01

C01-C12 · grupo eléctrico

Identificador del grupo eléctrico propuesto; no indica amperaje ni cantidad de cables.

DATOS Y CRITERIOS DEL PLANO

Luz general del modelo: 16 puntos

Círculo con cruz. Los puntos del visor no equivalen siempre a luminarias comerciales.

Apoyo / trabajo: 10 referencias

Círculo con barra; LED y apliques del modelo.

Tomas propuestas: 7 puntos

T01-T21: ubicación y altura por revisar.

Mandos propuestos: S5, S6, S11, S12, S13

S4 / S5: prever control de gradas desde ambos niveles.

NOTAS PARA REVISIÓN EN OBRA

Luminarias desde el modelo; tomas y mandos son nuevos puntos propuestos.

Líneas punteadas: relación de mando y recorrido conceptual; no son número de conductores.

Tablero, suministro, cargas, calibres, protecciones y tierra: levantar y calcular antes de tender.


Bajo Eternit: canalización y cajas fijadas a soporte definido, nunca a las planchas.

Verificar zonas húmedas y protección de tomas del baño.

E-03 · Electricidad · patio

CASA LALES · MAPA COMPLETO · ESCALA 1:40 · IMPRIMIR AL 100 %

Revisión 05/11/2026 · 338f2d42

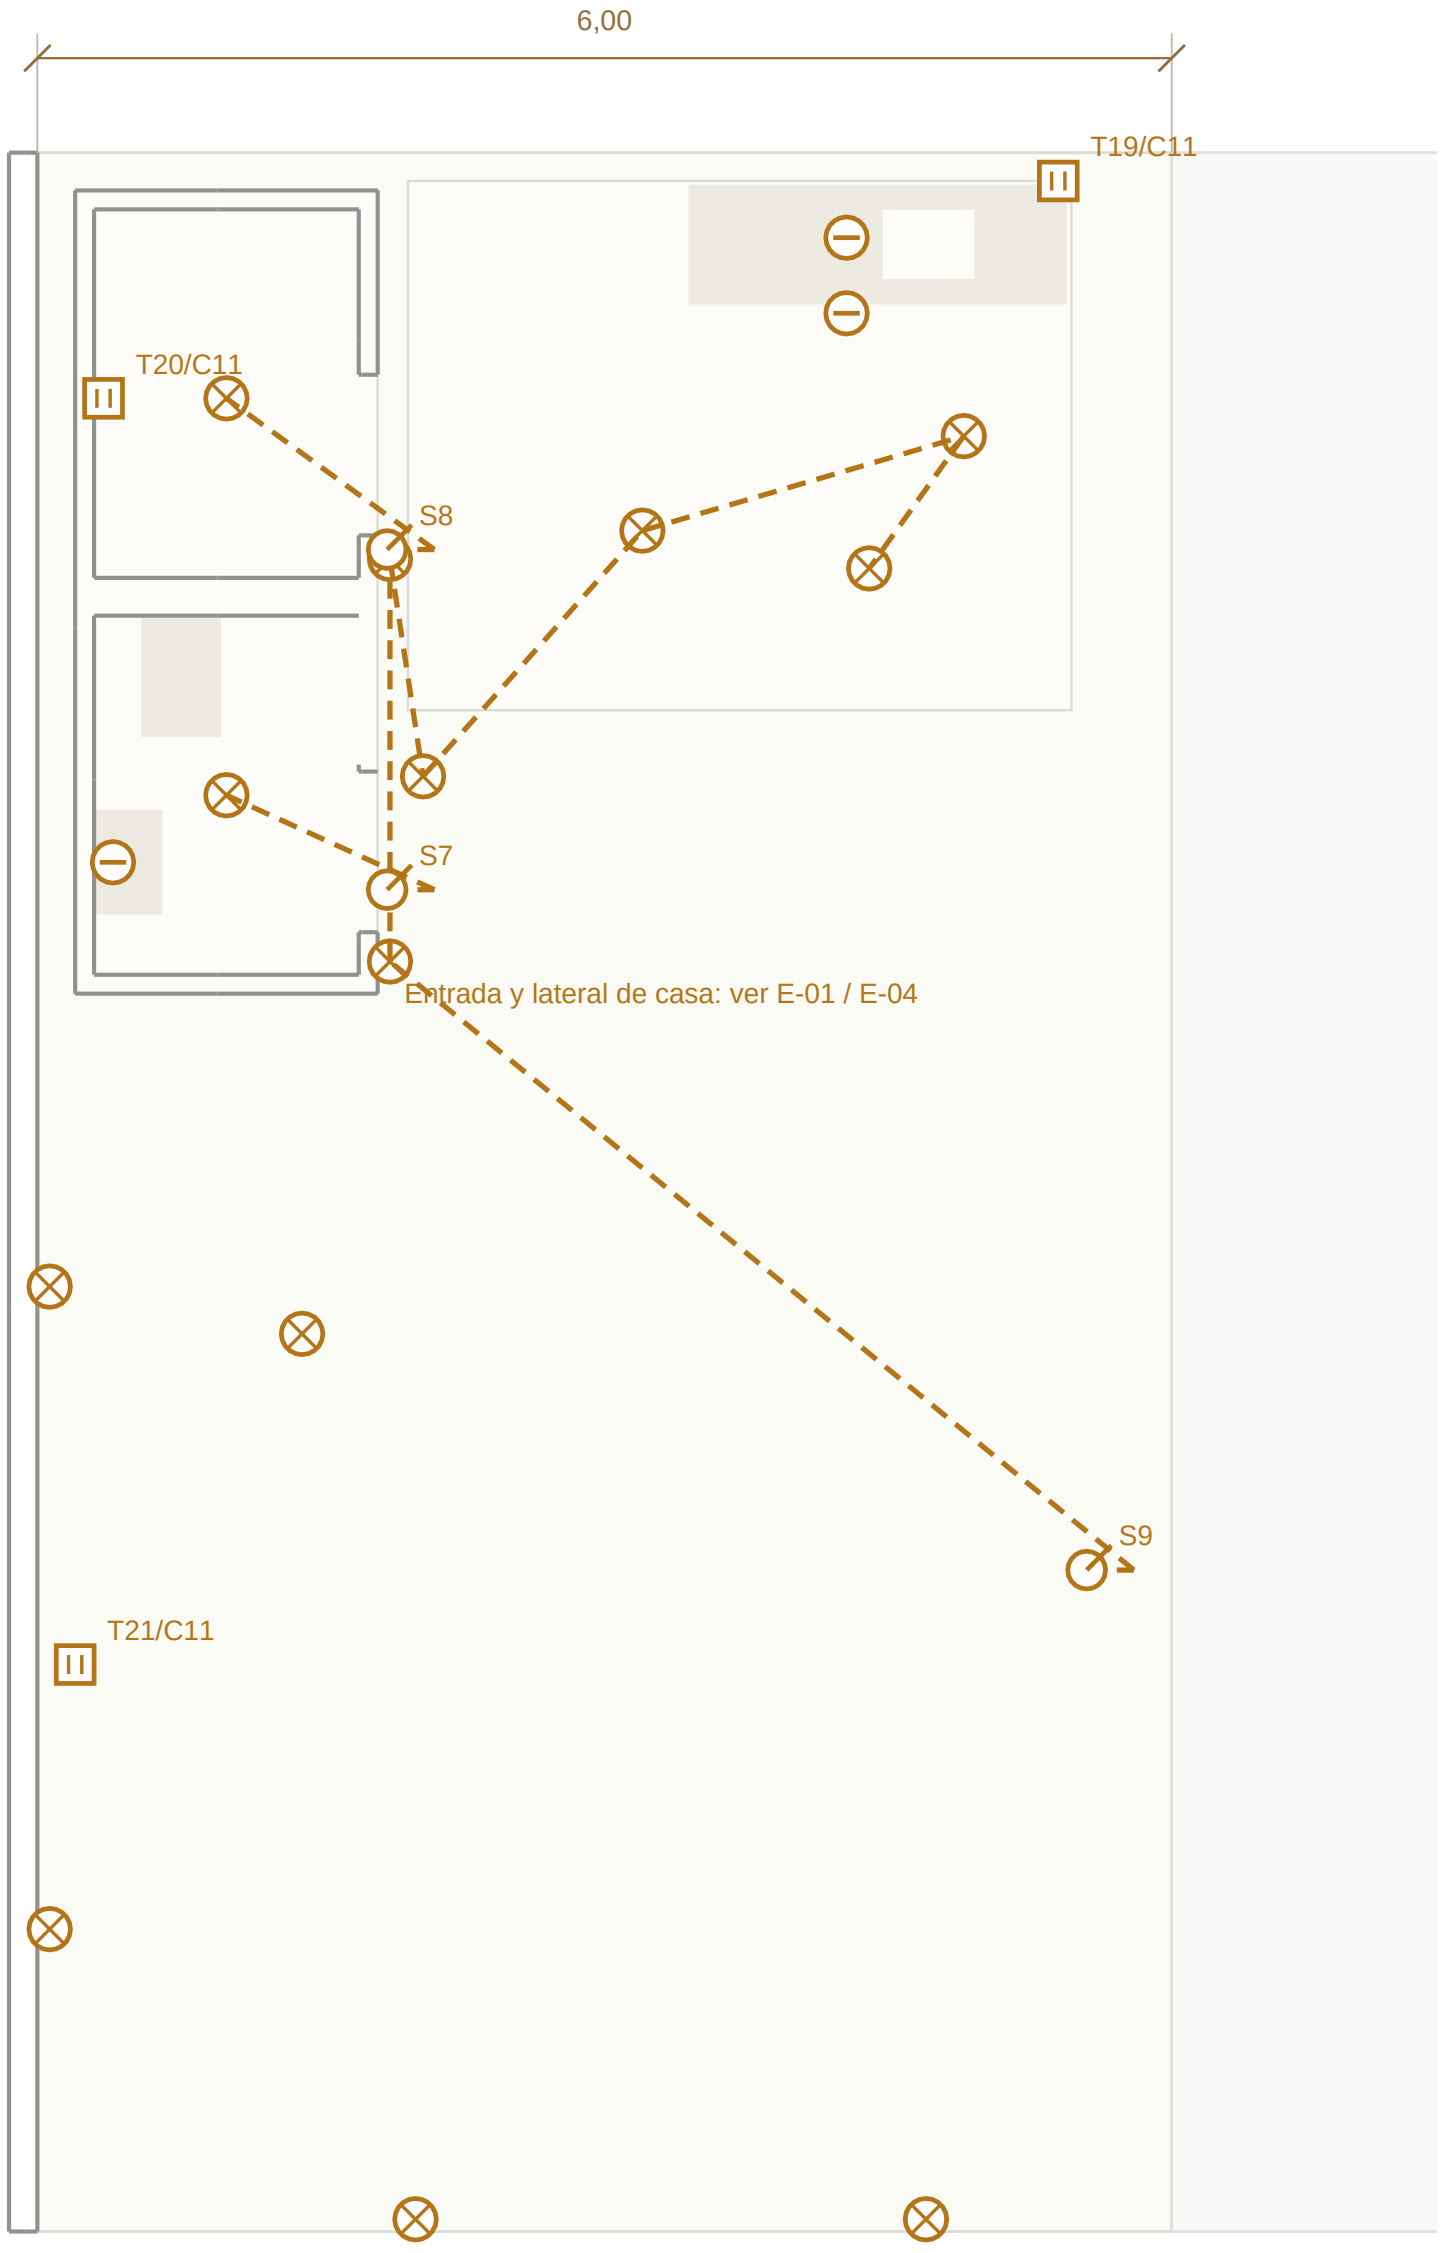

FRENTE ABAJO · RECORRIDOS PROPUESTOS

Simbología y notas en la hoja siguiente.

EXPLICACIÓN · E-03

Electricidad · patio

Casa Lales · Revisión 05/11/2026 · 338f2d42

QUÉ SIGNIFICA CADA FIGURA



Círculo con X · luz general

Punto de iluminación general: foco o plafón que ilumina el ambiente.



Círculo con raya · luz de apoyo

Luz de trabajo o ambiente: aplique, tira LED o apoyo de espejo, mueble o escalón.



Círculo con trazo inclinado · S

Interruptor propuesto: S7 para el baño, S8 para la bodega y S9 para la zona de patio indicada.



Cuadrado con dos rayas · T

Tomacorriente propuesto. T19/C11 significa toma T19 del grupo C11.

Línea punteada · mando

Relaciona un mando con sus luces. Es conceptual; no indica cableado ni número de hilos.



Líneas grises · muro

Contorno de las paredes del modelo; sirve para ubicar los puntos.



Figura beige · mueble o aparato

Huella de muebles y equipos como referencia para orientar las instalaciones.

C01

C01-C12 · grupo eléctrico

Identificador del grupo eléctrico propuesto; no indica amperaje ni cantidad de cables.

DATOS Y CRITERIOS DEL PLANO

Luz general del modelo: 13 puntos

Círculo con cruz. Los puntos del visor no equivalen siempre a luminarias comerciales.

Apoyo / trabajo: 3 referencias

Círculo con barra; LED y apliques del modelo.

Tomas propuestas: 3 puntos

T01-T21: ubicación y altura por revisar.

Mandos propuestos: S7, S8, S9

S4 / S5: prever control de gradas desde ambos niveles.

NOTAS PARA REVISIÓN EN OBRA

Luminarias desde el modelo; tomas y mandos son nuevos puntos propuestos.


Líneas punteadas: relación de mando y recorrido conceptual; no son número de conductores.

Tablero, suministro, cargas, calibres, protecciones y tierra: levantar y calcular antes de tender.

Bajo Eternit: canalización y cajas fijadas a soporte definido, nunca a las planchas.

Prever equipos aptos para intemperie y maniobra despejada.

Revisión 05/11/2026 · 338f2d42 | Modelo y propuesta de coordinación - comprobar en sitio

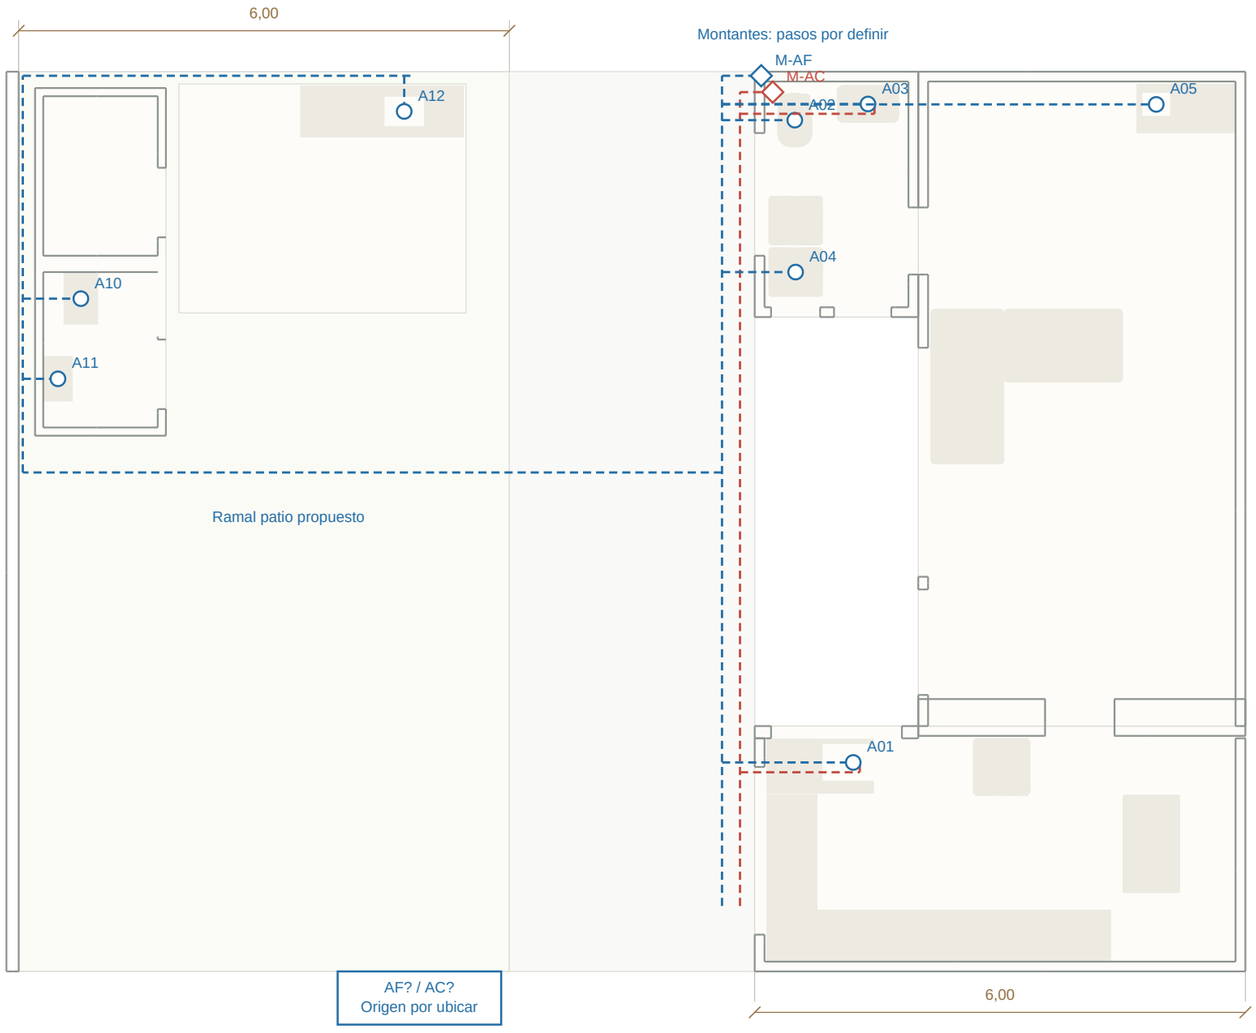

FRENTE ABAJO · RECORRIDOS PROPUESTOS

ESCALA 1:75 / A3 AL 100 %

Propuesta de coordinación; diseño pendiente.

Puntos de agua

8 aparatos

A01-A12: detalle en cuadro de instalaciones.

Agua caliente propuesta

A01, A03

Confirmar alcance y tipo de calentador.

M-AF / M-AC

Montantes propuestos

Coinciden entre H-01 y H-02; huecos no definidos.

Diámetros / presión

Por calcular

No comprar tubería por el grosor del dibujo.

NOTAS PARA REPLANTEO

Azul: agua fría. Rojo: reserva propuesta de agua caliente. Trazos punteados: recorridos por confirmar.


A01-A12 identifican aparatos del modelo; la salida exacta se ajusta al equipo real.

Medidor y calentador no se ubican físicamente. Conexiones AF? / AC? son referencias de margen.

Medir presión y caudal; calcular diámetros, llaves y pruebas antes de instalar.

No ranurar vigas ni perforar el entrepiso o volado sin definir el paso con el responsable técnico.

Revisión 05/11/2026 · 338f2d42 | Modelo y propuesta de coordinación - comprobar en sitio

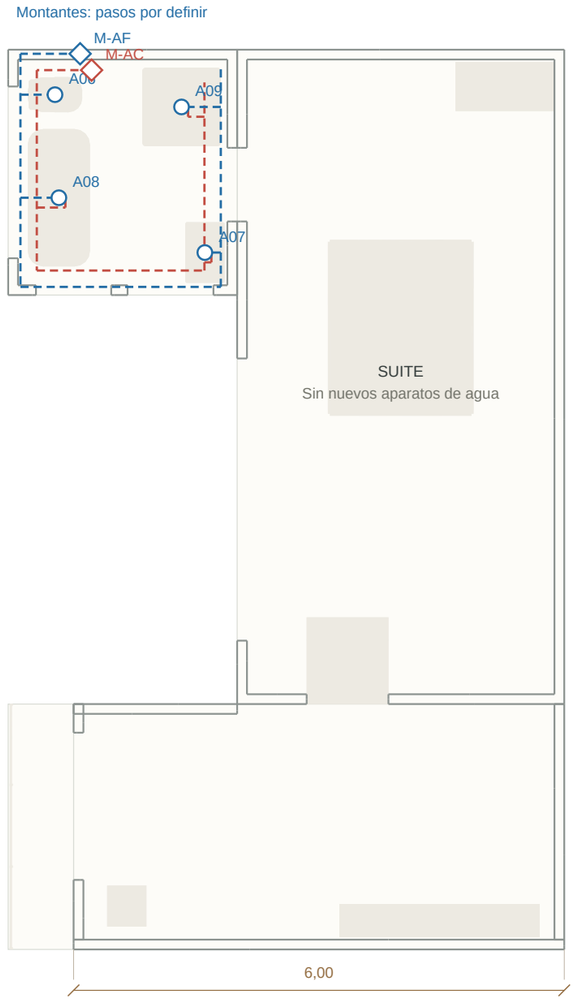

FRENTE ABAJO · RECORRIDOS PROPUESTOS

ESCALA 1:75 / A3 AL 100 %

Propuesta de coordinación; diseño pendiente.

Puntos de agua

4 aparatos

A01-A12: detalle en cuadro de instalaciones.

Agua caliente propuesta

A07, A08, A09

Confirmar alcance y tipo de calentador.

M-AF / M-AC

Montantes propuestos

Coinciden entre H-01 y H-02; huecos no definidos.

Diámetros / presión

Por calcular

No comprar tubería por el grosor del dibujo.

NOTAS PARA REPLANTEO

Azul: agua fría. Rojo: reserva propuesta de agua caliente. Trazos punteados: recorridos por confirmar.


A01-A12 identifican aparatos del modelo; la salida exacta se ajusta al equipo real.

Medidor y calentador no se ubican físicamente. Conexiones AF? / AC? son referencias de margen.

Medir presión y caudal; calcular diámetros, llaves y pruebas antes de instalar.

No ranurar vigas ni perforar el entrepiso o volado sin definir el paso con el responsable técnico.

Revisión 05/11/2026 · 338f2d42 | Modelo y propuesta de coordinación - comprobar en sitio

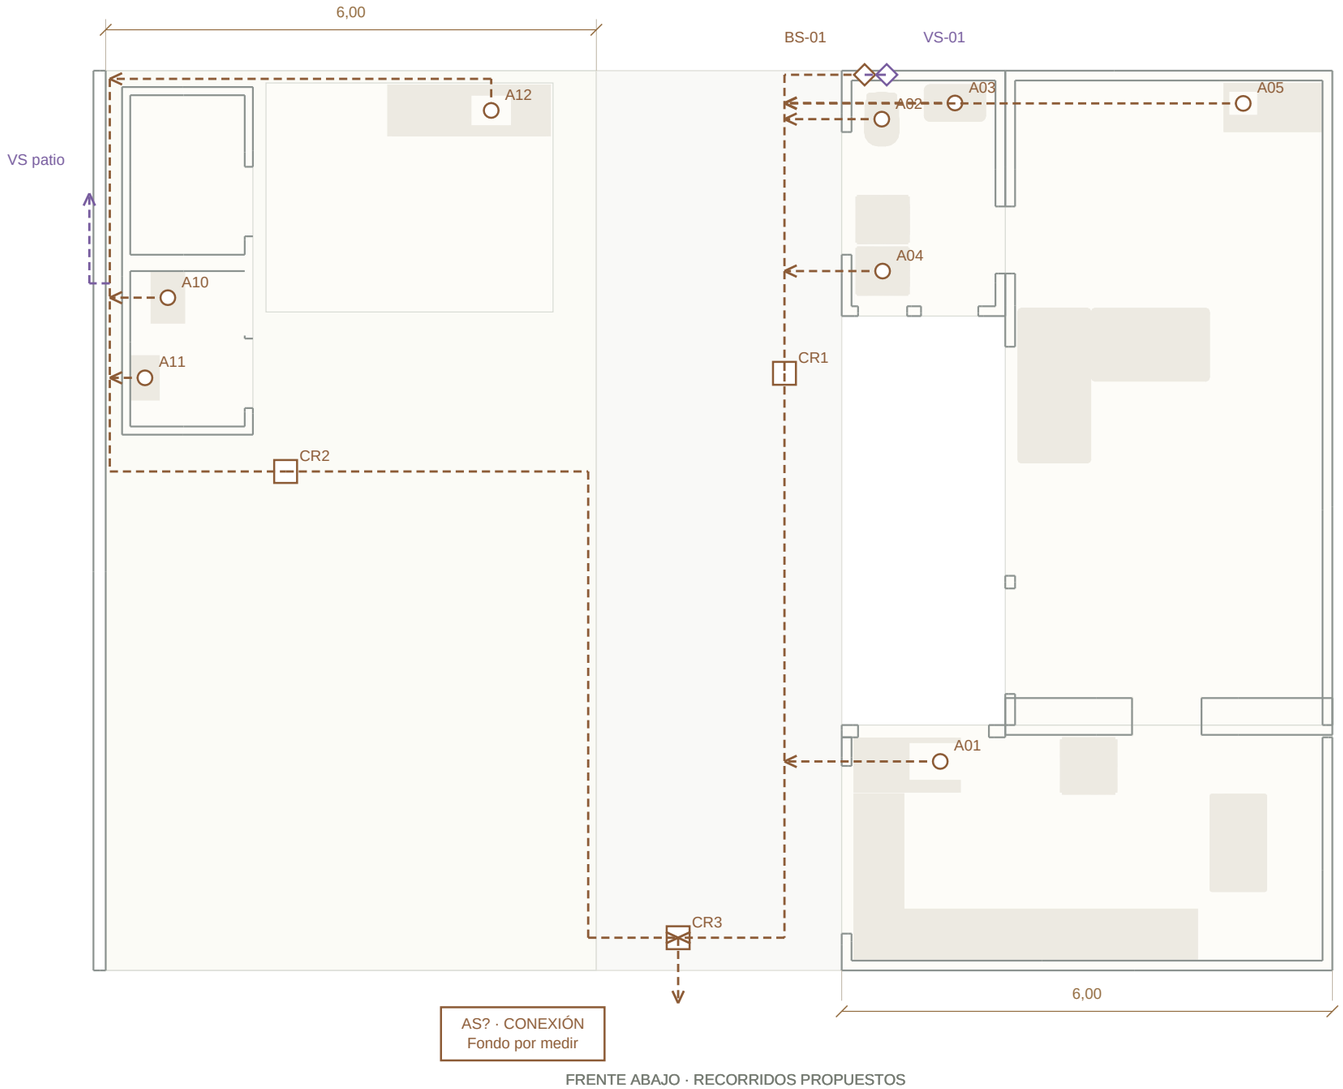

FRENTE ABAJO · RECORRIDOS PROPUESTOS

ESCALA 1:75 / A3 AL 100 %

Propuesta de coordinación; diseño pendiente.

Aparatos conectados

8 puntos sanitarios

Identificación A01-A12 igual a la red de agua.

BS-01 / VS-01

Bajante / ventilación

Trazo propuesto, sin perforación definida.

CR-01 / CR-02 / CR-03

Registros propuestos

En PB: accesos y niveles por comprobar.

Diámetros / pendientes

Por calcular

Dependen de carga y cota real de descarga.

NOTAS PARA REPLANTEO

Marrón: aguas servidas. Violeta: ventilación sanitaria a resolver hasta cubierta.


Flechas indican destino conceptual; no fijan pendiente ni profundidad.

Salida sanitaria, cotas de fondo y red existente: levantar antes de zanjas o cortes.

Prever sifones y registros accesibles; dimensionar ramales, bajantes y ventilación.

Las aguas lluvias tienen red separada en P-01; su destino final se comprueba con la red del predio.

Revisión 05/11/2026 · 338f2d42 | Modelo y propuesta de coordinación - comprobar en sitio

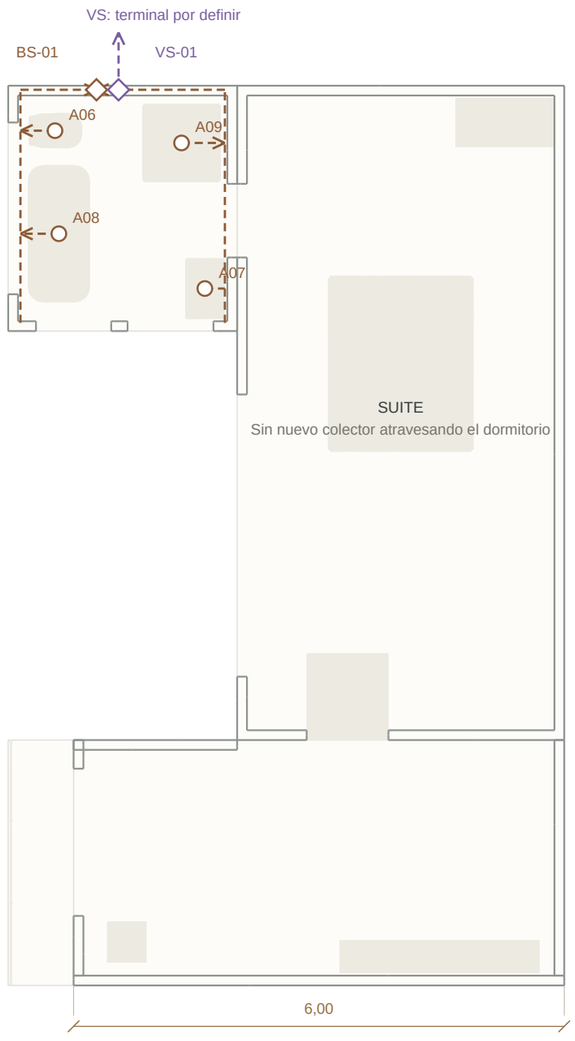

FRENTE ABAJO · RECORRIDOS PROPUESTOS

ESCALA 1:75 / A3 AL 100 %

Propuesta de coordinación; diseño pendiente.

Aparatos conectados

4 puntos sanitarios

Identificación A01-A12 igual a la red de agua.

BS-01 / VS-01

Bajante / ventilación

Trazo propuesto, sin perforación definida.

CR-01 / CR-02 / CR-03

Registros propuestos

En PB: accesos y niveles por comprobar.

Diámetros / pendientes

Por calcular

Dependen de carga y cota real de descarga.

NOTAS PARA REPLANTEO

Marrón: aguas servidas. Violeta: ventilación sanitaria a resolver hasta cubierta.

Flechas indican destino conceptual; no fijan pendiente ni profundidad.

Salida sanitaria, cotas de fondo y red existente: levantar antes de zanjas o cortes.

Prever sifones y registros accesibles; dimensionar ramales, bajantes y ventilación.

Las aguas lluvias tienen red separada en P-01; su destino final se comprueba con la red del predio.

Revisión 05/11/2026 · 338f2d42 | Modelo y propuesta de coordinación - comprobar en sitio

HUECOS, PUERTAS Y PASOS - MEDIDAS DEL MODELO

IDENTIFICACIÓN	NIVEL	ANCHO m	ALTO m	COTA INFERIOR m
Acceso al baño principal	PA	0,90	2,10	2,30
Entrada 1,20 x 2,10 (altura por verificar)	PB	1,29	2,15	0,00
Sala · ventanal hacia el patio	PB	2,80	1,20	0,65
Social · frente, lado izquierdo	PB	0,60	0,57	1,22
Social · frente, lado derecho	PB	0,70	0,57	1,22
Principal · frente, lado izquierdo	PA	0,92	0,75	3,47
Principal · frente, lado derecho	PA	1,05	0,75	3,47
Social · ventana hacia calle	PB	1,50	0,75	1,10
Principal · ventana hacia calle	PA	2,10	0,85	3,40
Dormitorio · ventanal hacia patio	PA	3,45	1,40	3,00
Cocina · ventana hacia calle	PB	2,05	1,20	0,95
Cocina · ventana de retorno	PB	1,60	1,20	0,95
Baño social (hoja 0,80 x 1,95)	PB	0,82	1,98	0,00
Acceso elevado al estudio	PA	1,00	2,14	2,65
Estudio · corredera al balcón	PA	1,80	2,14	2,65
Paso cocina sin hoja · luz útil	PB	0,826	1,985	0,00
Puerta baño patio (hoja 0,80 x 1,98)	Patio	0,85	2,05	-0,23
Puerta bodega (hoja 0,80 x 1,98)	Patio	0,85	2,05	-0,23
Ventana bodega	Patio	0,80	0,20	1,85
Ventana baño patio	Patio	0,75	0,60	Por medir

Cotas inferiores referidas al origen común del modelo. En PA no equivalen a antepecho desde su piso.

PENDIENTES DE MEDICIÓN

Replantear anchos libres, espesores de muro y posición real de cada hueco.

Medir niveles de piso, entrepiso, vigas y altura libre antes de definir las gradas.

Verificar hojas, marcos y giro real de puertas. Diferenciar hueco de obra y paso útil.

Cubiertas: definir ficha del producto, pendiente, traslapes, anclajes y drenajes.

Confirmar ubicación de agua, desagües, ventilación, luminarias, mandos y tomas.

Dimensionar volado, gradas, barandas, refuerzos y cimentaciones con el responsable técnico.

Entrada objetivo: 1,20 x 2,10 m, apertura exterior. Cielo de sala a 2,10 m aprox.: replantear altura y dintel. Descanso exterior y giro por medir.