
# A-01 · Conjunto y medidas generales

CASA LALES · MAPA COMPLETO · ESCALA 1:60 · IMPRIMIR AL 100 %

Revisión 12/11/2026 · 2212a8f4

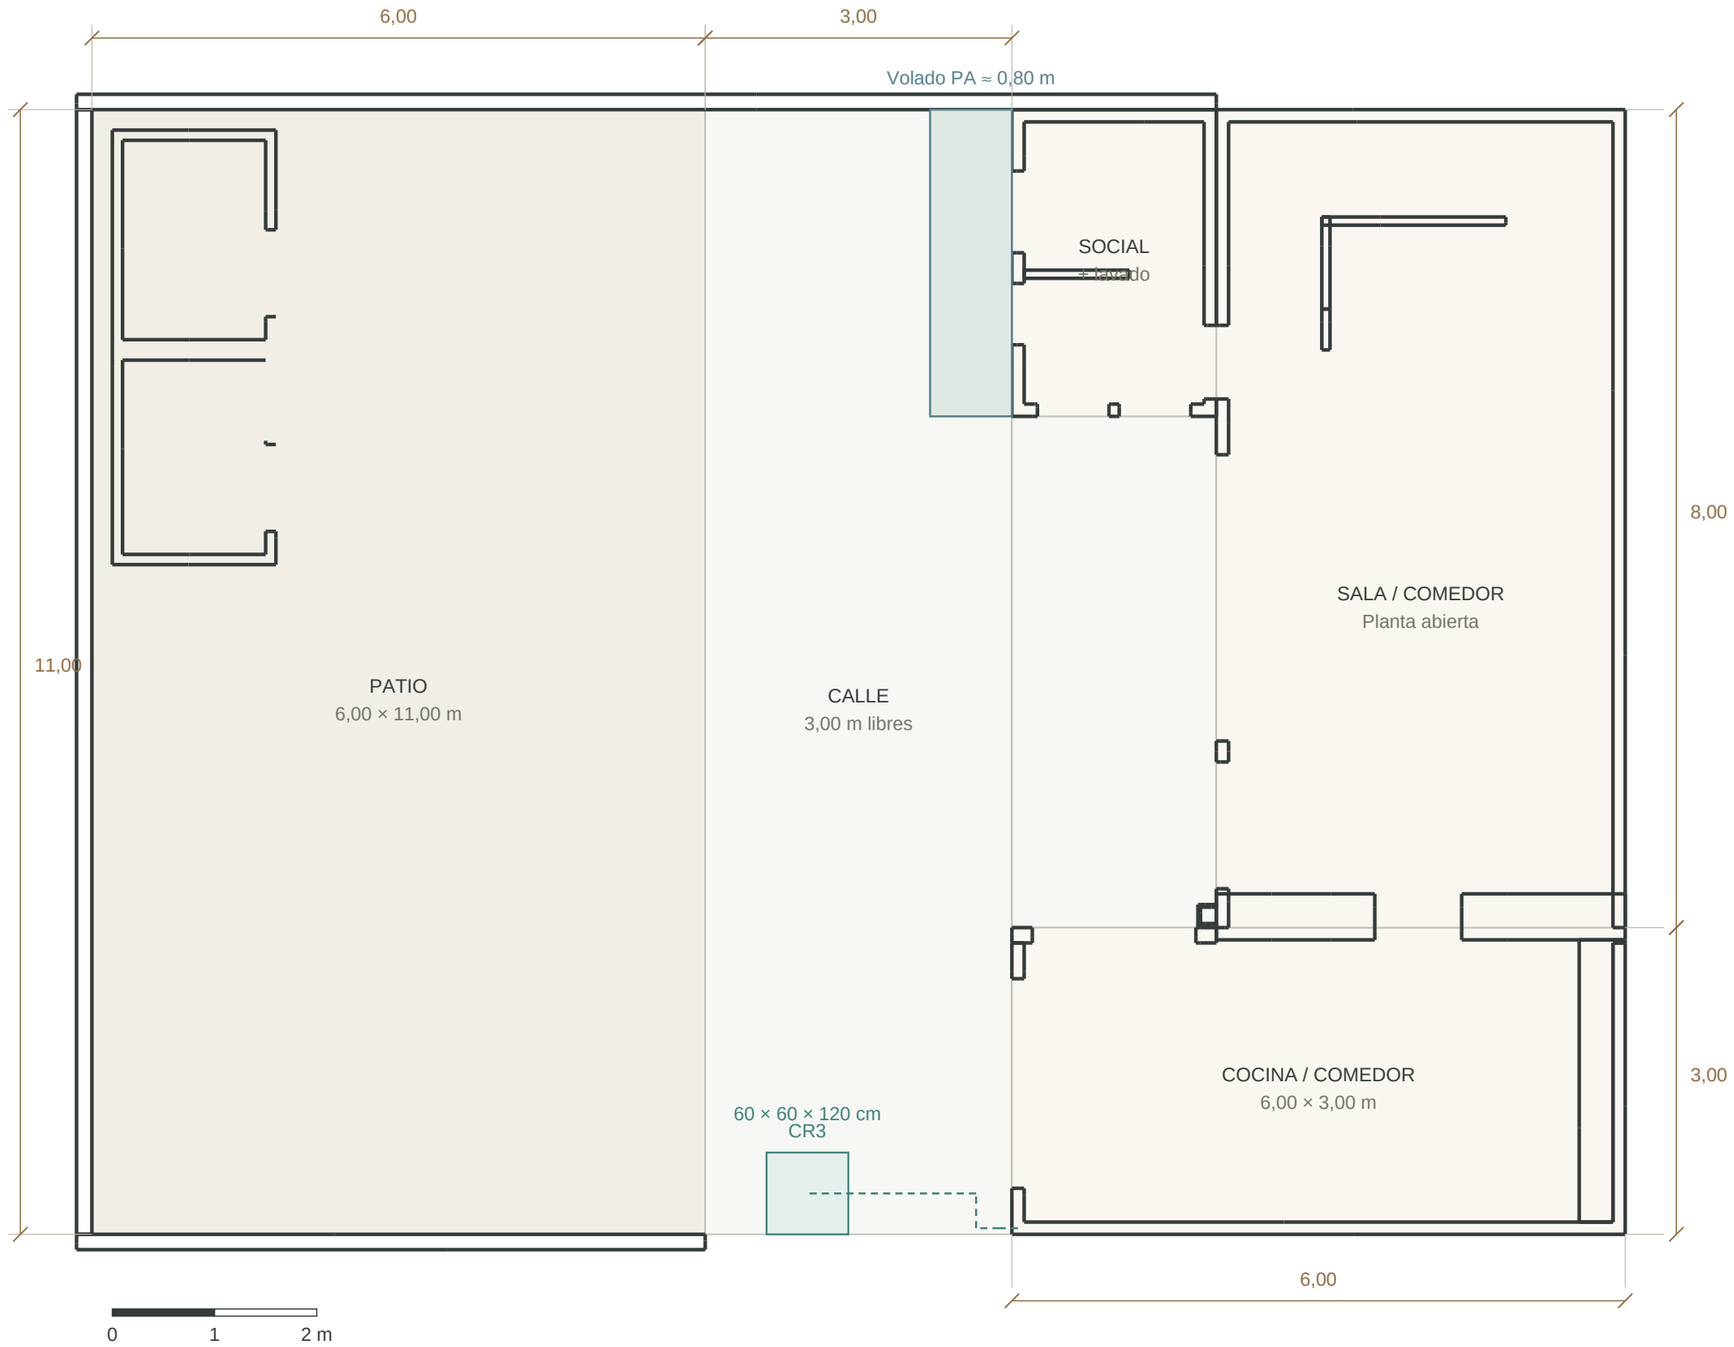



FRENTE / LLEGADA DESDE LA CALLE

# A-02 · Planta baja · cocina, sala y servicios

CASA LALES · MAPA COMPLETO · ESCALA 1:40 · IMPRIMIR AL 100 %


Revisión 12/11/2026 · 2212a8f4

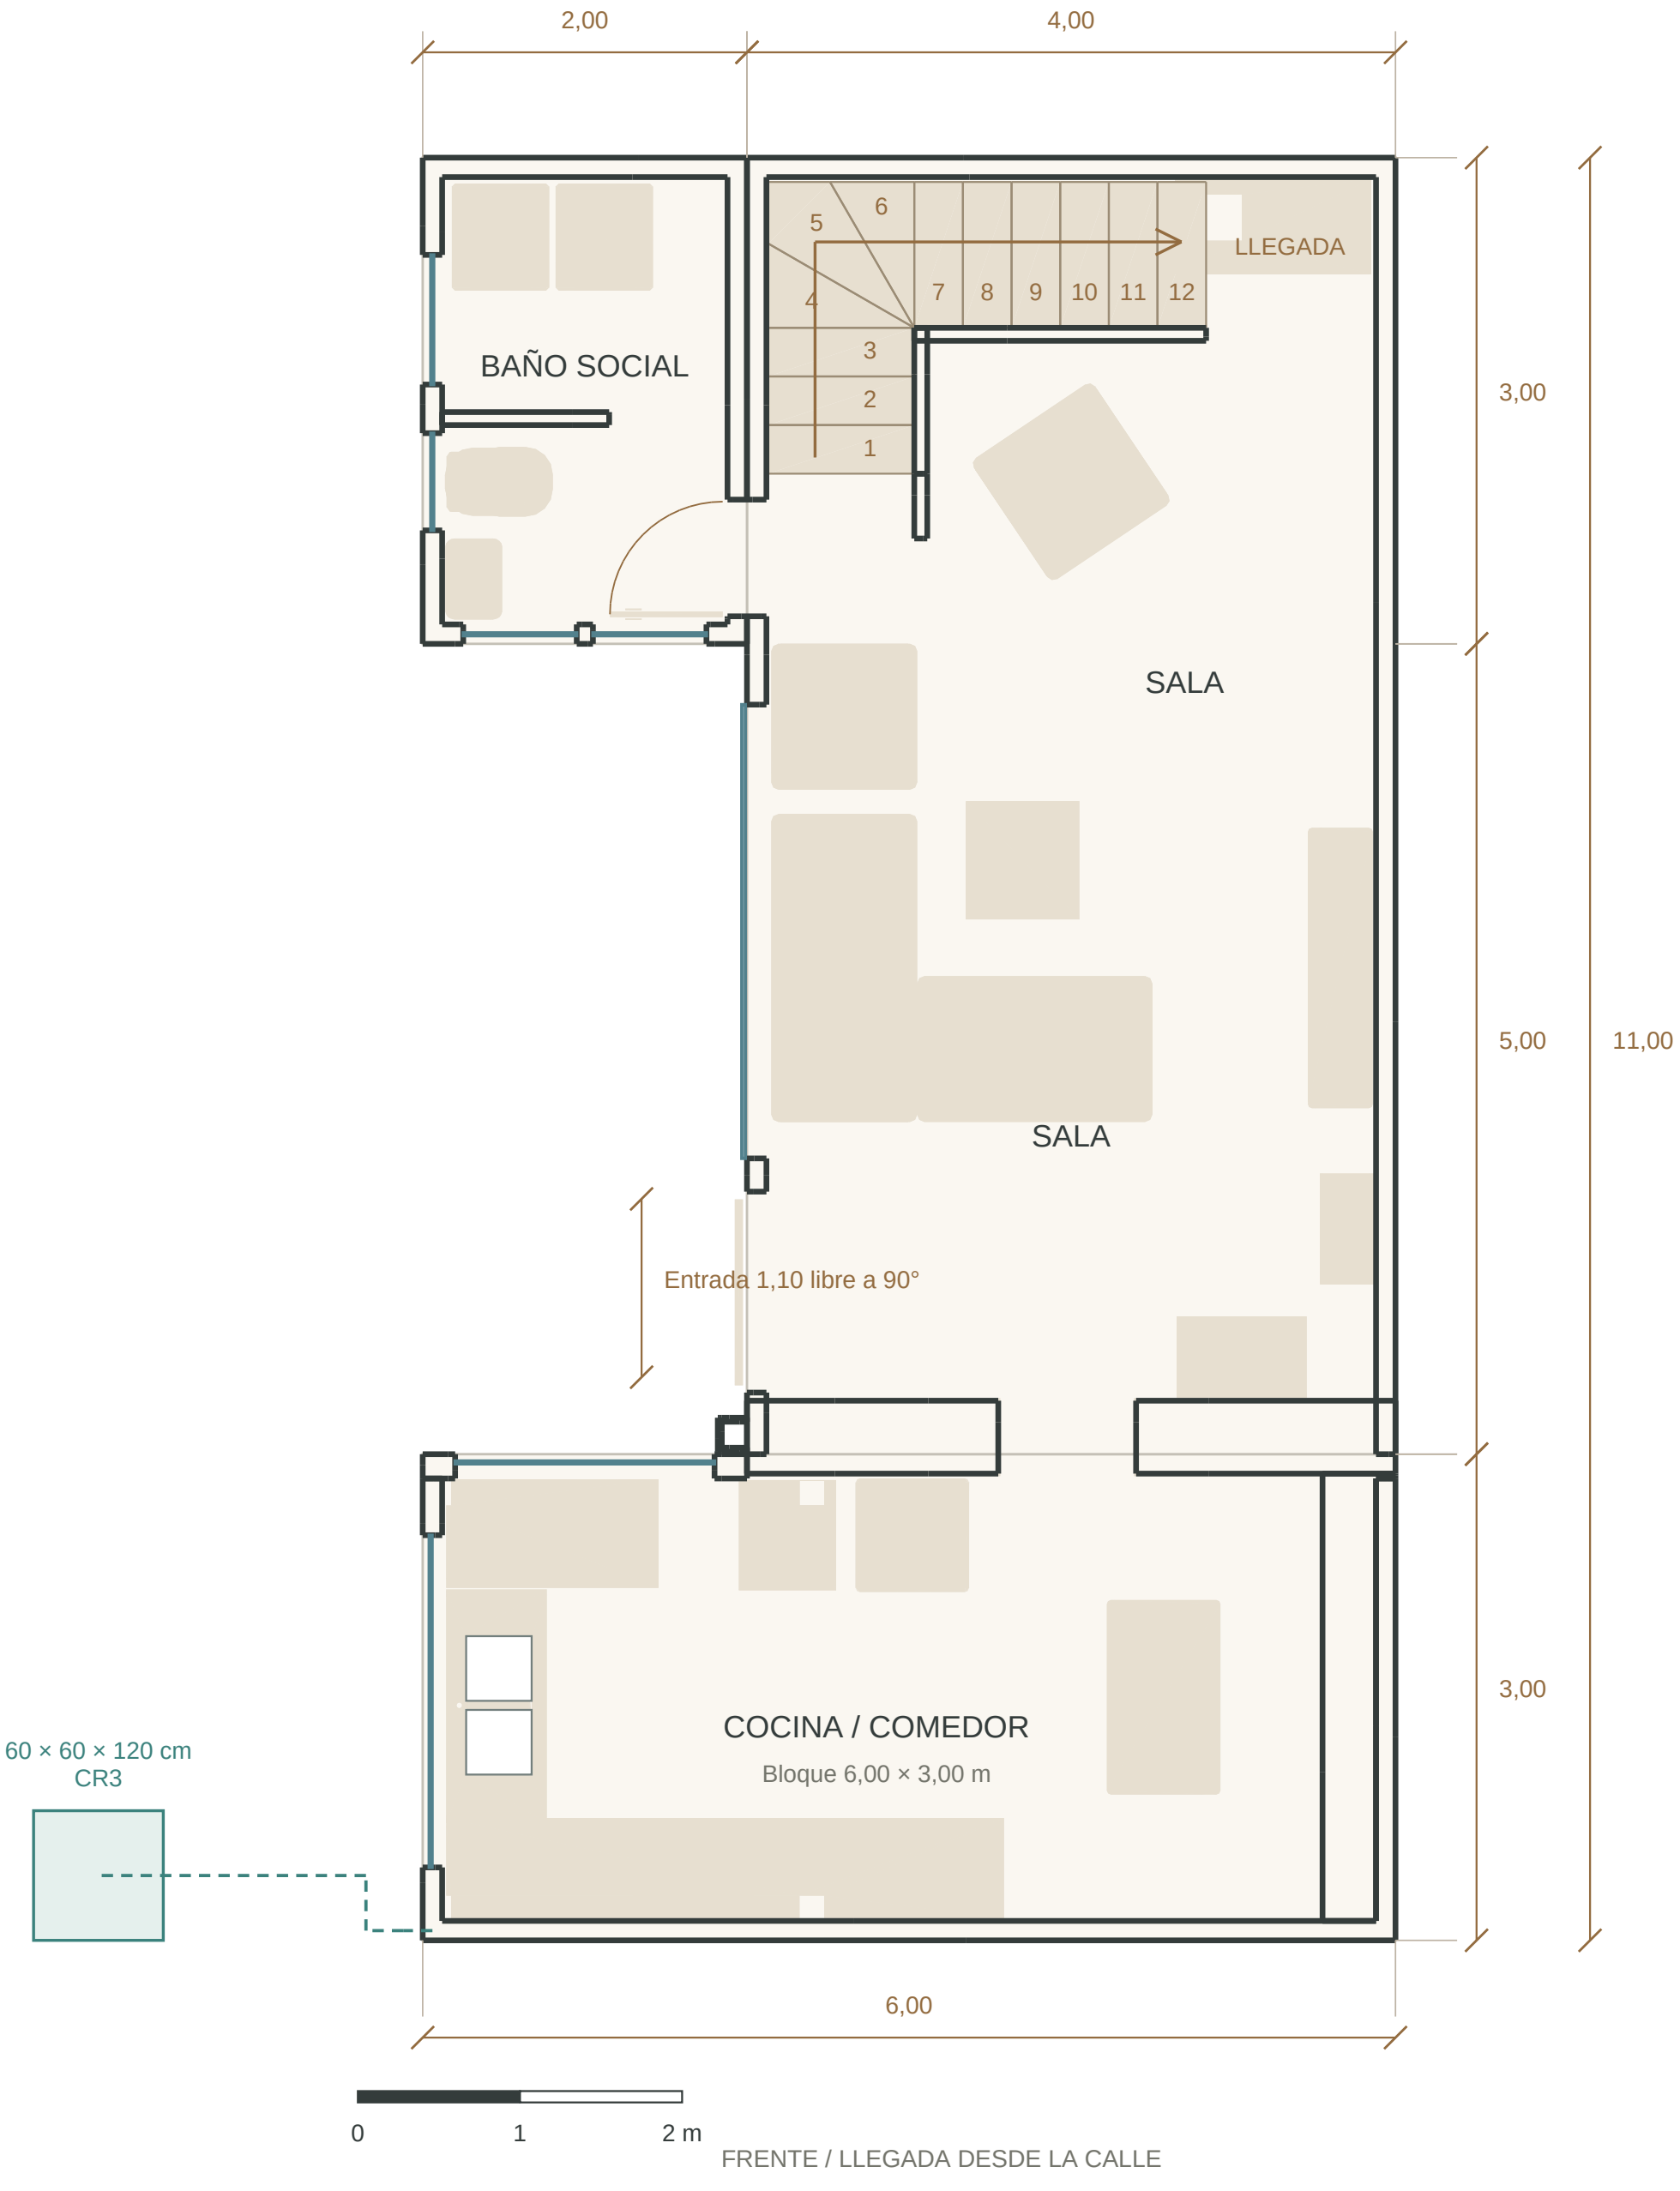

# A-08 · Entrada · paso libre y traslado de sillones

CASA LALES · MAPA COMPLETO · ESCALA 1:25 · IMPRIMIR AL 100 %


Revisión 12/11/2026 · 2212a8f4

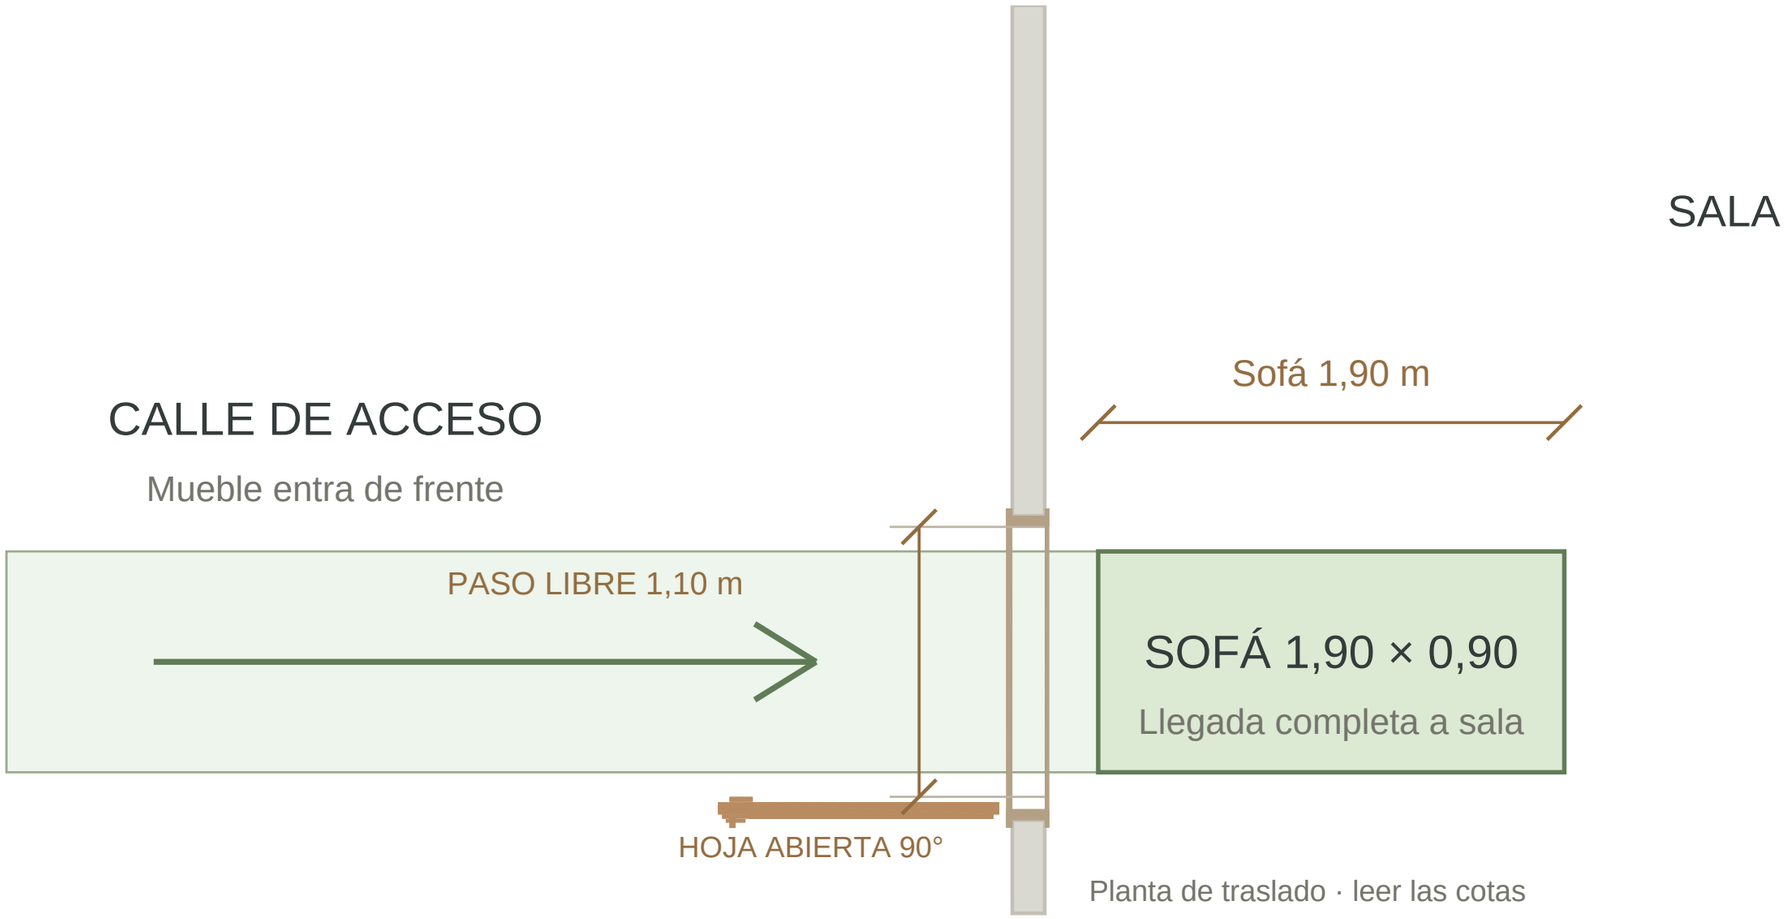

# A-03 · Planta alta · dormitorio, estudio y balcón

CASA LALES · MAPA COMPLETO · ESCALA 1:40 · IMPRIMIR AL 100 %


Revisión 12/11/2026 · 2212a8f4

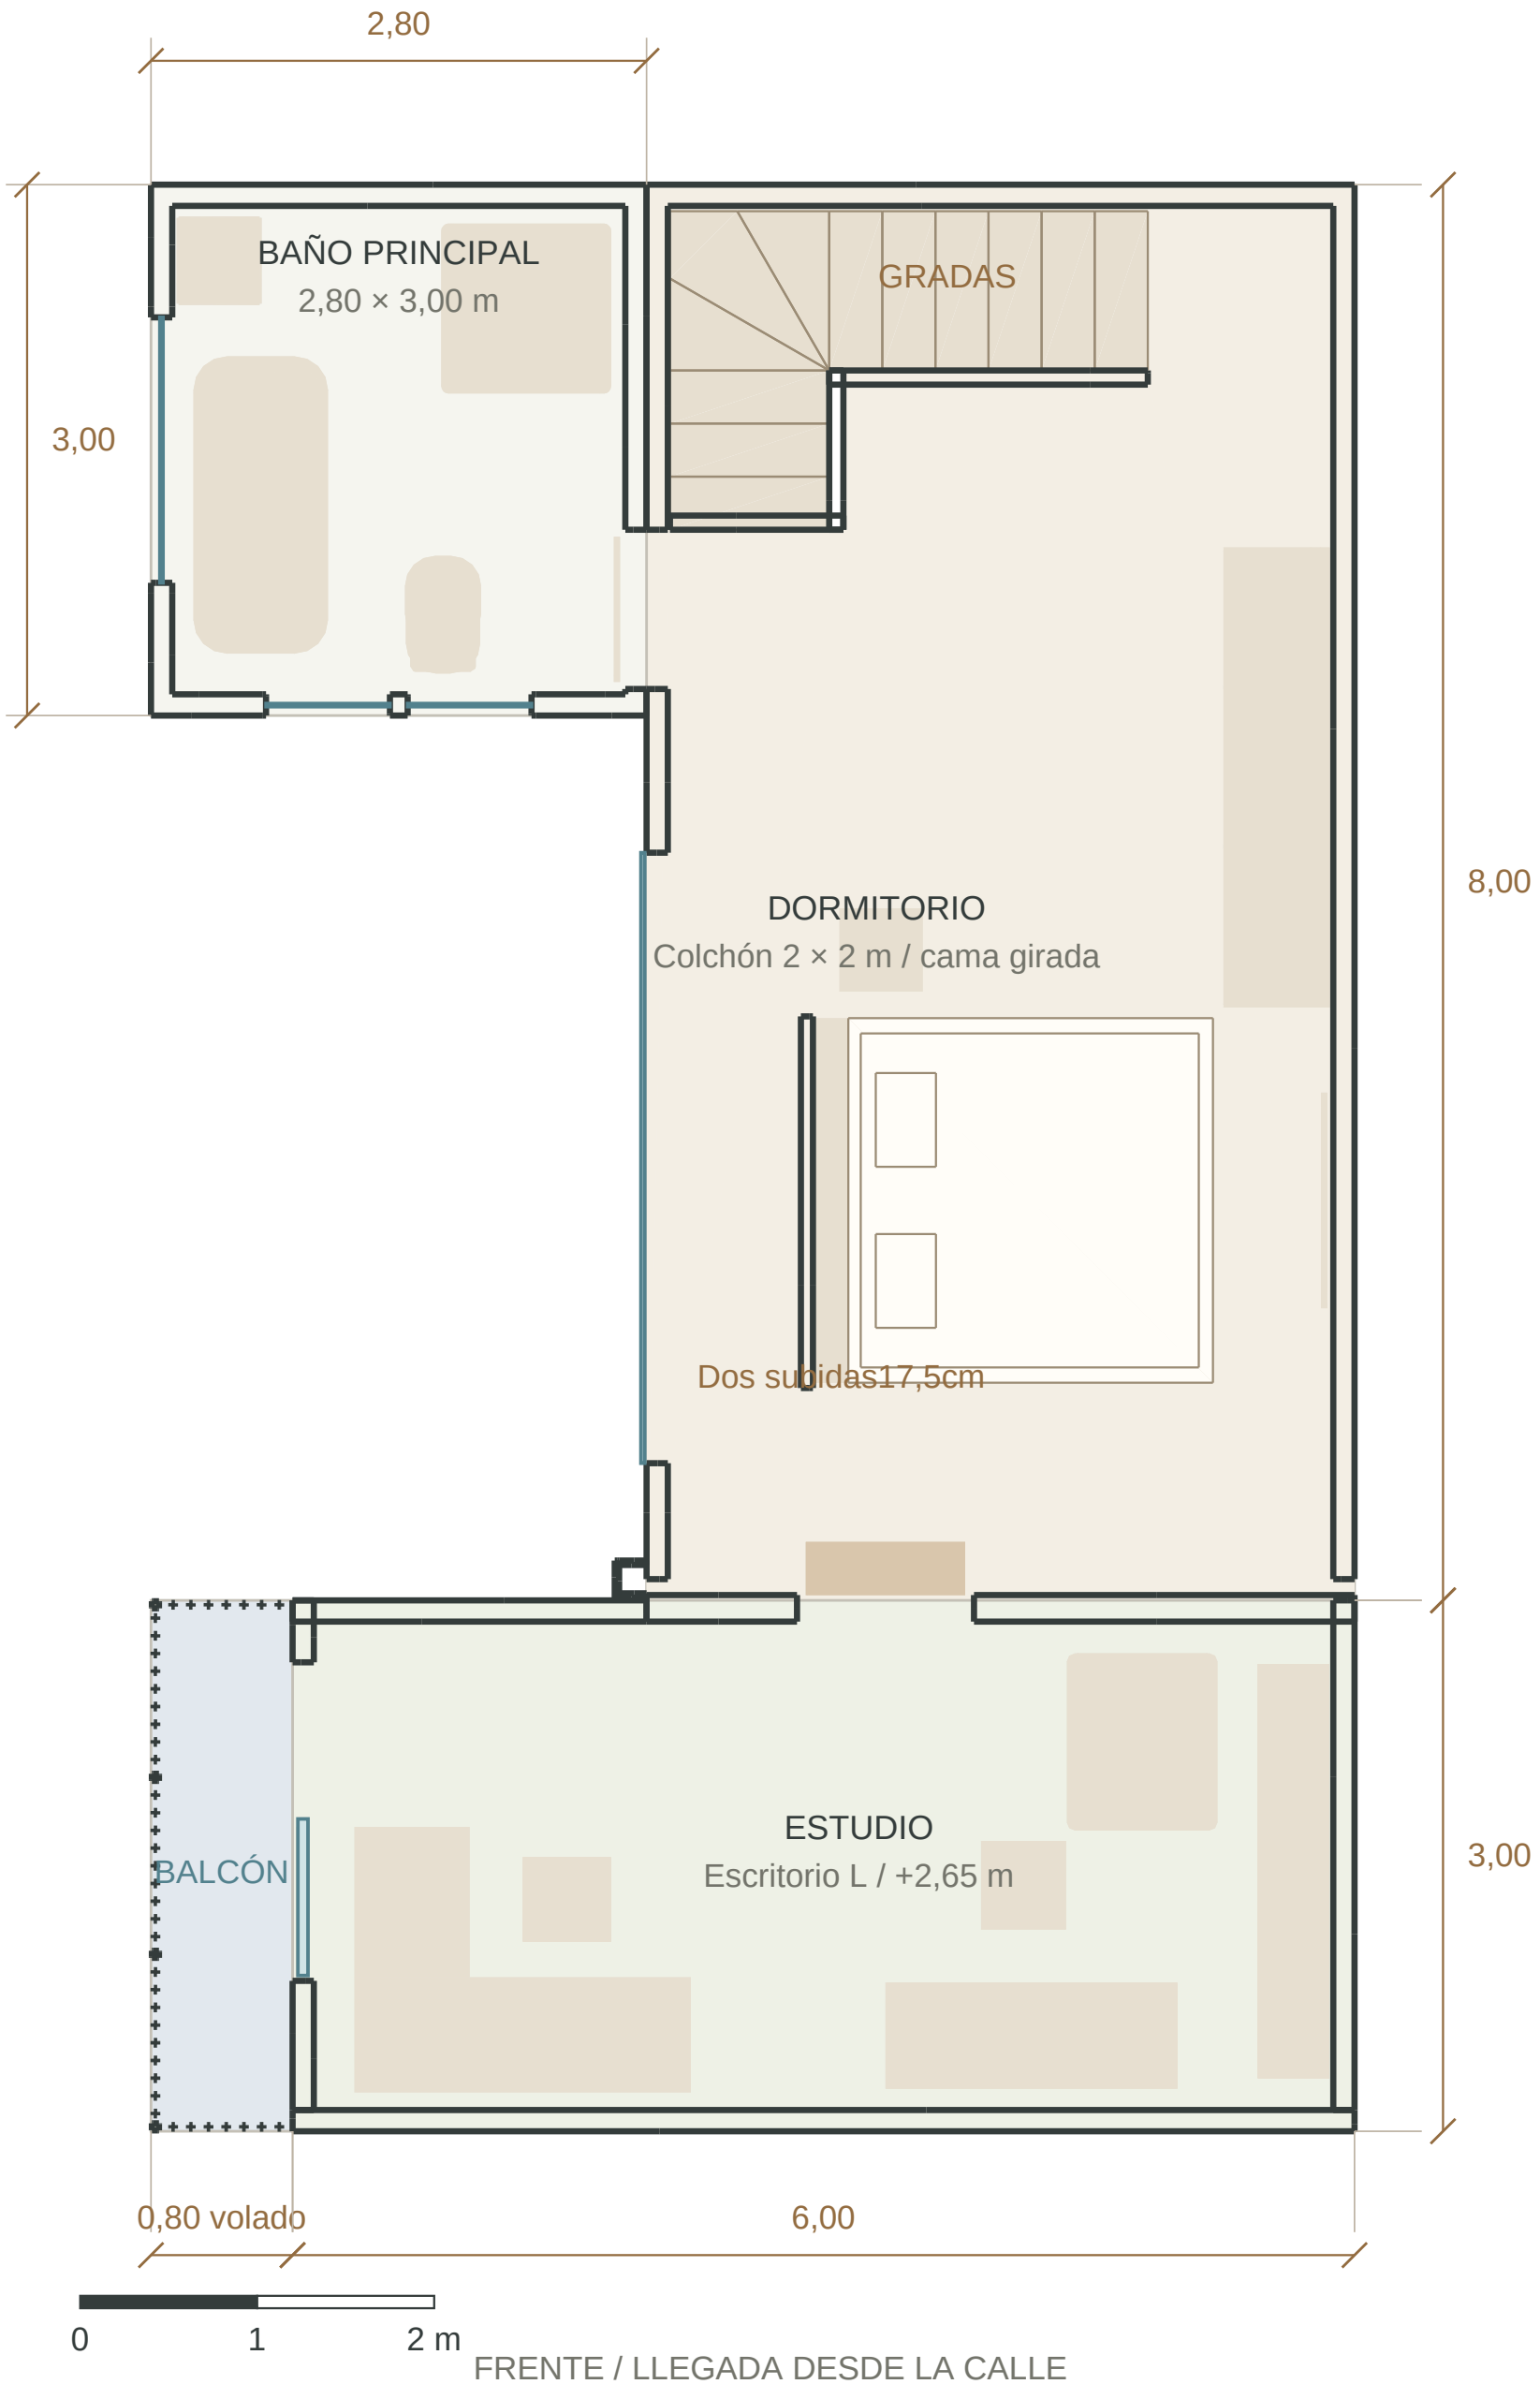

# A-04 · Patio · baño, bodega y asadero

CASA LALES · MAPA COMPLETO · ESCALA 1:40 · IMPRIMIR AL 100 %


Revisión 12/11/2026 · 2212a8f4

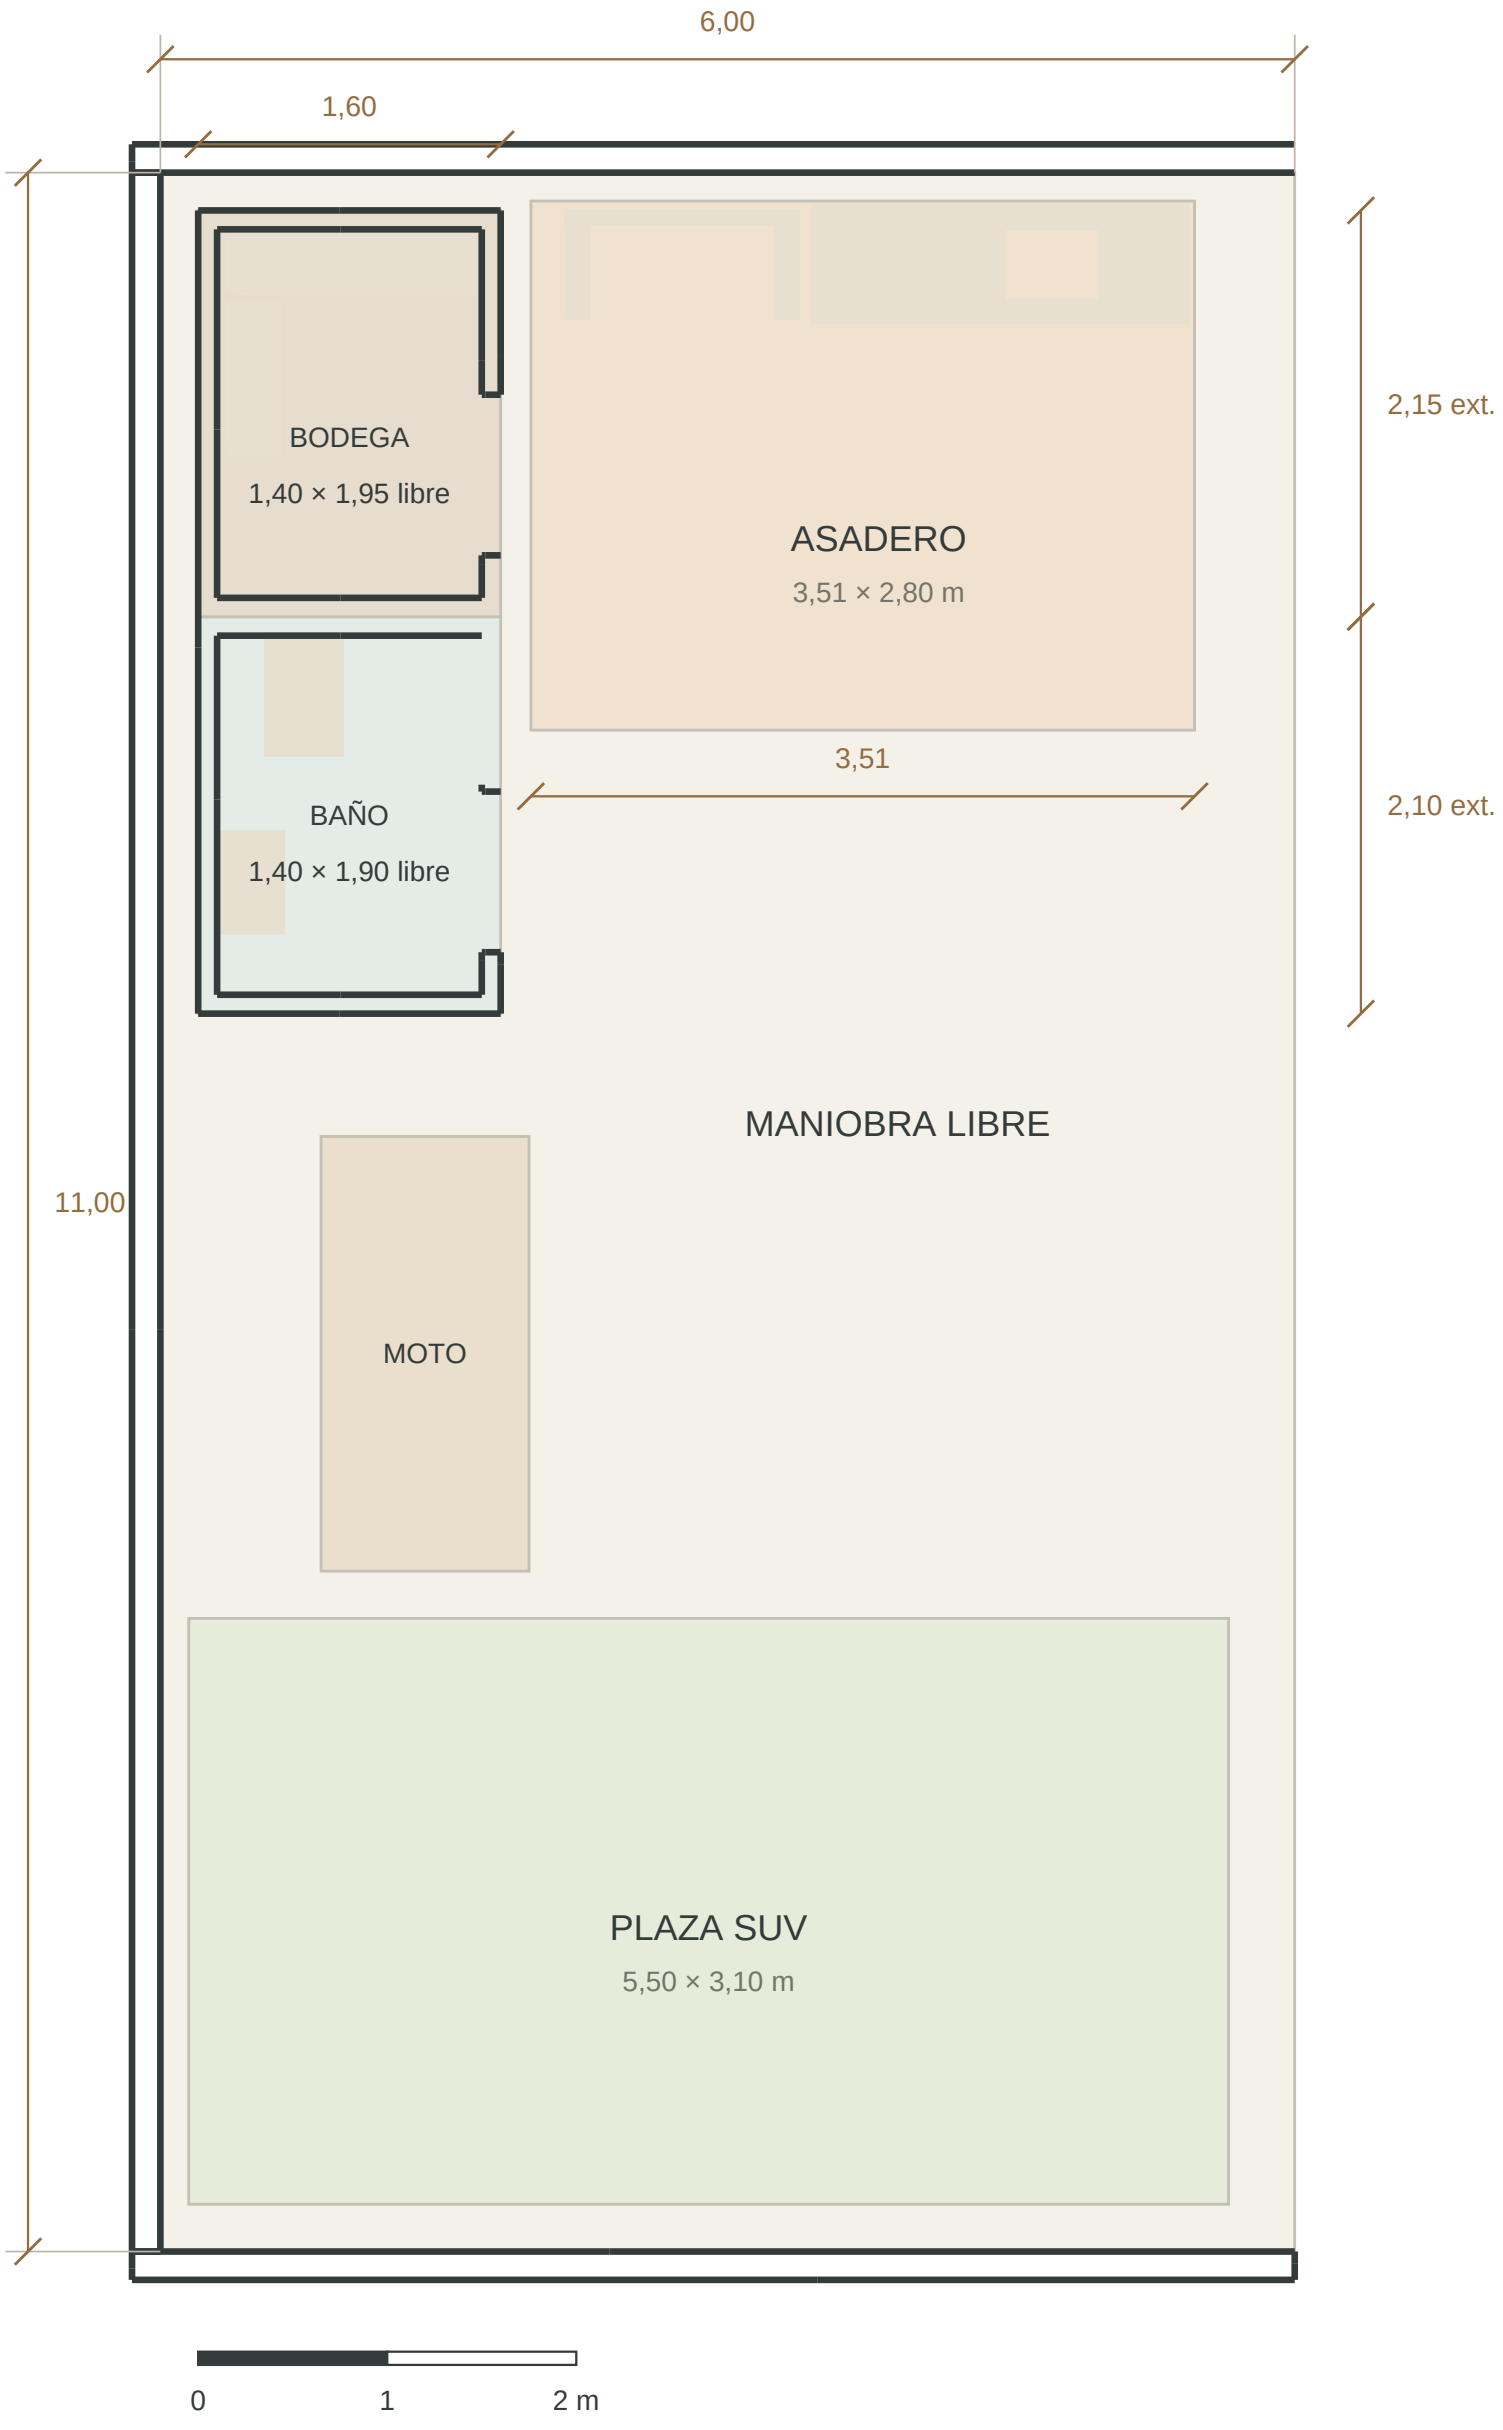

# E-01T · Tomacorrientes y equipos · Planta baja

CASA LALES · MAPA COMPLETO · ESCALA 1:40 · IMPRIMIR AL 100 %

Revisión 12/11/2026 · 2212a8f4

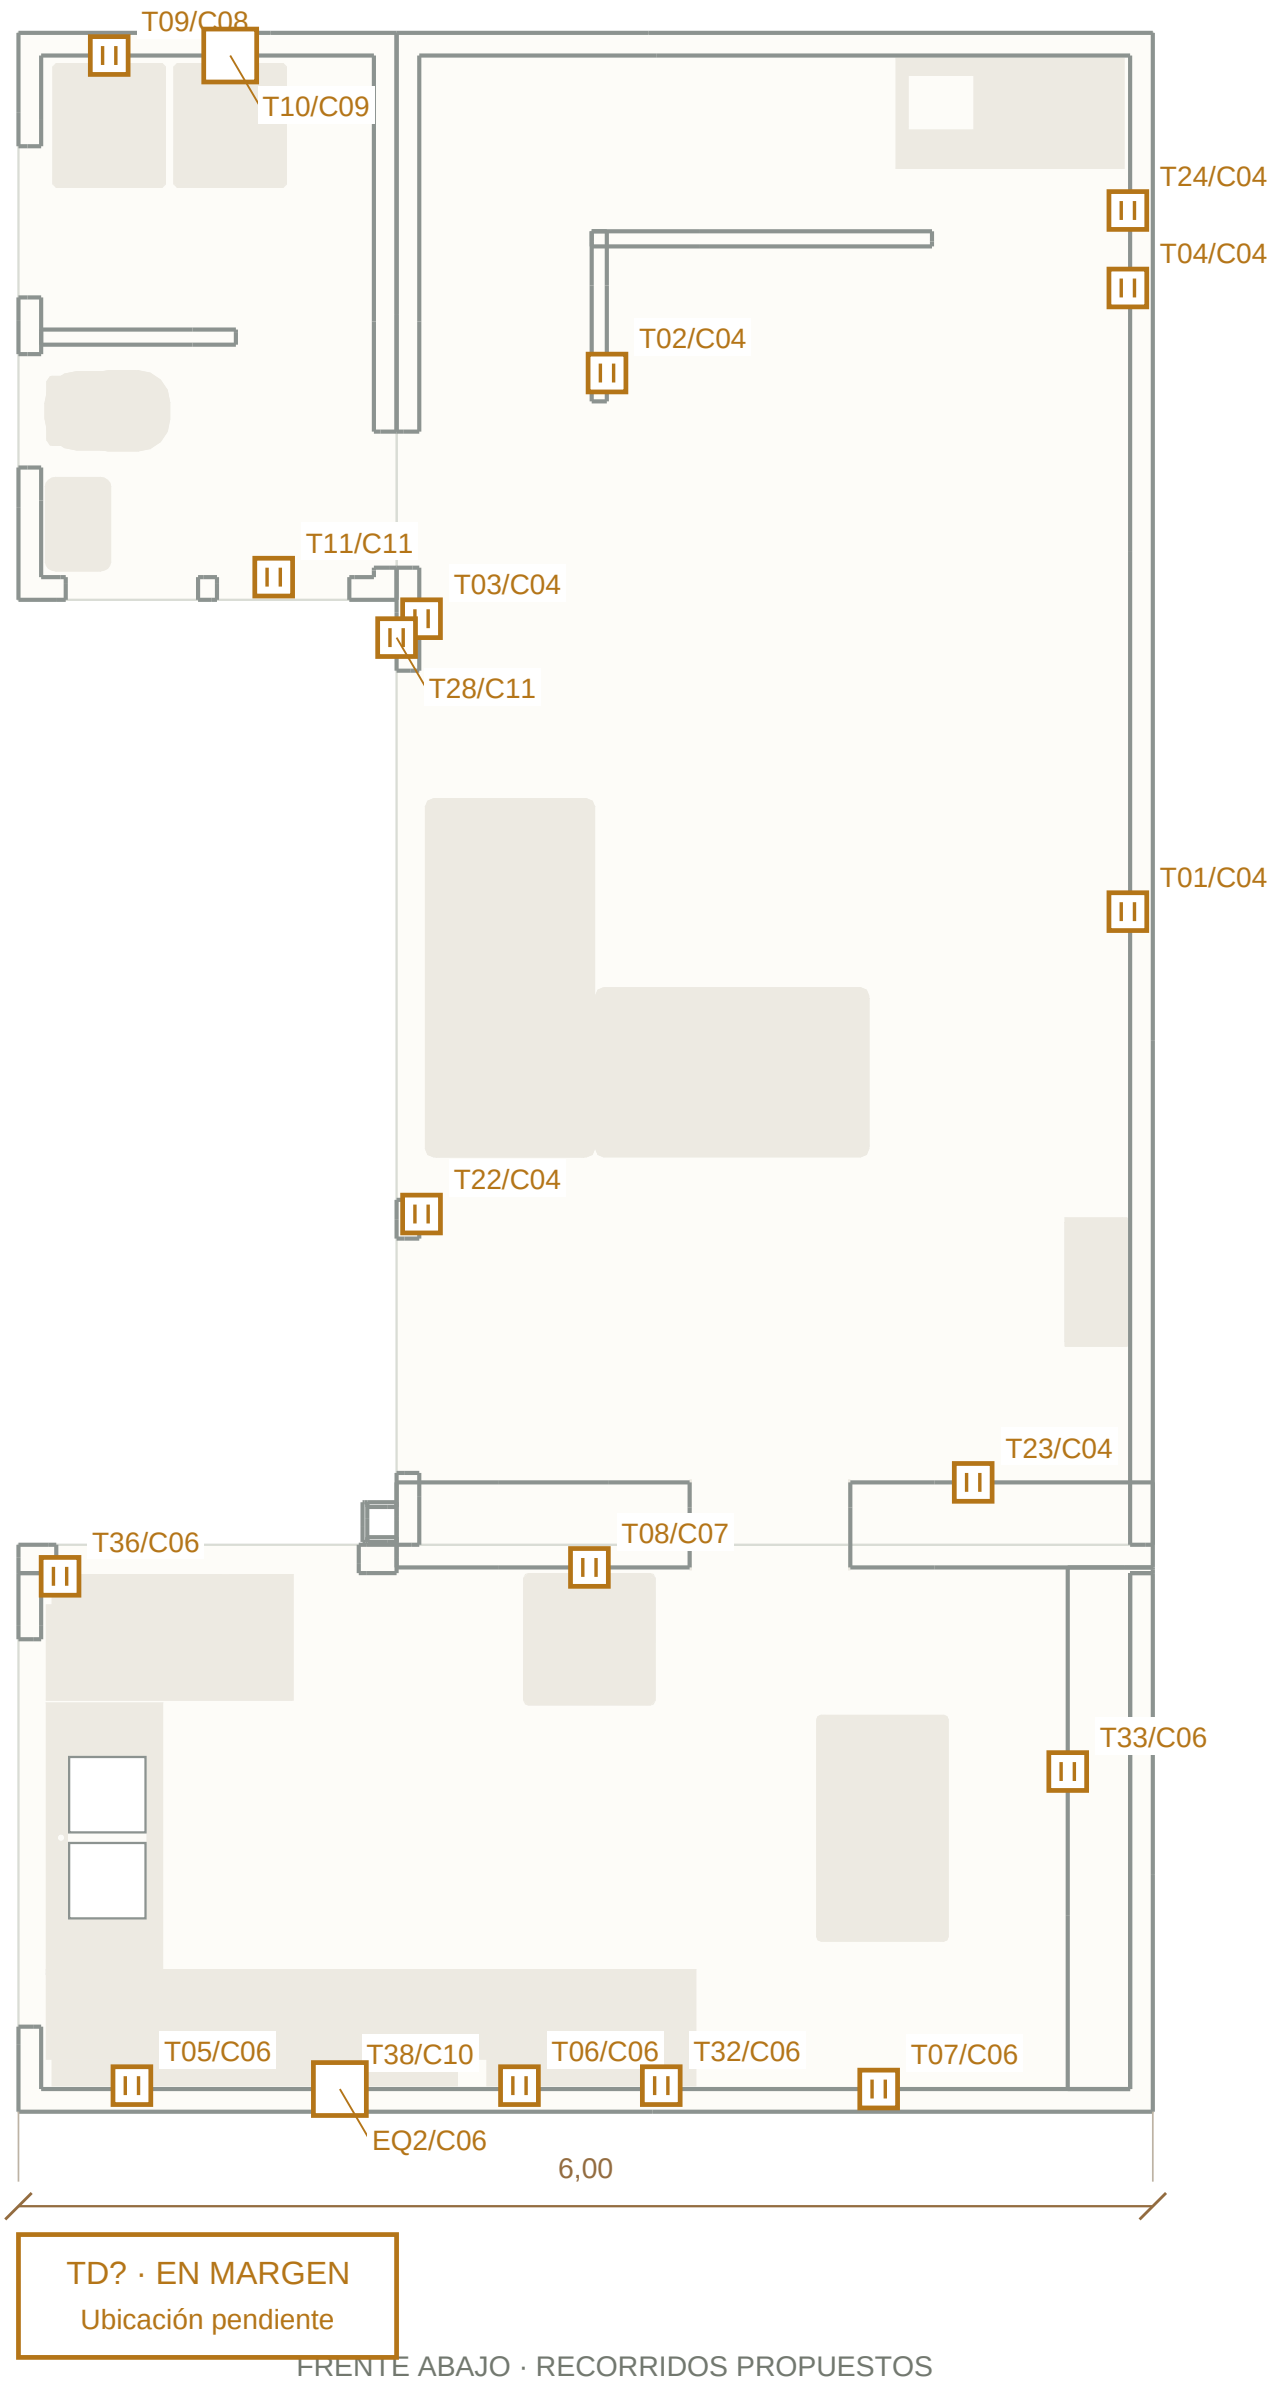


Simbología y notas en la hoja siguiente.

# EXPLICACIÓN · E-01T

Tomacorrientes y equipos · Planta baja

Casa Lales · Revisión 12/11/2026 · 2212a8f4

## QUÉ SIGNIFICA CADA FIGURA



**Cuadrado con dos rayas · T**

Tomacorriente. Código T y grupo C coinciden con el visor 3D; no indican voltaje ni amperaje.



**Cuadrado vacío · reserva**

EQ1: cocción; EQ2: campana. T10: conexión de secadora por definir según equipo.



**Líneas grises · muro**

Paredes del modelo como referencia para situar los puntos.




**C04-C11 · grupo funcional**

El sufijo /C identifica un uso propuesto, sujeto al cálculo de cargas y protecciones.




**Rectángulo TD? · tablero**

Se dibuja al margen. La ubicación y las protecciones siguen pendientes.



**Figura beige · mueble o aparato**

Huella de referencia; se conservan las posiciones del modelo.

## DATOS Y CRITERIOS DEL PLANO

**Tomacorrientes: 19 puntos**

Códigos T conservados. /C identifica grupo funcional; no es voltaje ni capacidad.

**Reservas de equipos: 1 cajas**

EQ: conexión de equipo por definir. T10 sigue identificado como reserva para secadora.

**Plano de luces y mandos: E-01L**

Consultar su mapa independiente; no se representan aquí sus símbolos.

## NOTAS PARA REVISIÓN EN OBRA

Mismas posiciones y códigos que en imágenes 3D; alturas propuestas. Cabezal sin instalaciones.

Dimensiones y capacidades de conductores, protecciones y puesta a tierra pendientes de cálculo.


T10 es caja de conexión por definir según secadora; no se asigna tensión.

Baños y exterior: posición, protección y equipo apropiado por validar.

# E-01L · Iluminación y mandos · Planta baja

CASA LALES · MAPA COMPLETO · ESCALA 1:40 · IMPRIMIR AL 100 %

Revisión 12/11/2026 · 2212a8f4

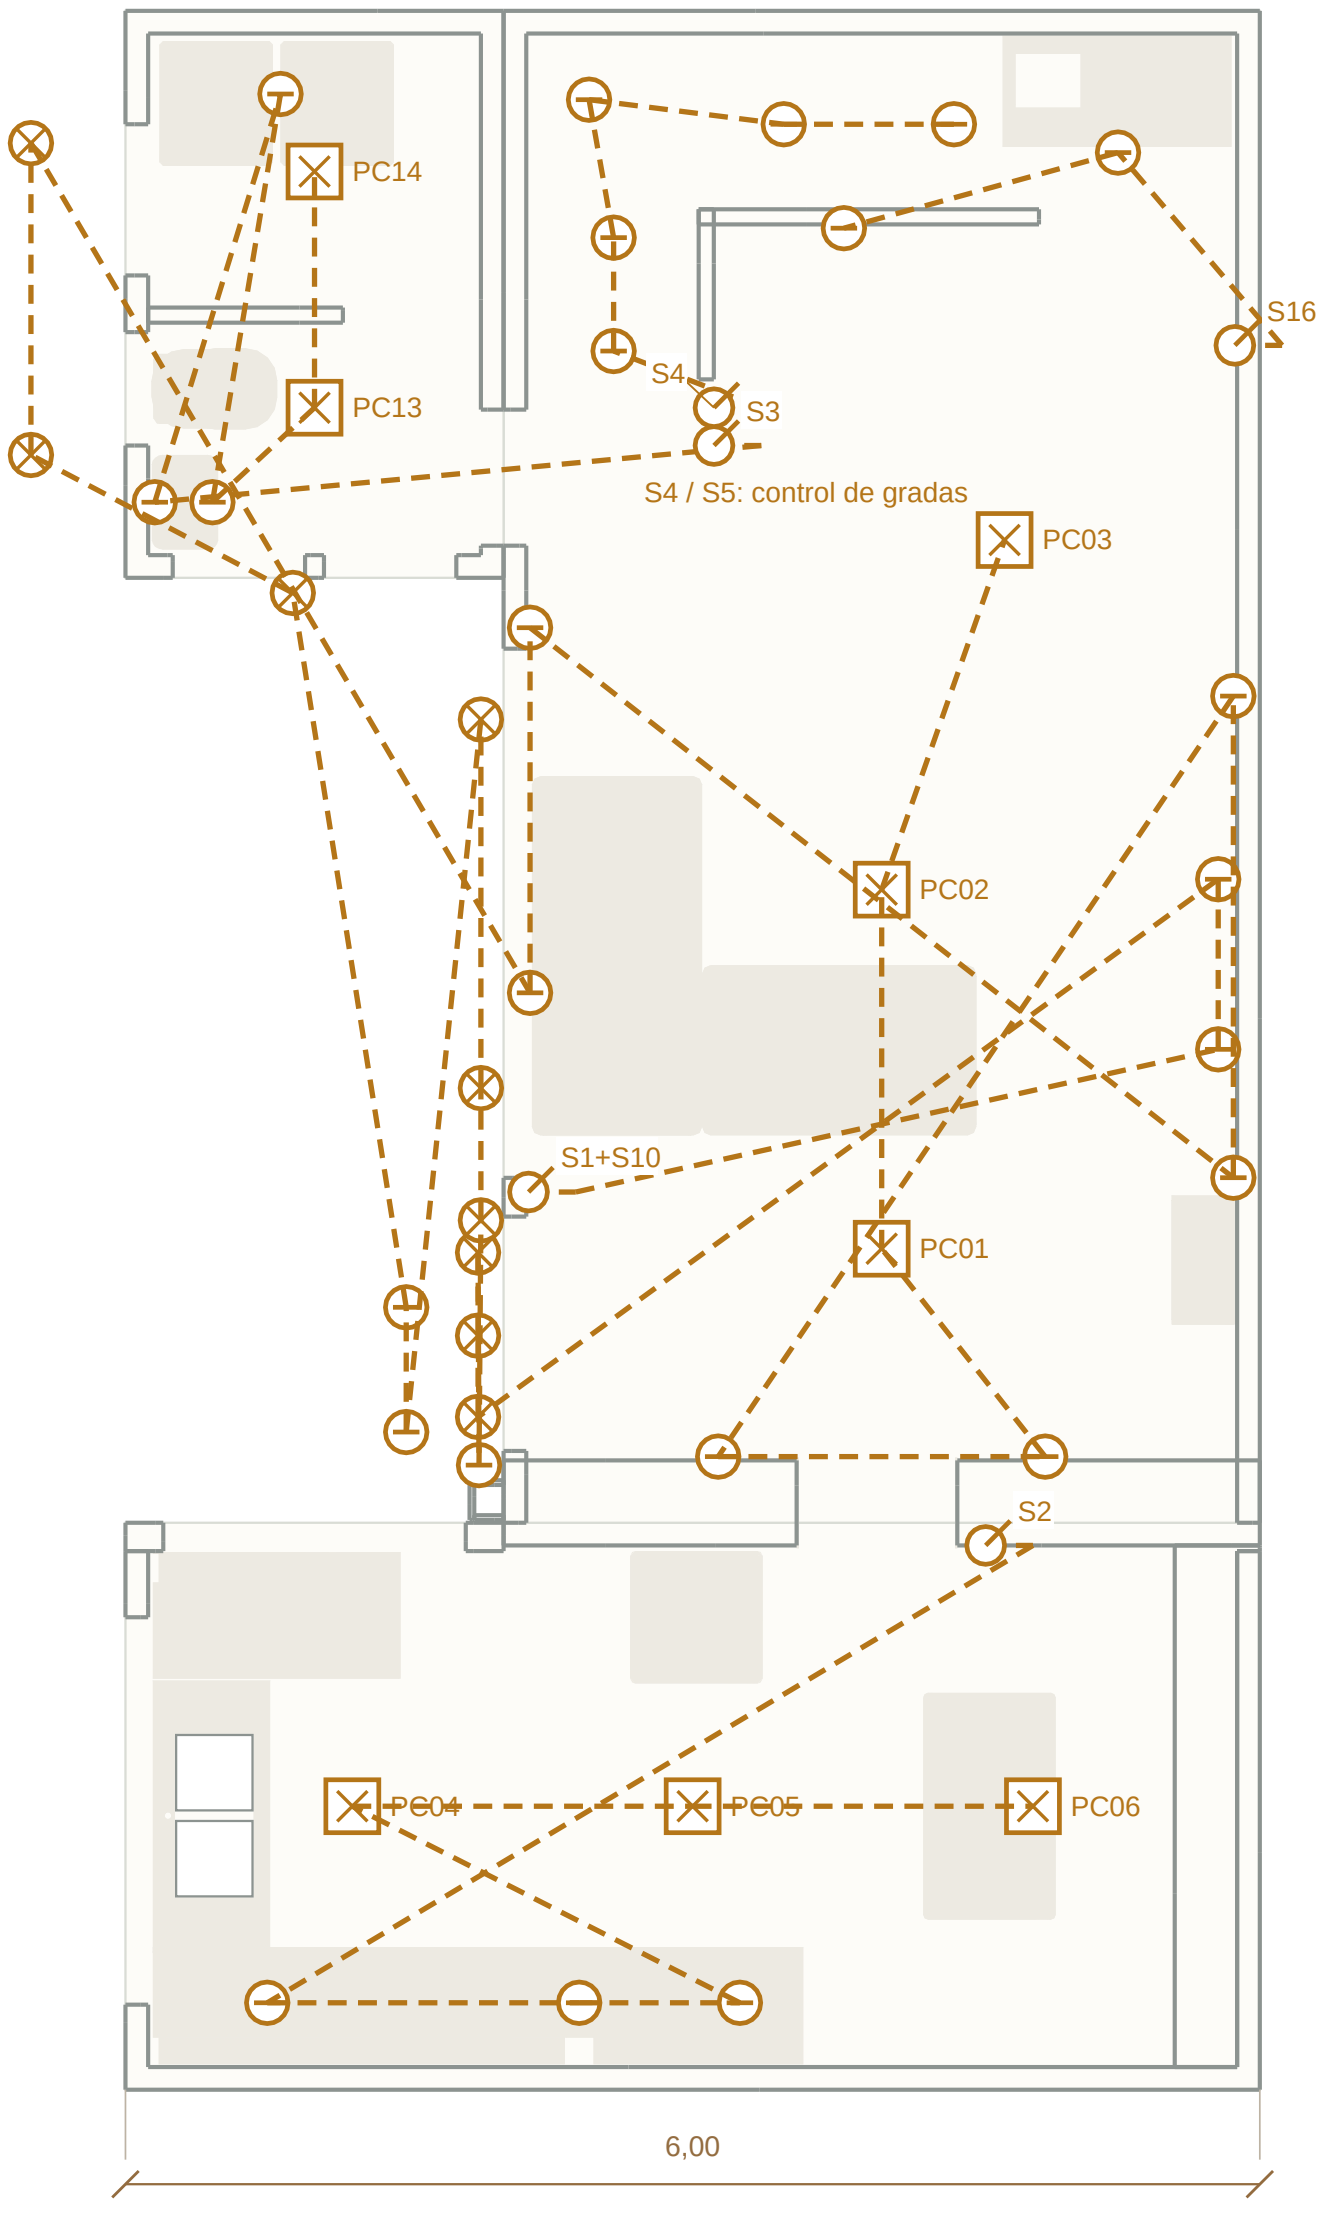


FRENTE ABAJO · RECORRIDOS PROPUESTOS

Simbología y notas en la hoja siguiente.

# EXPLICACIÓN · E-01L

Iluminación y mandos · Planta baja

Casa Lales · Revisión 12/11/2026 · 2212a8f4

## QUÉ SIGNIFICA CADA FIGURA

**Cuadrado con X · plafón PC**
Lámpara cuadrada de sobreponer. Cada código PC identifica una unidad; potencia y temperatura en el cuadro de esta hoja.

**Círculo con X · luz general**
Punto de iluminación general del modelo. No equivale siempre a una unidad comercial.

**Círculo con raya · luz de apoyo**
Referencia de trabajo o ambiente: LED, espejo, mueble, aplique o escalón.

**Círculo con trazo · S**
Interruptor o caja de teclas. Misma posición y código que el visor; S4/S5 coordinan las gradas.

**Línea punteada · relación de mando**
Relaciona el mando con sus luces. No fija un cableado, conductores ni trayecto de ejecución.

**Líneas grises · muro**
Paredes del modelo como referencia para situar los puntos.

**Figura beige · mueble o aparato**
Huella de referencia; se conservan las posiciones del modelo.

## DATOS Y CRITERIOS DEL PLANO

**Iluminación general: 8 plafones PC / 9 otros**
Cuadrado con X: plafón PC; círculo con X: otra luz general.

**Luz de trabajo / ambiente: 24 referencias**
Círculo con raya; incluye LED, apliques y apoyos.

**Cajas de mandos: S1+S10, S2, S3, S4, S16**
S4/S5: coordinar el control de gradas desde ambos niveles.

**Plano de tomacorrientes: E-01T**
Consultar su mapa independiente; no se representan aquí sus símbolos.

**Sala: 3 × 24 W · 3000 K**
Interior seco

**Cocina y comedor: 3 × 24 W · 4000 K**
Interior seco

**Baño social y lavandería: 2 × 12 W · 4000 K**
Sellado para zona húmeda; por confirmar

## NOTAS PARA REVISIÓN EN OBRA

Mismas tomas y mandos que en imágenes 3D. Alturas propuestas; dormitorio según distribución aplicada.

Líneas punteadas: relación de mando y recorrido conceptual; no son número de conductores.

Grupos C01-C12 funcionales: dividir por planta, cargas y protecciones en cálculo. Tablero y tierra pendientes.

Bajo Eternit: canalización y cajas fijadas a soporte definido, nunca a las planchas.

Las luces de gradas se asignan a PB o PA por cota: cada referencia aparece una sola vez.

PC: plafón cuadrado sobrepuesto. Modelo seco de referencia 28,5 × 28,5 × 2,8 cm, 24 W, 1800 lm, 0,583 kg; 100–240 V. Confirmar equipo y suministro.

Fijar herraje a perfil/refuerzo del cielo; no cargar sólo la placa. Revisar perfilería, anclaje y acceso al driver; no suspender del Eternit.


Baños: variante sellada IP44 mínimo; IP65 si la zona lo exige. Potencia y formato menores orientativos; modelo y protección por elegir.

Plafón de referencia sin dimmer. LED indirecto y tarea separados. Cantidad propuesta; verificar iluminación con fotometría y medidas reales.

# E-02T · Tomacorrientes y equipos · Planta alta

CASA LALES · MAPA COMPLETO · ESCALA 1:40 · IMPRIMIR AL 100 %

Revisión 12/11/2026 · 2212a8f4

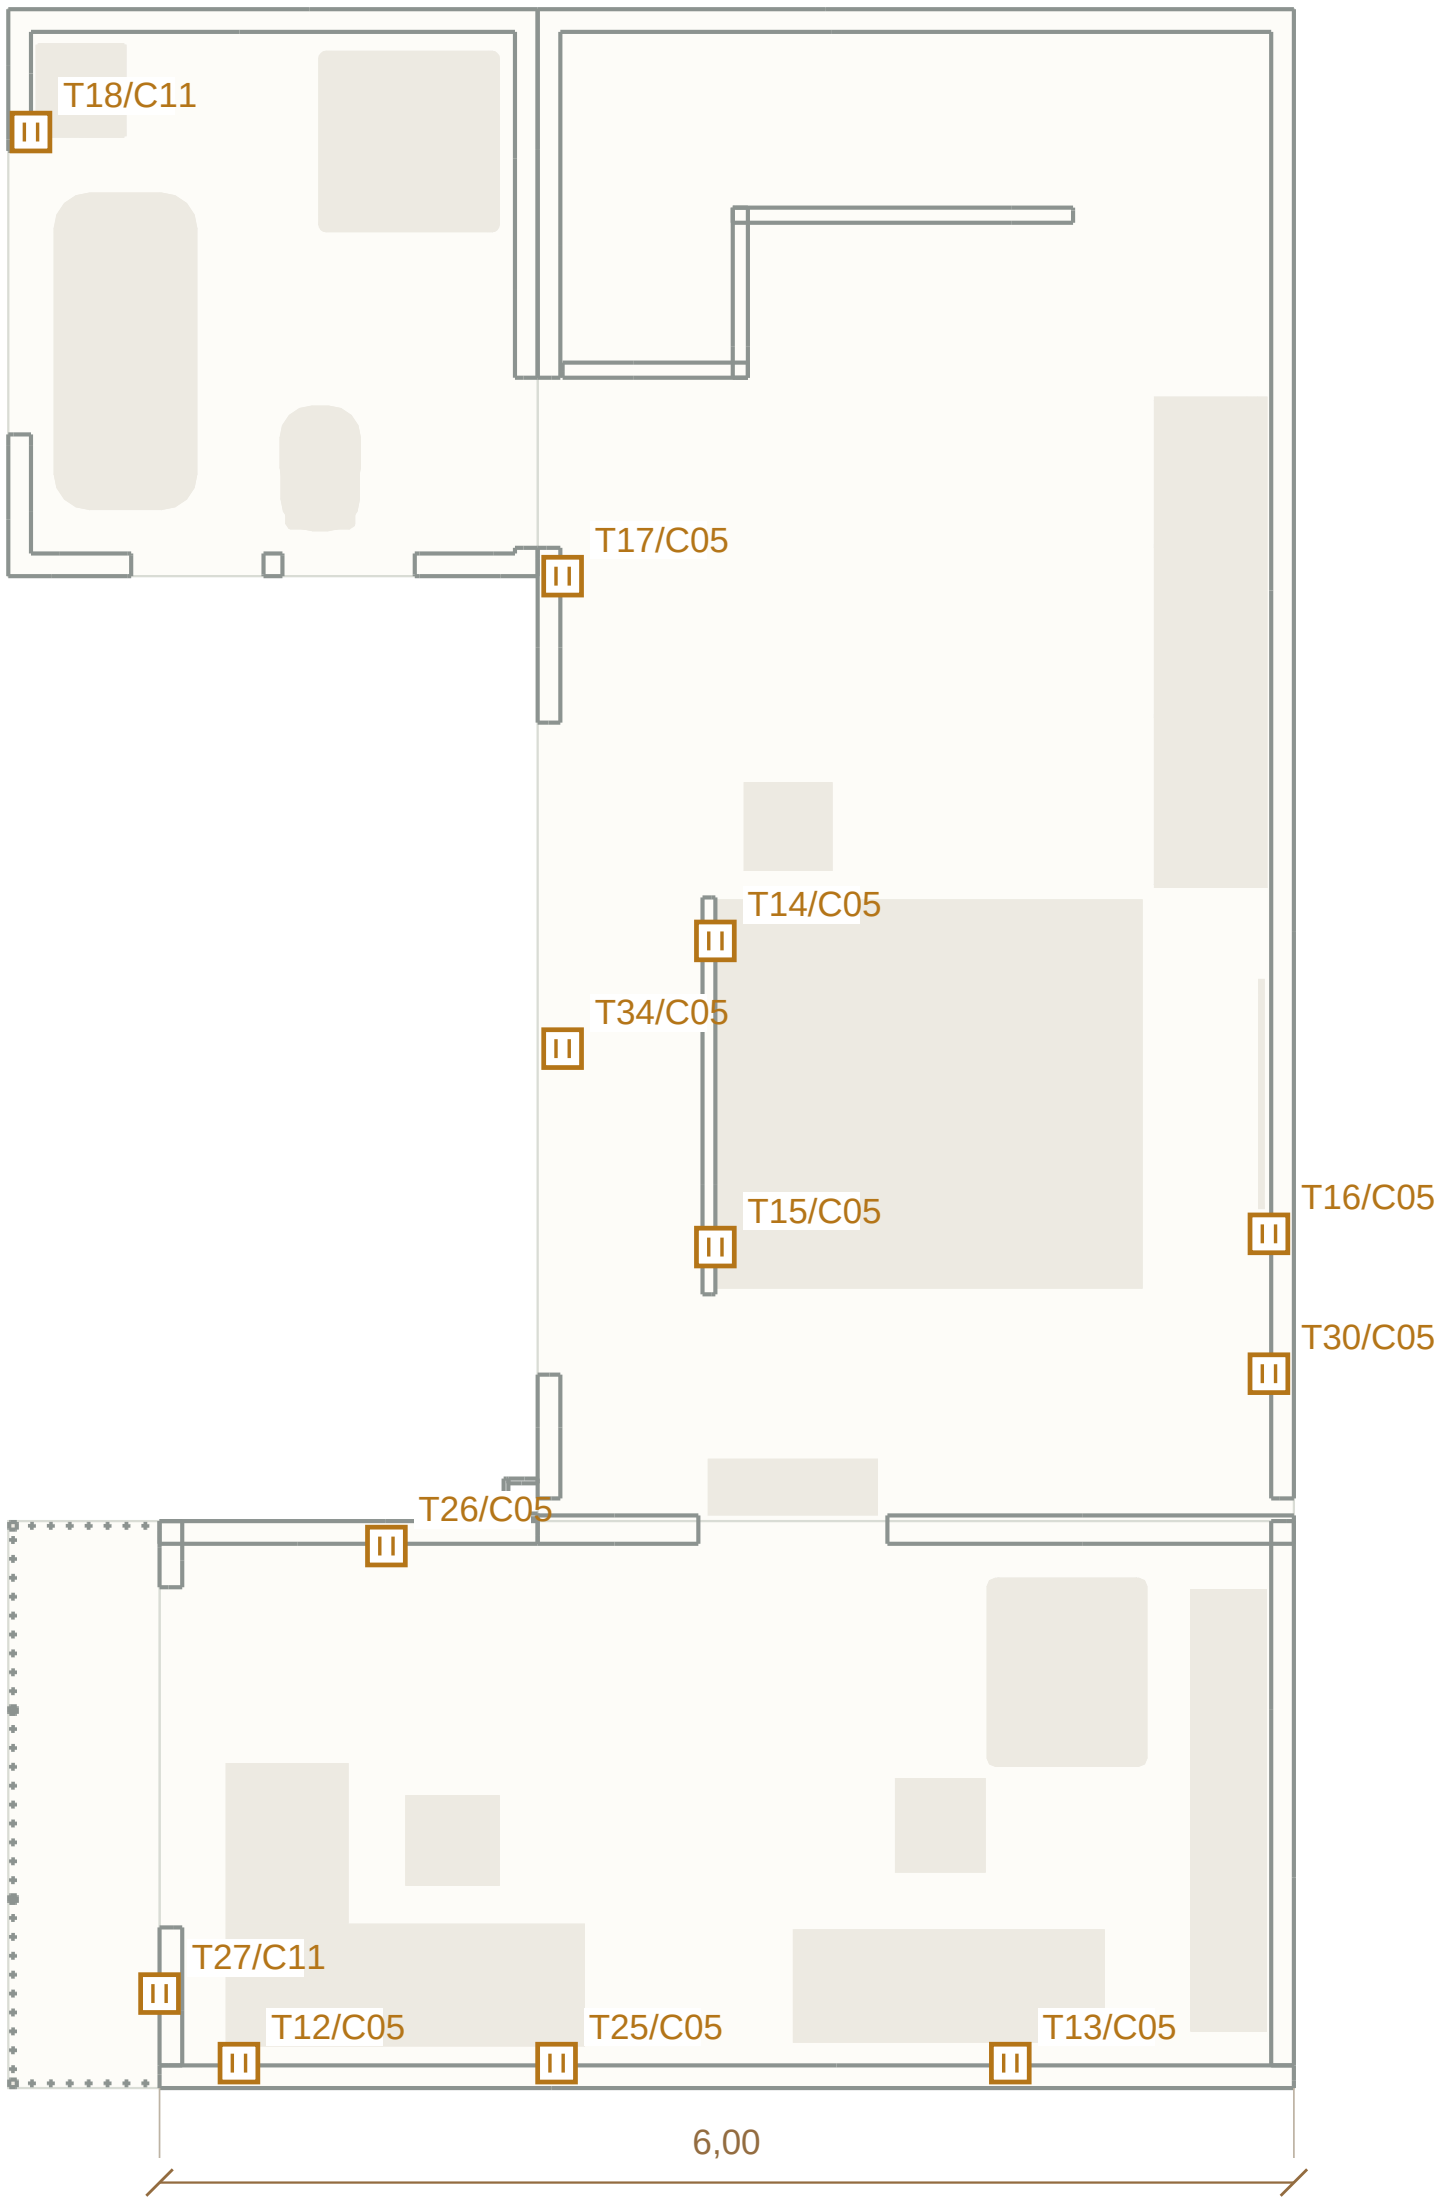


FRENTE ABAJO · RECORRIDOS PROPUESTOS

Simbología y notas en la hoja siguiente.

# EXPLICACIÓN · E-02T

Tomacorrientes y equipos · Planta alta

Casa Lales · Revisión 12/11/2026 · 2212a8f4

## QUÉ SIGNIFICA CADA FIGURA



**Cuadrado con dos rayas · T**

Tomacorriente. Código T y grupo C coinciden con el visor 3D; no indican voltaje ni amperaje.

C01

**C04-C11 · grupo funcional**

El sufijo /C identifica un uso propuesto, sujeto al cálculo de cargas y protecciones.



**Líneas grises · muro**

Paredes del modelo como referencia para situar los puntos.



**Figura beige · mueble o aparato**

Huella de referencia; se conservan las posiciones del modelo.

## DATOS Y CRITERIOS DEL PLANO

**Tomacorrientes: 12 puntos**

Códigos T conservados. /C identifica grupo funcional; no es voltaje ni capacidad.

**Reservas de equipos: 0 cajas**

No hay cajas EQ adicionales en este nivel.

**Plano de luces y mandos: E-02L**

Consultar su mapa independiente; no se representan aquí sus símbolos.

## NOTAS PARA REVISIÓN EN OBRA

Mismas posiciones y códigos que en imágenes 3D; alturas propuestas. Cabezal sin instalaciones.


Dimensiones y capacidades de conductores, protecciones y puesta a tierra pendientes de cálculo.

Baños y exterior: posición, protección y equipo apropiado por validar.

# E-02L · Iluminación y mandos · Planta alta

CASA LALES · MAPA COMPLETO · ESCALA 1:40 · IMPRIMIR AL 100 %

Revisión 12/11/2026 · 2212a8f4

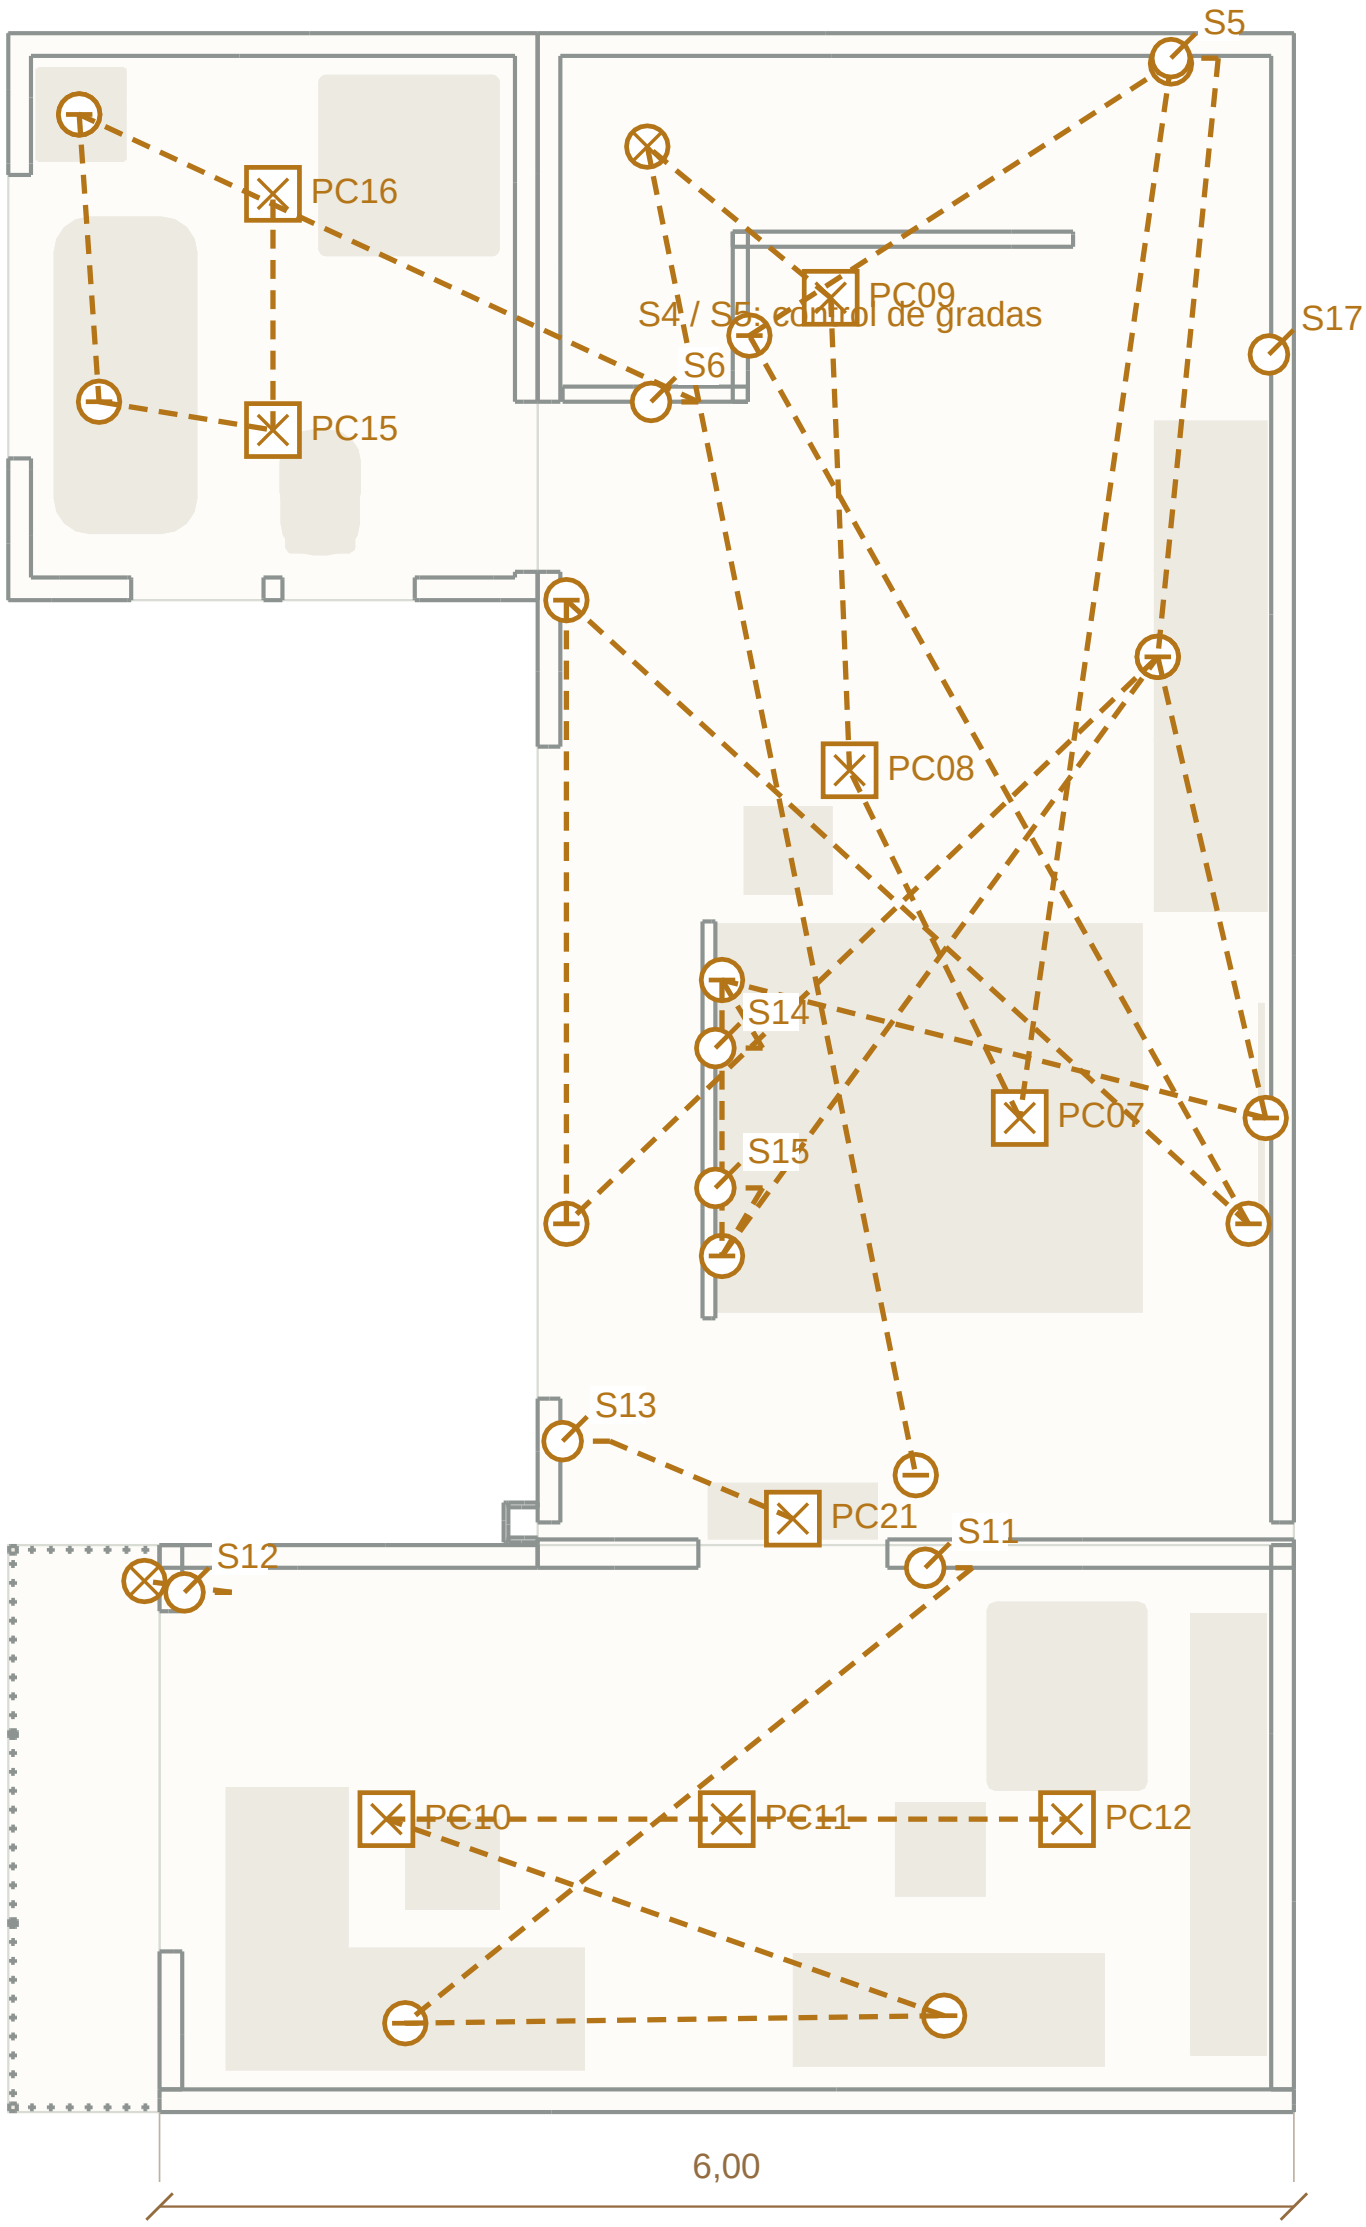


FRENTE ABAJO · RECORRIDOS PROPUESTOS

Simbología y notas en la hoja siguiente.

# EXPLICACIÓN · E-02L

Iluminación y mandos · Planta alta

Casa Lales · Revisión 12/11/2026 · 2212a8f4

## QUÉ SIGNIFICA CADA FIGURA

**Cuadrado con X · plafón PC**
Lámpara cuadrada de sobreponer. Cada código PC identifica una unidad; potencia y temperatura en el cuadro de esta hoja.

**Círculo con X · luz general**
Punto de iluminación general del modelo. No equivale siempre a una unidad comercial.

**Círculo con raya · luz de apoyo**
Referencia de trabajo o ambiente: LED, espejo, mueble, aplique o escalón.

**Círculo con trazo · S**
Interruptor o caja de teclas. Misma posición y código que el visor; S4/S5 coordinan las gradas.

**Línea punteada · relación de mando**
Relaciona el mando con sus luces. No fija un cableado, conductores ni trayecto de ejecución.

**Líneas grises · muro**
Paredes del modelo como referencia para situar los puntos.

**Figura beige · mueble o aparato**
Huella de referencia; se conservan las posiciones del modelo.

## DATOS Y CRITERIOS DEL PLANO

**Iluminación general: 9 plafones PC / 2 otros**
Cuadrado con X: plafón PC; círculo con X: otra luz general.

**Luz de trabajo / ambiente: 16 referencias**
Círculo con raya; incluye LED, apliques y apoyos.

**Cajas de mandos: S5, S17, S6, S13, S14, S15, S11, S12**
S4/S5: coordinar el control de gradas desde ambos niveles.

**Plano de tomacorrientes: E-02T**
Consultar su mapa independiente; no se representan aquí sus símbolos.

**Dormitorio y armarios: 3 × 24 W · 3000 K**
Interior seco

**Estudio: 3 × 24 W · 4000 K**
Interior seco

**Baño principal: 2 × 18 W · 4000 K**
Eternit hacia casa; inclinación 12,14% en boceto. Cielo libre 2,20 m. Producto y solución de baja pendiente por confirmar.

**Acceso al estudio: 1 × 12 W · 3000 K**
Interior seco

## NOTAS PARA REVISIÓN EN OBRA

Mismas tomas y mandos que en imágenes 3D. Alturas propuestas; dormitorio según distribución aplicada.

Líneas punteadas: relación de mando y recorrido conceptual; no son número de conductores.

Grupos C01-C12 funcionales: dividir por planta, cargas y protecciones en cálculo. Tablero y tierra pendientes.

Bajo Eternit: canalización y cajas fijadas a soporte definido, nunca a las planchas.

Las luces de gradas se asignan a PB o PA por cota: cada referencia aparece una sola vez.

PC: plafón cuadrado sobrepuesto. Modelo seco de referencia 28,5 × 28,5 × 2,8 cm, 24 W, 1800 lm, 0,583 kg; 100–240 V. Confirmar equipo y suministro.

Fijar herraje a perfil/refuerzo del cielo; no cargar sólo la placa. Revisar perfilería, anclaje y acceso al driver; no suspender del Eternit.


Baños: variante sellada IP44 mínimo; IP65 si la zona lo exige. Potencia y formato menores orientativos; modelo y protección por elegir.

Plafón de referencia sin dimmer. LED indirecto y tarea separados. Cantidad propuesta; verificar iluminación con fotometría y medidas reales.

# E-03T · Tomacorrientes y equipos · Patio

CASA LALES · MAPA COMPLETO · ESCALA 1:40 · IMPRIMIR AL 100 %

Revisión 12/11/2026 · 2212a8f4

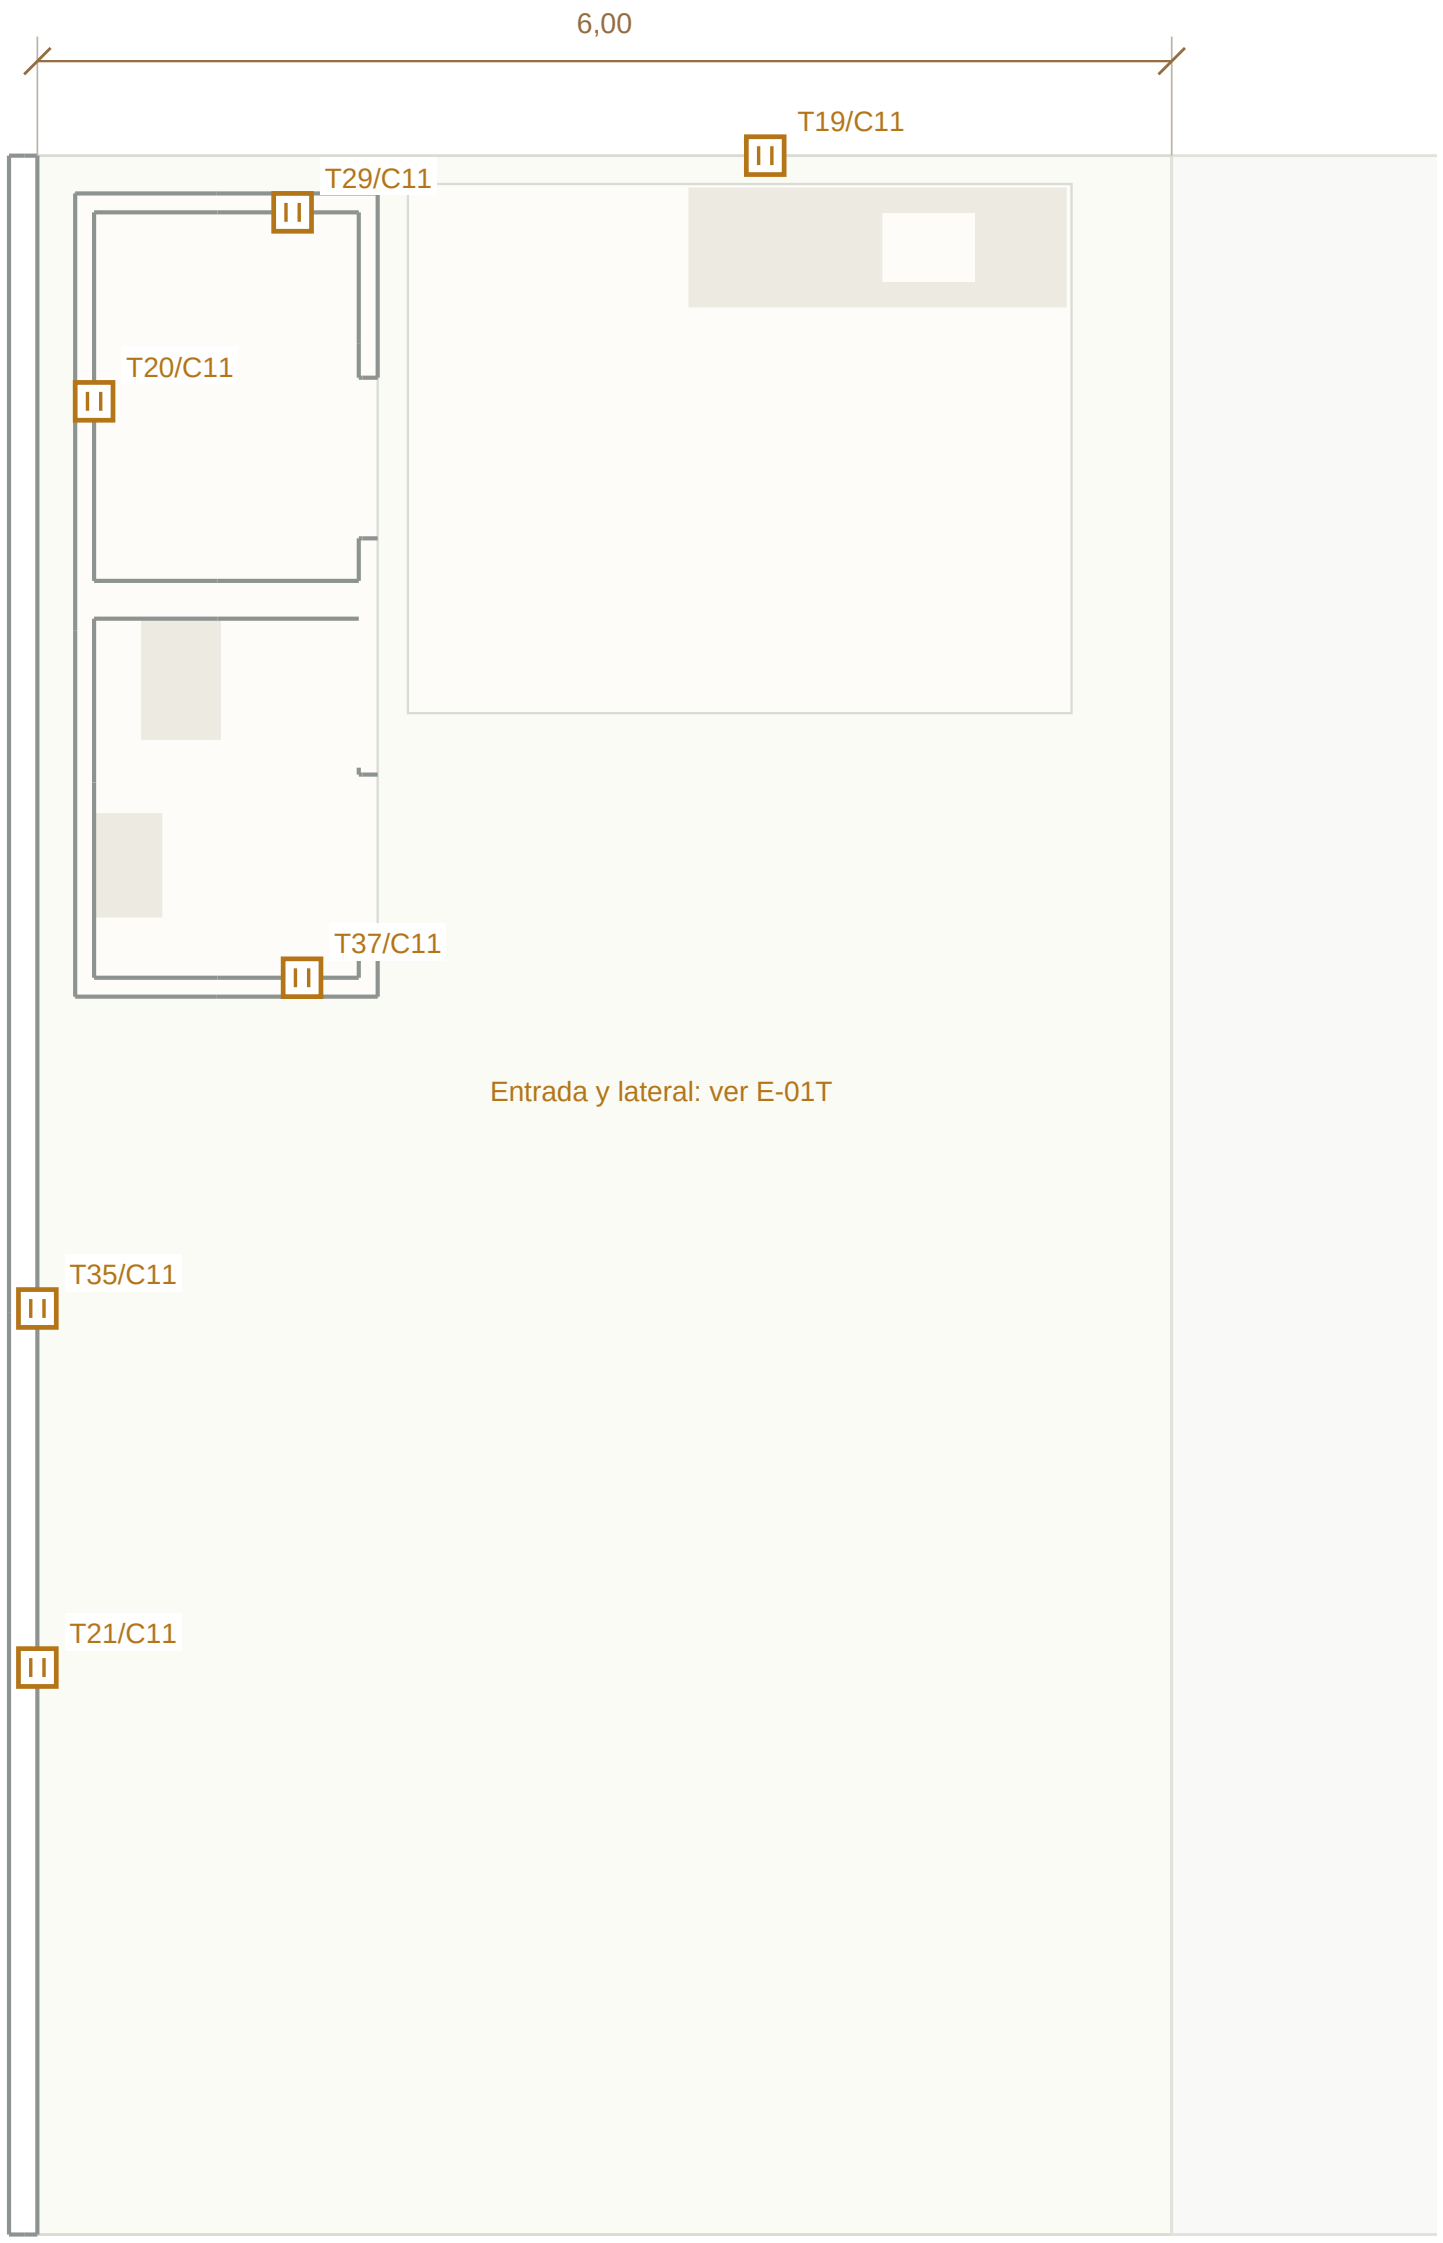


FRENTE ABAJO · RECORRIDOS PROPUESTOS

Simbología y notas en la hoja siguiente.

# EXPLICACIÓN · E-03T

Tomacorrientes y equipos · Patio

Casa Lales · Revisión 12/11/2026 · 2212a8f4

## QUÉ SIGNIFICA CADA FIGURA



**Cuadrado con dos rayas · T**

Tomacorriente. Código T y grupo C coinciden con el visor 3D; no indican voltaje ni amperaje.

C01

**C04-C11 · grupo funcional**

El sufijo /C identifica un uso propuesto, sujeto al cálculo de cargas y protecciones.



**Líneas grises · muro**

Paredes del modelo como referencia para situar los puntos.



**Figura beige · mueble o aparato**

Huella de referencia; se conservan las posiciones del modelo.

## DATOS Y CRITERIOS DEL PLANO

**Tomacorrientes: 6 puntos**

Códigos T conservados. /C identifica grupo funcional; no es voltaje ni capacidad.

**Reservas de equipos: 0 cajas**

No hay cajas EQ adicionales en este nivel.

**Plano de luces y mandos: E-03L**

Consultar su mapa independiente; no se representan aquí sus símbolos.

## NOTAS PARA REVISIÓN EN OBRA

Mismas posiciones y códigos que en imágenes 3D; alturas propuestas. Cabezal sin instalaciones.


Dimensiones y capacidades de conductores, protecciones y puesta a tierra pendientes de cálculo.

Baños y exterior: posición, protección y equipo apropiado por validar.

# E-03L · Iluminación y mandos · Patio

CASA LALES · MAPA COMPLETO · ESCALA 1:40 · IMPRIMIR AL 100 %

Revisión 12/11/2026 · 2212a8f4

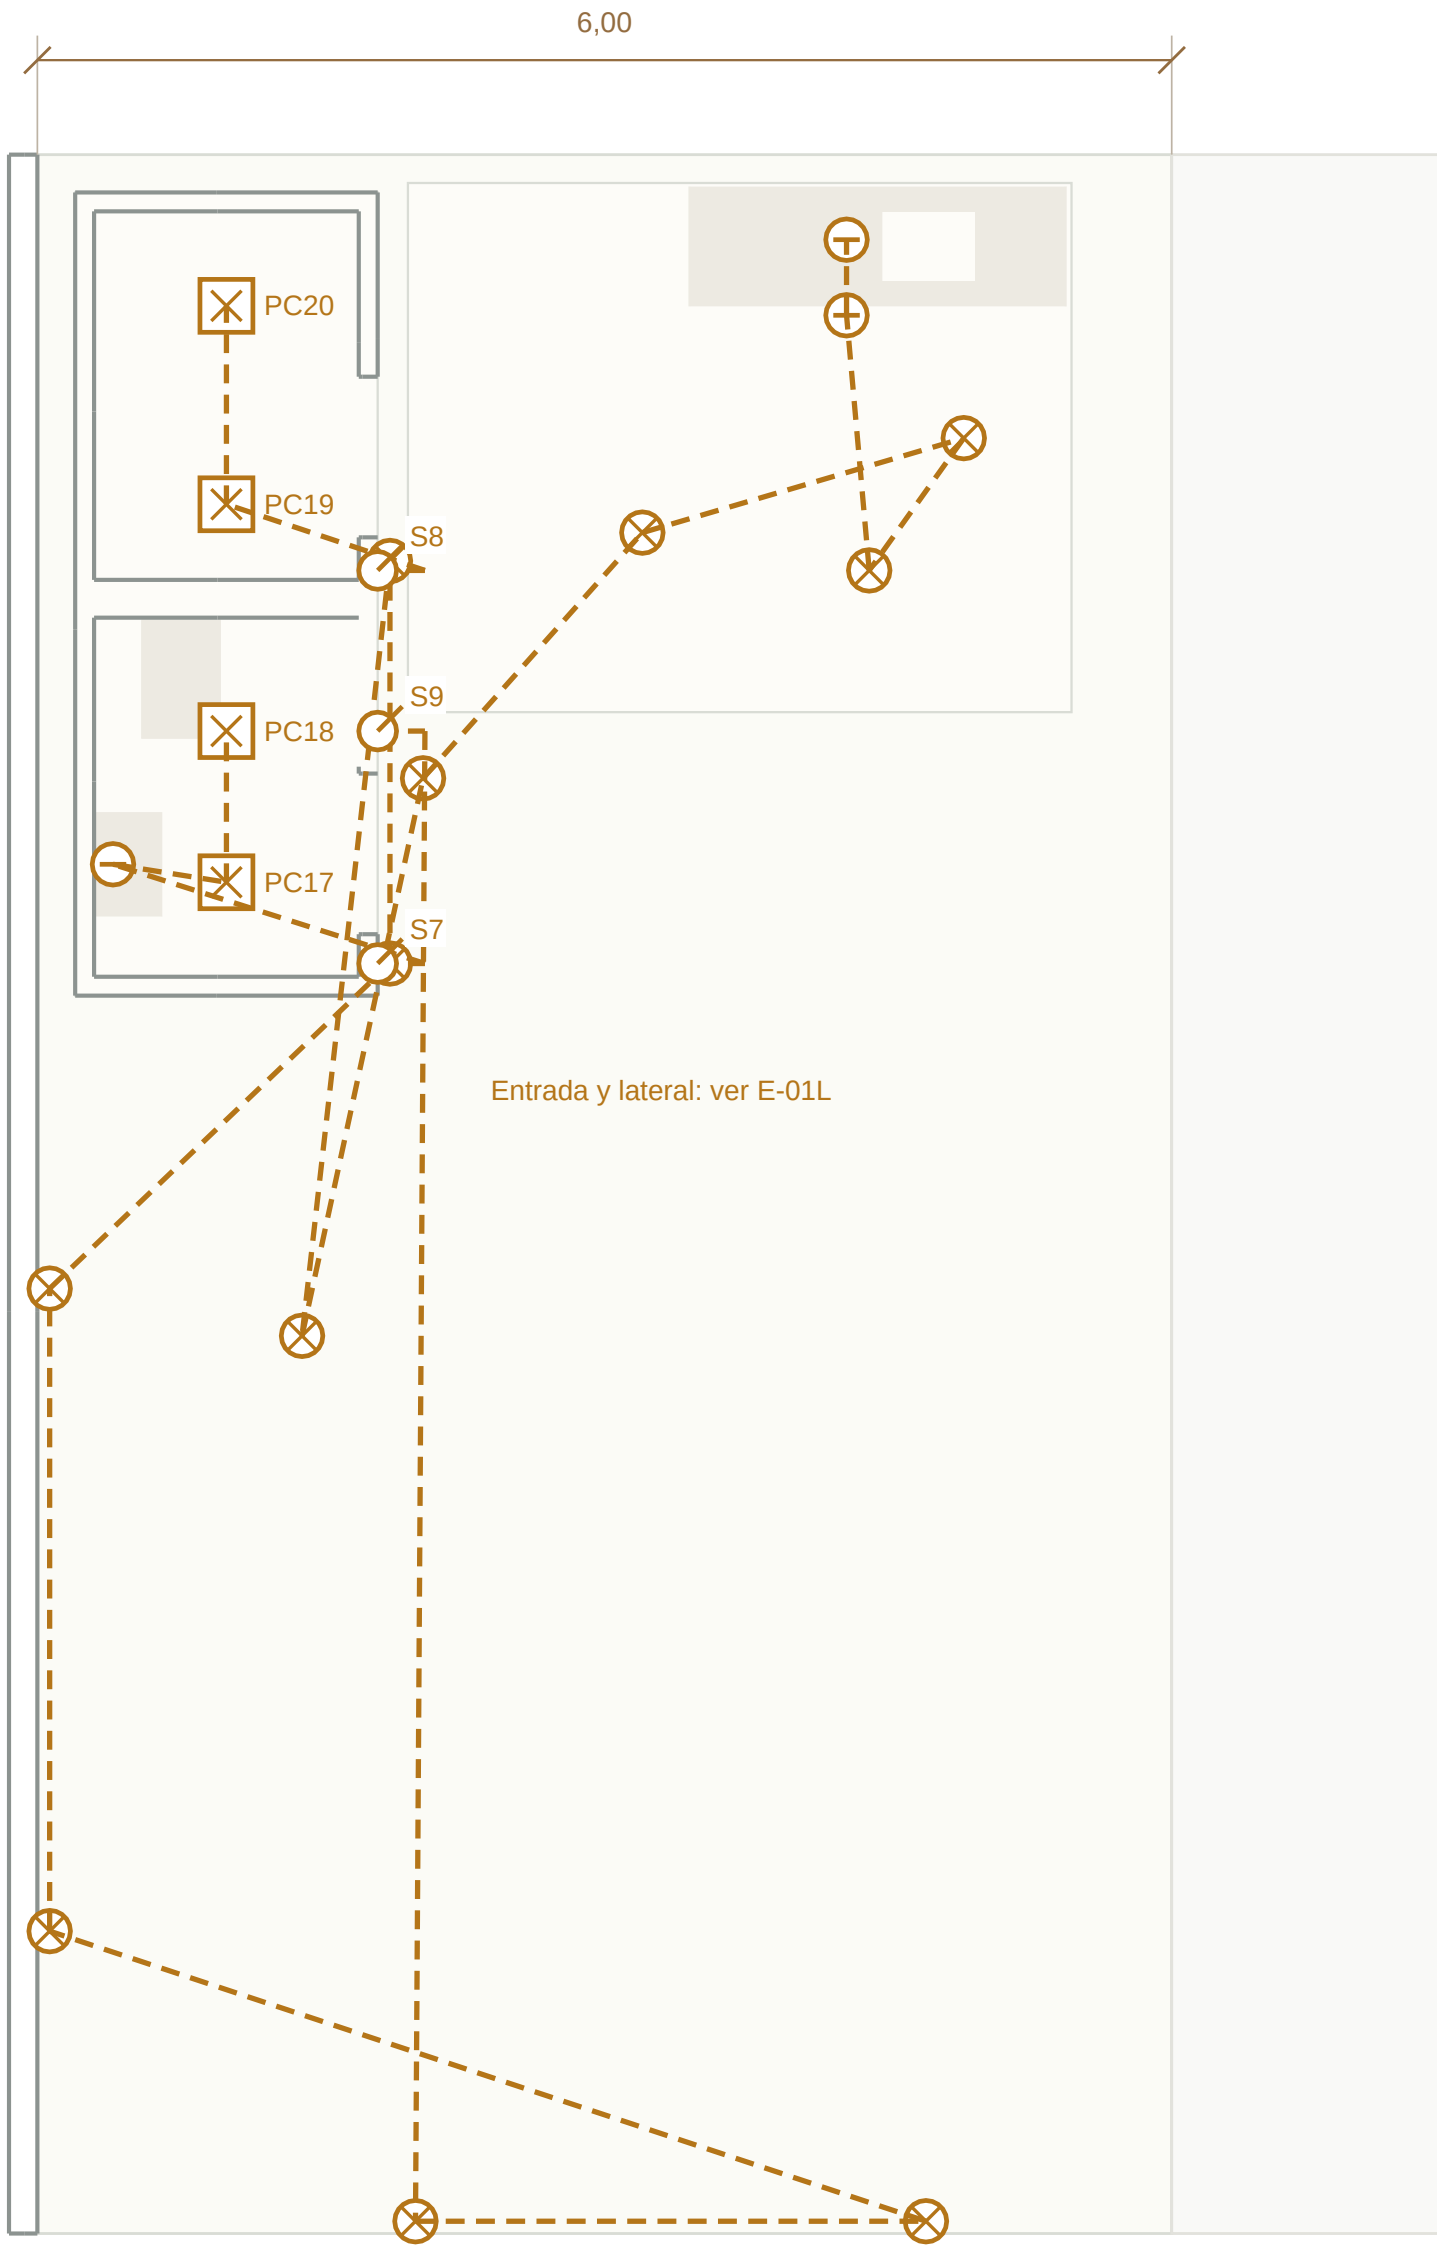


FRENTE ABAJO · RECORRIDOS PROPUESTOS

Simbología y notas en la hoja siguiente.

# EXPLICACIÓN · E-03L

Iluminación y mandos · Patio

Casa Lales · Revisión 12/11/2026 · 2212a8f4

## QUÉ SIGNIFICA CADA FIGURA

**Cuadrado con X · plafón PC**
Lámpara cuadrada de sobreponer. Cada código PC identifica una unidad; potencia y temperatura en el cuadro de esta hoja.

**Círculo con X · luz general**
Punto de iluminación general del modelo. No equivale siempre a una unidad comercial.

**Círculo con raya · luz de apoyo**
Referencia de trabajo o ambiente: LED, espejo, mueble, aplique o escalón.

**Círculo con trazo · S**
Interruptor o caja de teclas. Misma posición y código que el visor; S4/S5 coordinan las gradas.

**Línea punteada · relación de mando**
Relaciona el mando con sus luces. No fija un cableado, conductores ni trayecto de ejecución.

**Líneas grises · muro**
Paredes del modelo como referencia para situar los puntos.

**Figura beige · mueble o aparato**
Huella de referencia; se conservan las posiciones del modelo.

## DATOS Y CRITERIOS DEL PLANO

**Iluminación general: 4 plafones PC / 11 otros**
Cuadrado con X: plafón PC; círculo con X: otra luz general.

**Luz de trabajo / ambiente: 3 referencias**
Círculo con raya; incluye LED, apliques y apoyos.

**Cajas de mandos: S7, S8, S9**
S4/S5: coordinar el control de gradas desde ambos niveles.

**Plano de tomacorrientes: E-03T**
Consultar su mapa independiente; no se representan aquí sus símbolos.

**Baño del patio: 2 × 12 W · 4000 K**
Sellado para zona húmeda; por confirmar

**Bodega: 2 × 12 W · 4000 K**
Interior seco

## NOTAS PARA REVISIÓN EN OBRA

Mismas tomas y mandos que en imágenes 3D. Alturas propuestas; dormitorio según distribución aplicada.

Líneas punteadas: relación de mando y recorrido conceptual; no son número de conductores.

Grupos C01-C12 funcionales: dividir por planta, cargas y protecciones en cálculo. Tablero y tierra pendientes.

Bajo Eternit: canalización y cajas fijadas a soporte definido, nunca a las planchas.

Las luces de gradas se asignan a PB o PA por cota: cada referencia aparece una sola vez.

PC: plafón cuadrado sobrepuesto. Modelo seco de referencia 28,5 × 28,5 × 2,8 cm, 24 W, 1800 lm, 0,583 kg; 100–240 V. Confirmar equipo y suministro.

Fijar herraje a perfil/refuerzo del cielo; no cargar sólo la placa. Revisar perfilería, anclaje y acceso al driver; no suspender del Eternit.


Baños: variante sellada IP44 mínimo; IP65 si la zona lo exige. Potencia y formato menores orientativos; modelo y protección por elegir.

Plafón de referencia sin dimmer. LED indirecto y tarea separados. Cantidad propuesta; verificar iluminación con fotometría y medidas reales.

# H-01 · Agua fría y caliente · PB y patio

CASA LALES · MAPA COMPLETO · ESCALA 1:60 · IMPRIMIR AL 100 %

Revisión 12/11/2026 · 2212a8f4

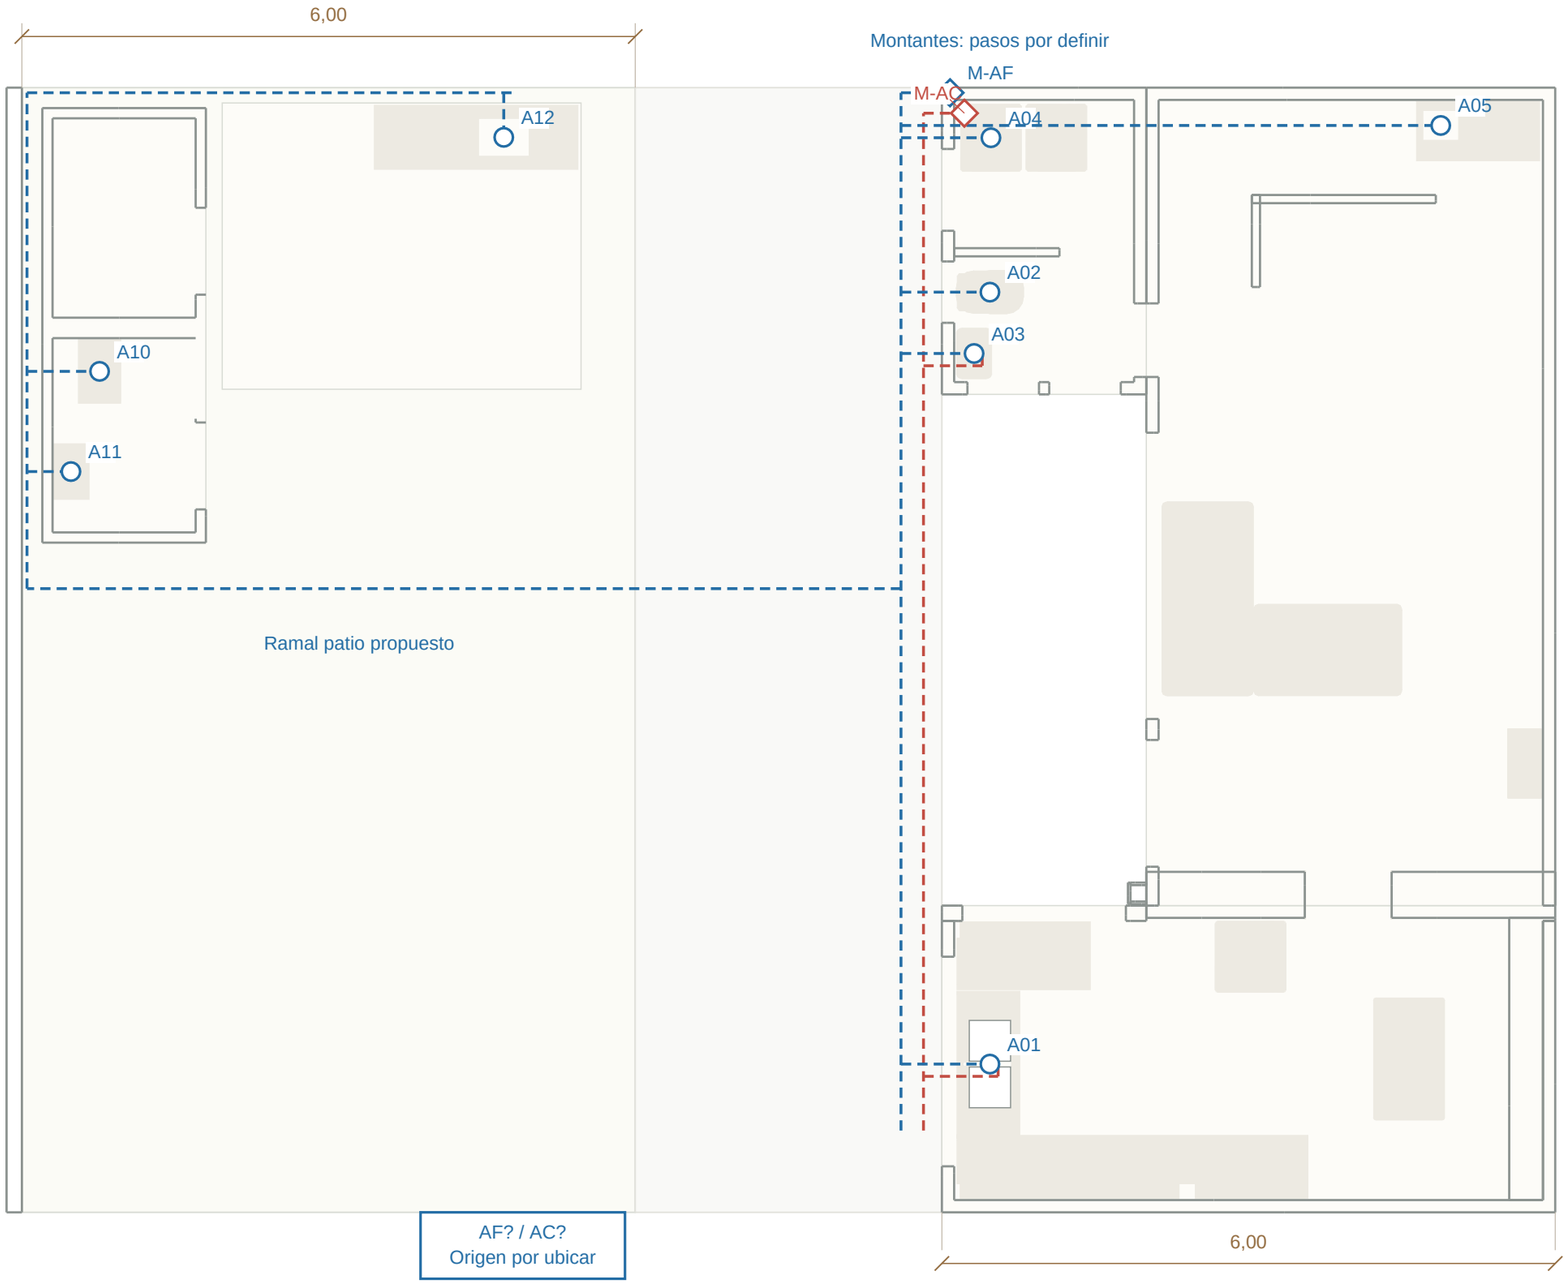



FRENTE ABAJO · RECORRIDOS PROPUESTOS

# H-02 · Agua fría y caliente · planta alta

CASA LALES · MAPA COMPLETO · ESCALA 1:40 · IMPRIMIR AL 100 %

Revisión 12/11/2026 · 2212a8f4

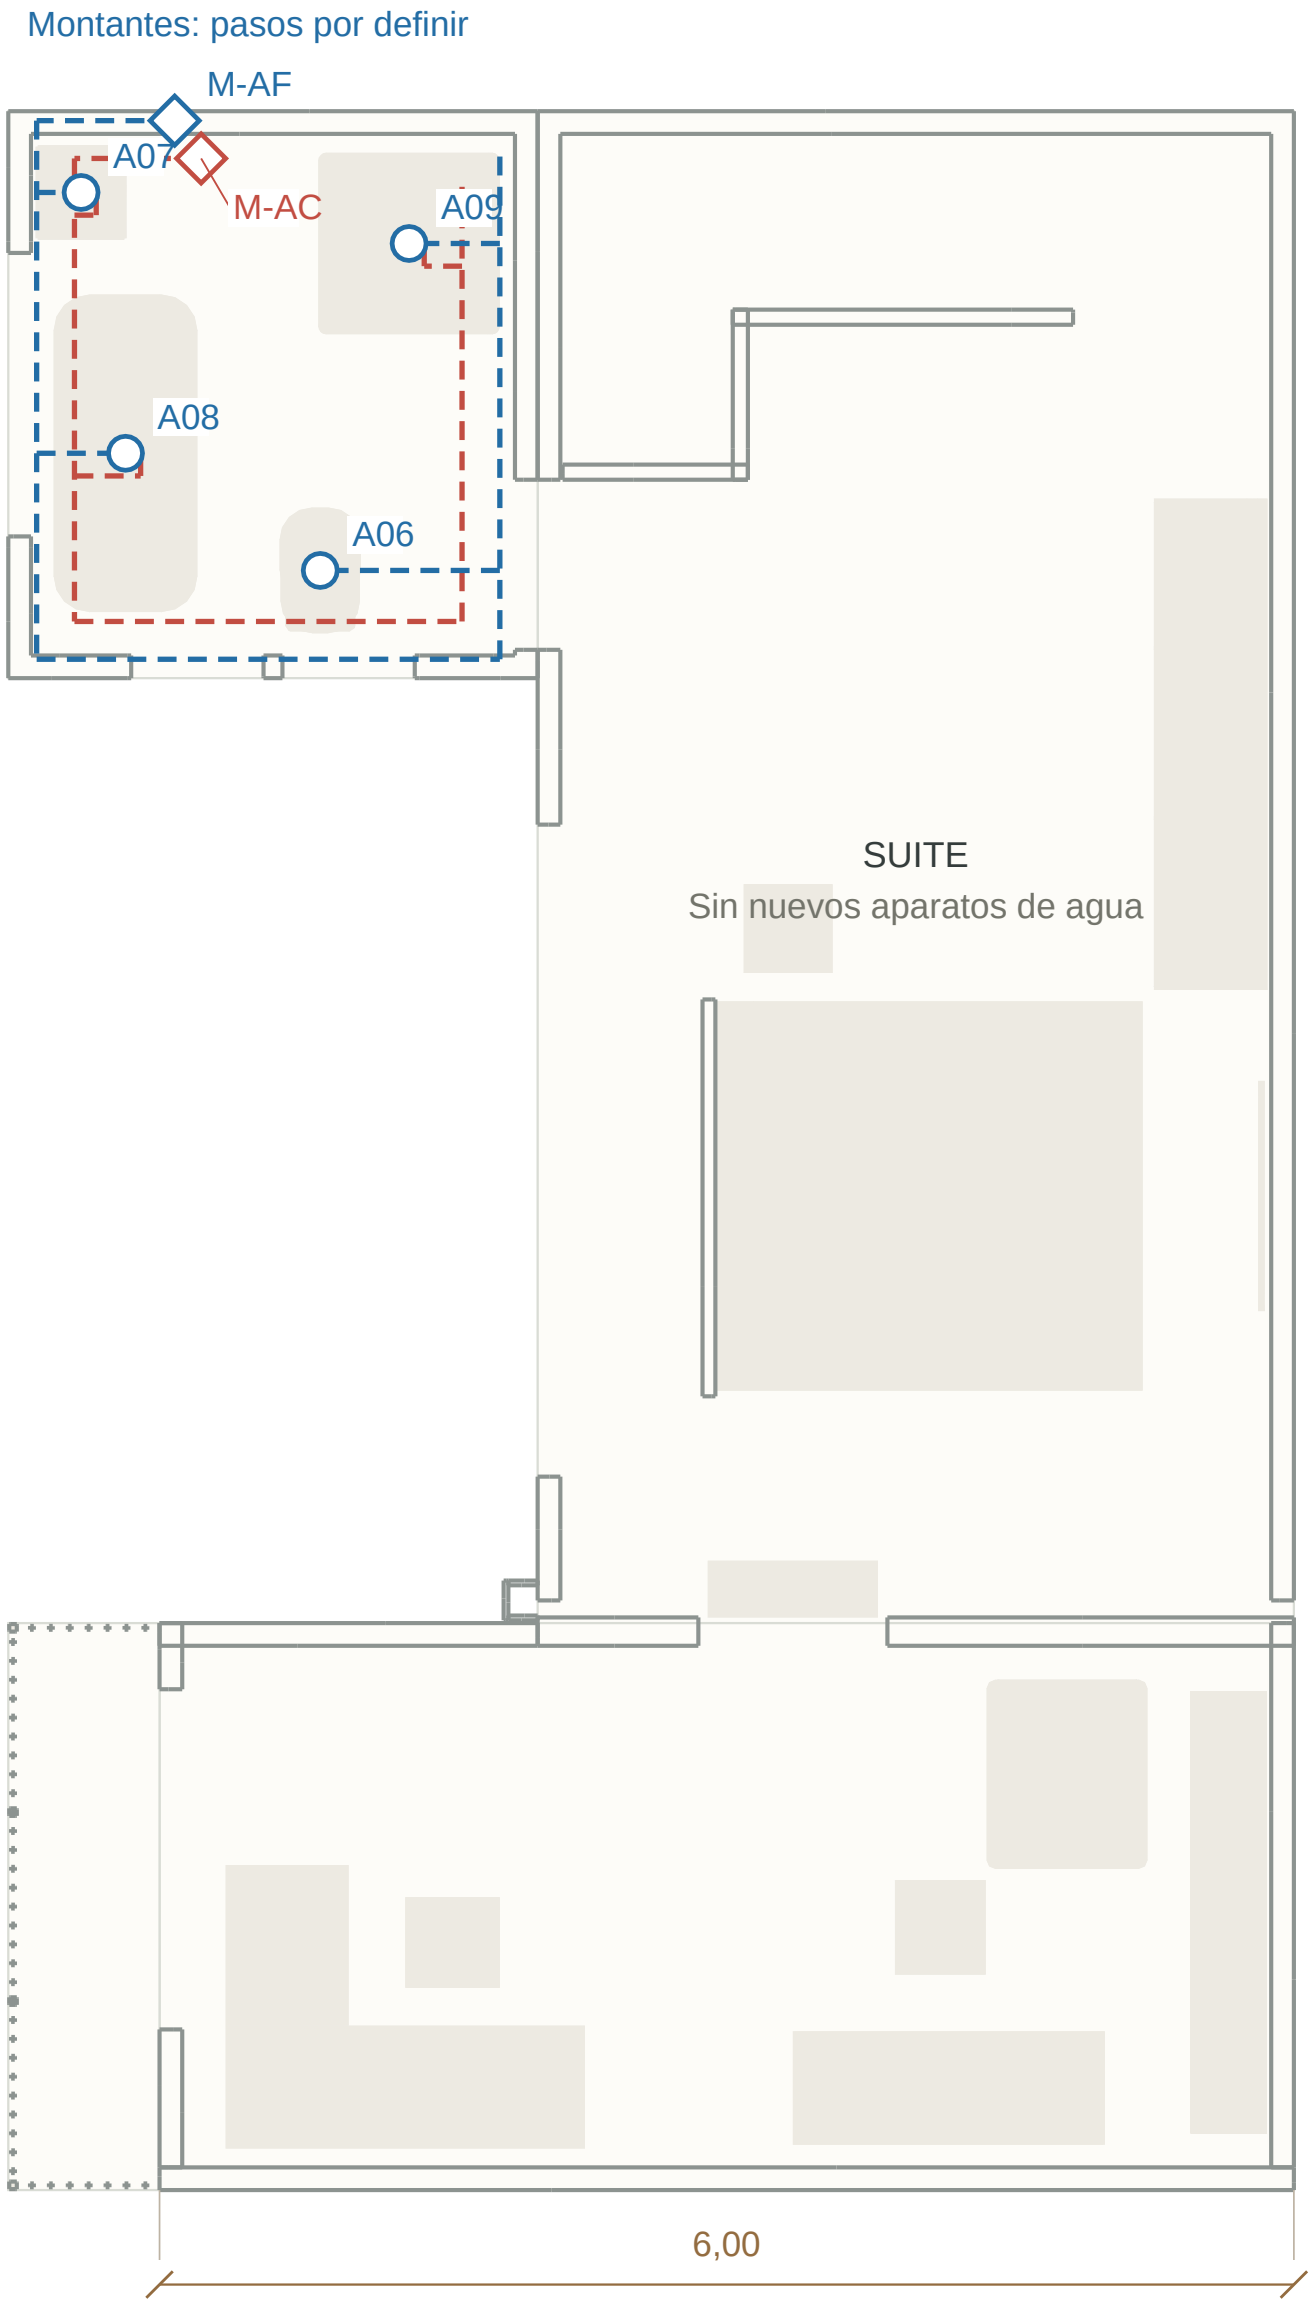



FRENTE ABAJO · RECORRIDOS PROPUESTOS

# S-01 · Desagües y ventilación · PB y patio

CASA LALES · MAPA COMPLETO · ESCALA 1:60 · IMPRIMIR AL 100 %

Revisión 12/11/2026 · 2212a8f4

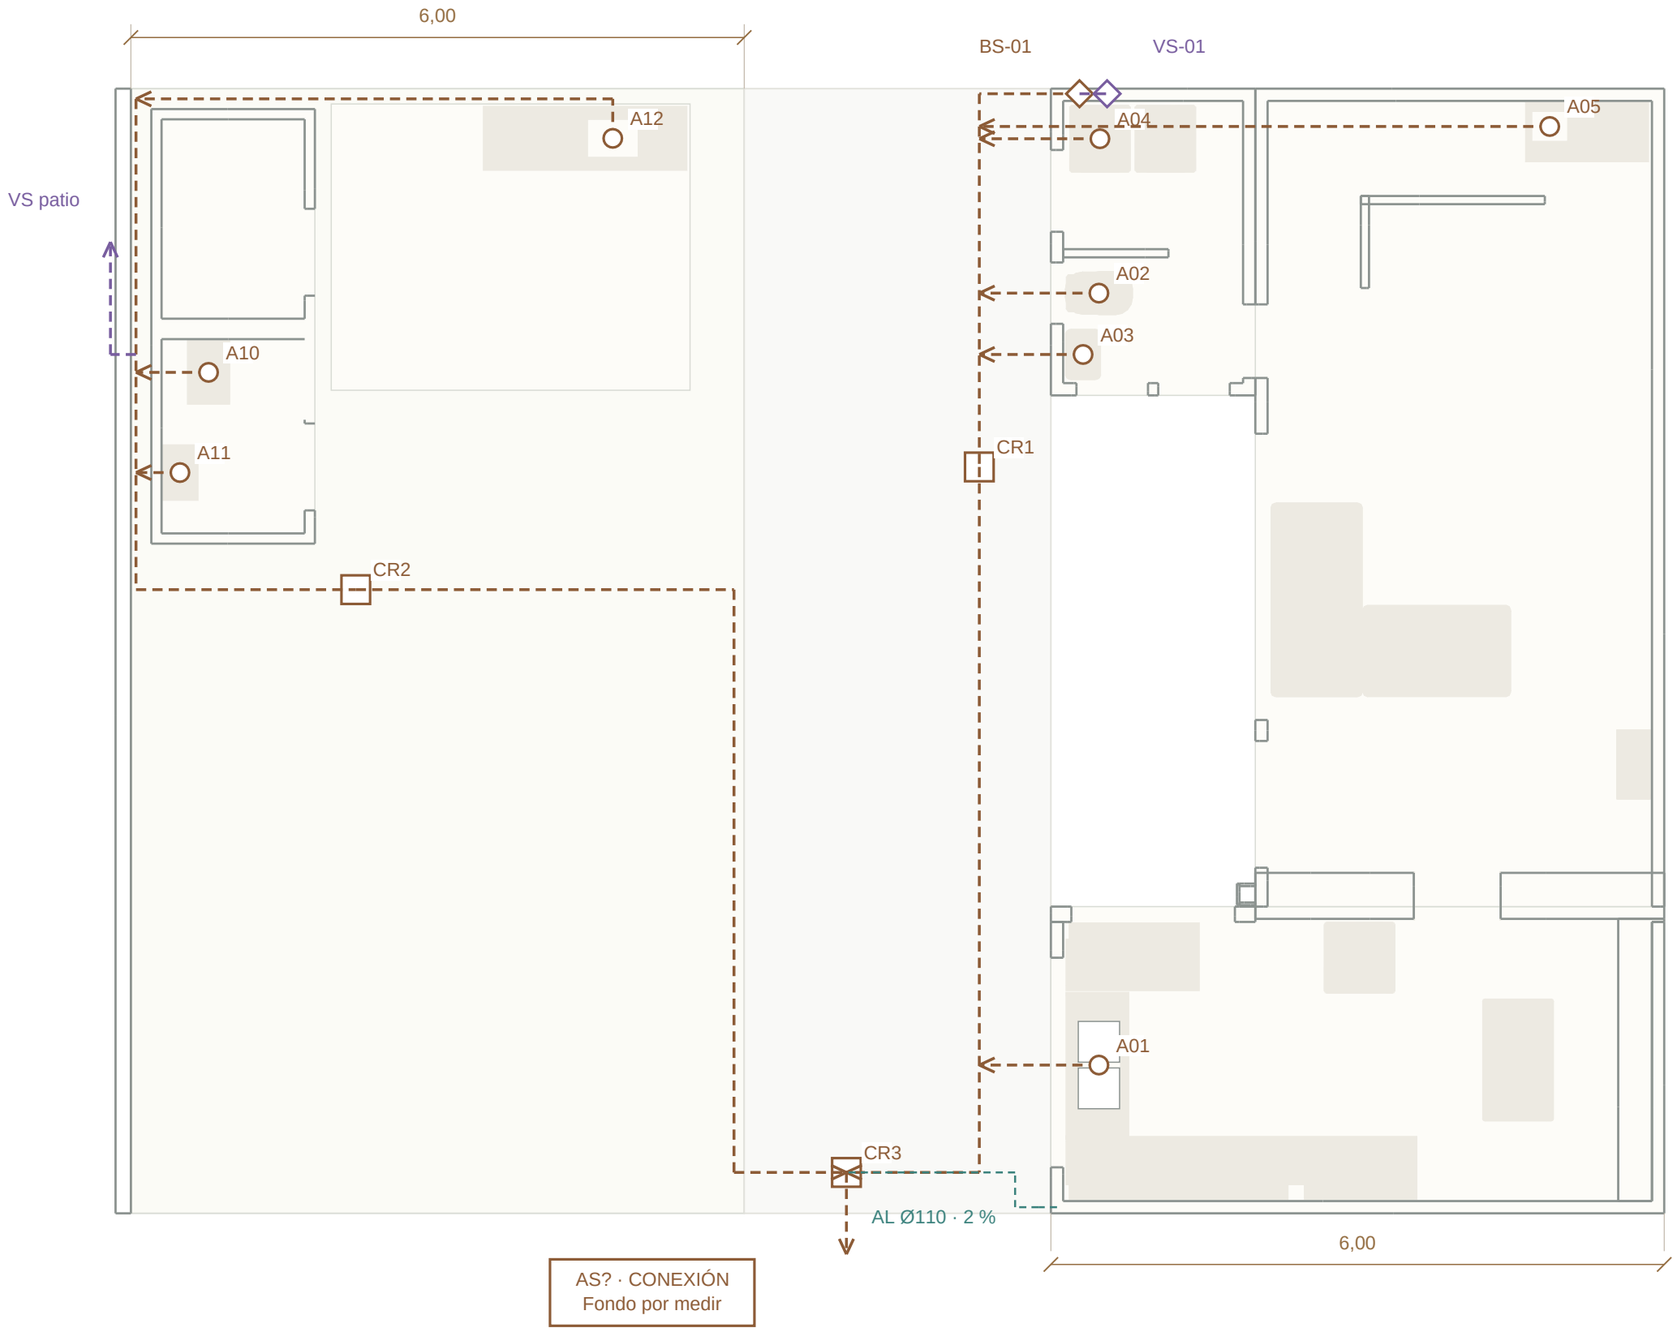



FRENTE ABAJO · RECORRIDOS PROPUESTOS

# S-02 · Desagües y ventilación · planta alta

CASA LALES · MAPA COMPLETO · ESCALA 1:40 · IMPRIMIR AL 100 %

Revisión 12/11/2026 · 2212a8f4

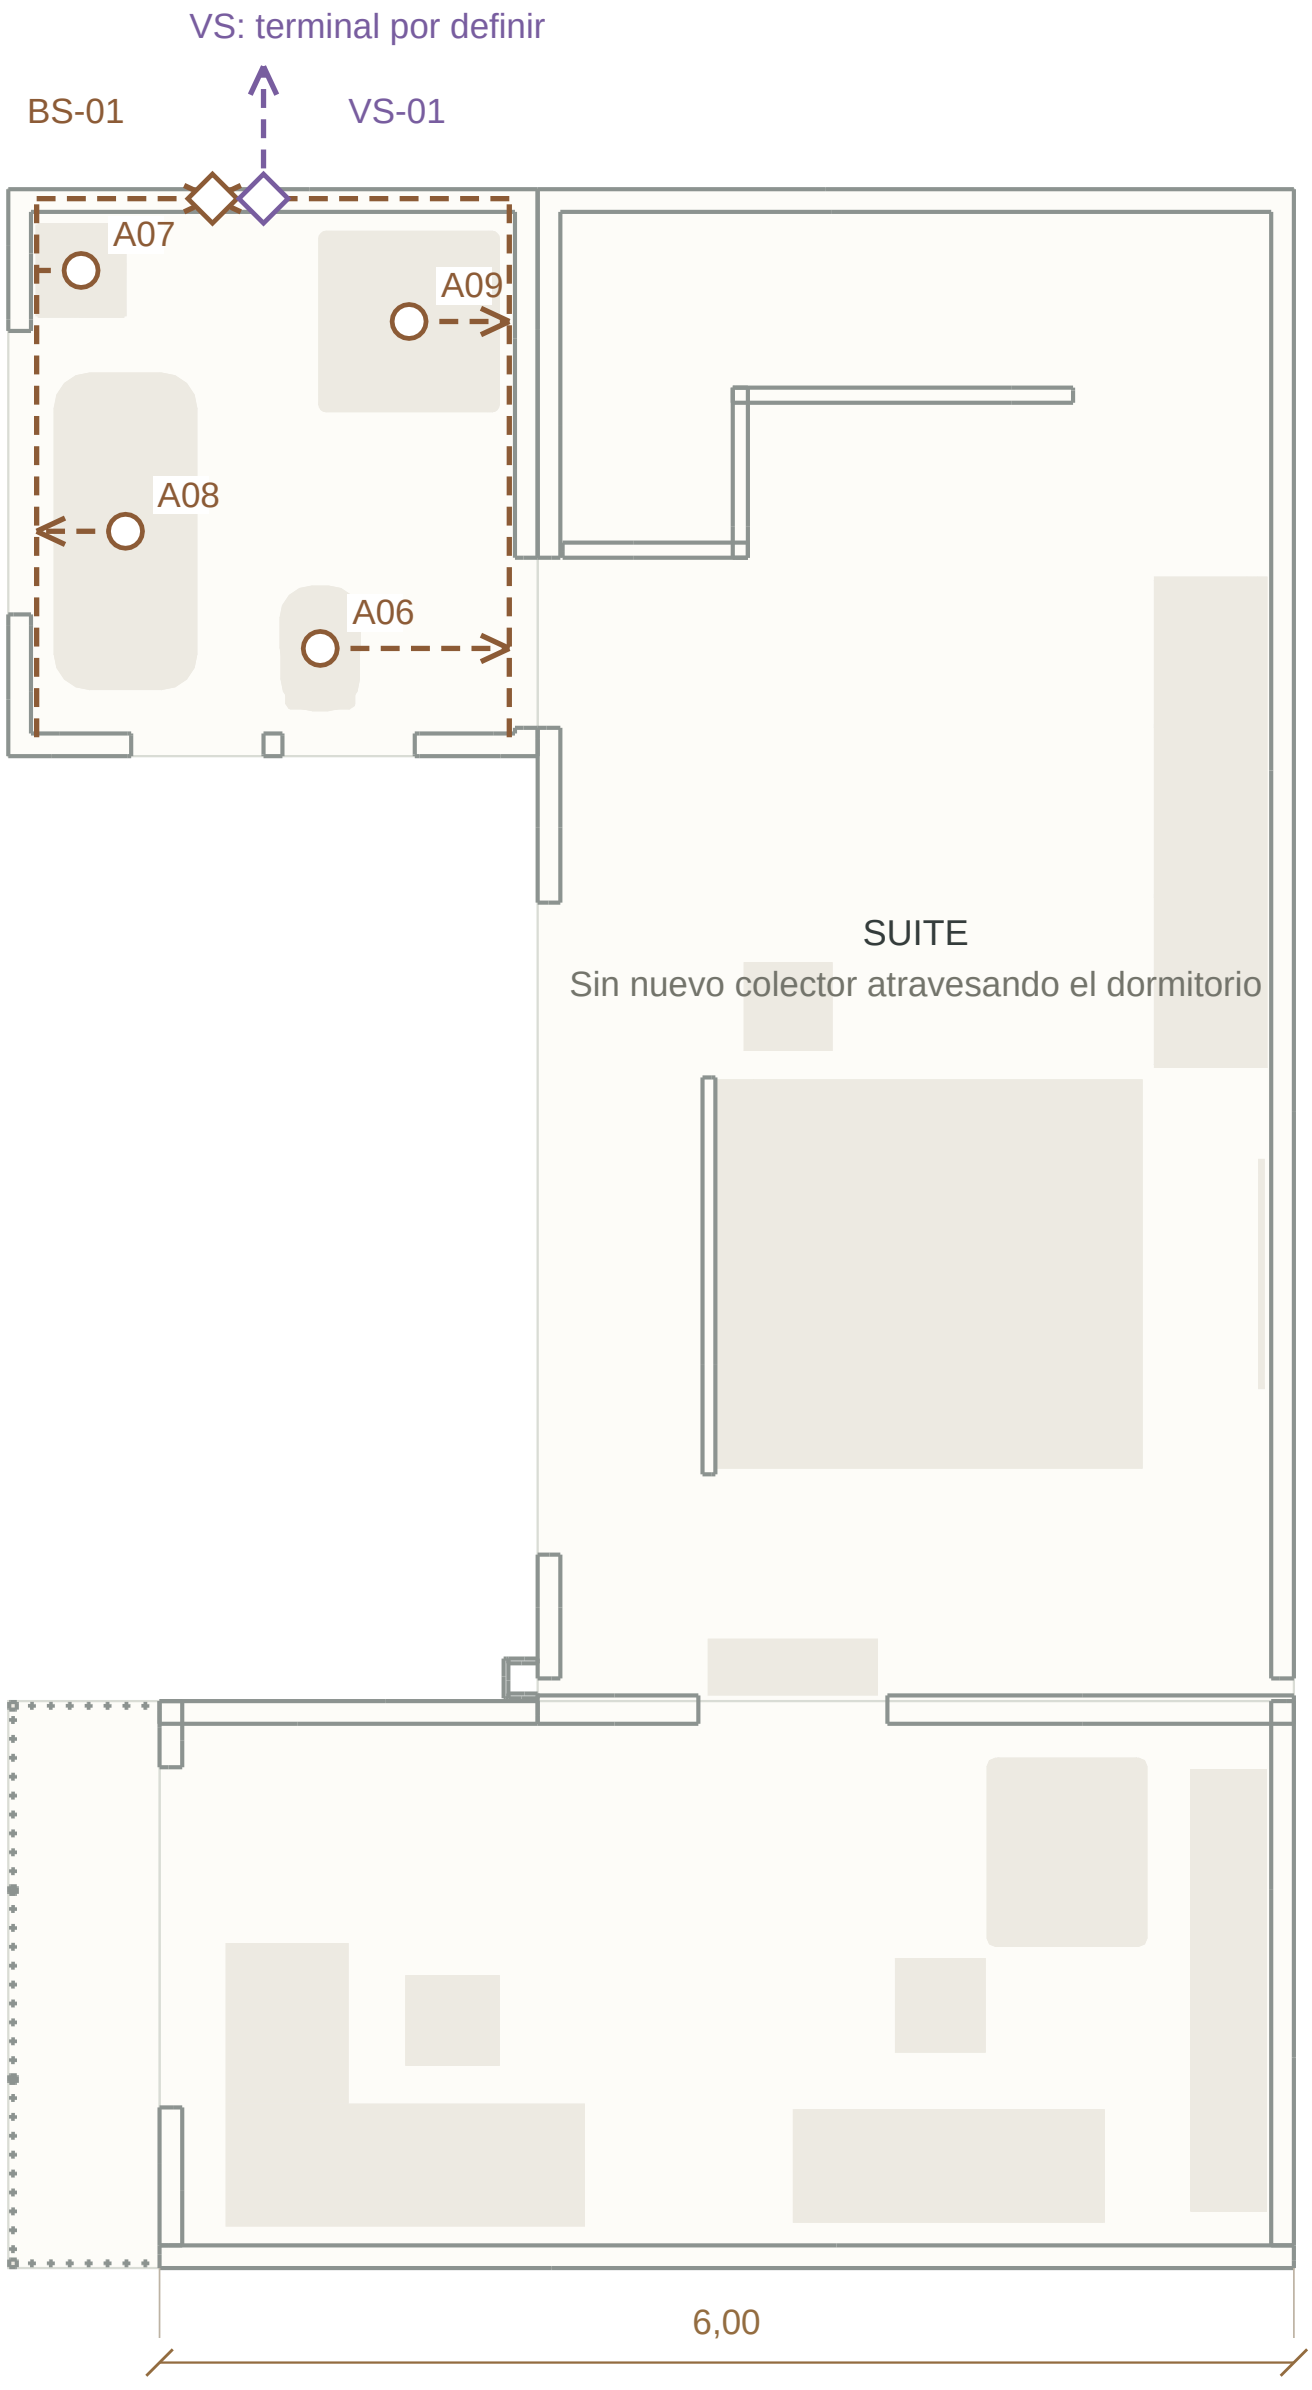


FRENTE ABAJO · RECORRIDOS PROPUESTOS

# A-07 · Medidas y alturas confirmadas por el usuario

CASA LALES · MAPA COMPLETO · ESCALA 1:40 · IMPRIMIR AL 100 %


Revisión 12/11/2026 · 2212a8f4

| ESPACIO | MEDIDAS m | ÁREA m² | ALTURA m |
|---|---|---|---|
| Sala, bloque completo | 4,00 × 8,00 | 32,00 | 2,10 |
| Cocina y comedor | 6,00 × 3,00 | 18,00 | 2,20 |
| Baño social con lavandería | 2,00 × 3,00 | 6,00 | 2,10 |
| Dormitorio, bloque completo | 4,00 × 8,00 | 32,00 | 2,10 |
| Baño principal | 2,80 × 3,00 | 8,40 | 2,20 |
| Estudio sobre cocina | 6,00 × 3,00 | 18,00 | 2,20 |
| Balcón del estudio | 0,80 × 3,00 | 2,40 | Pretil 1,10 |
| Baño del patio, interior libre | 1,40 × 1,90 | 2,66 | 3,50 - 3,58 |
| Bodega del patio, interior libre | 1,40 × 1,95 | 2,73 | 3,50 - 3,60 |
| Área del asadero | 3,51 × 2,80 | 9,83 | 3,33 - 3,51 |
| Patio completo | 6,00 × 11,00 | 66,00 | Abierto |

## A-09 · Baño principal · Losa propuesta y encuentro de alturas

CASA LALES · MAPA COMPLETO · ESCALA 1:25 · IMPRIMIR AL 100 %

Revisión 12/11/2026 · 2212a8f4

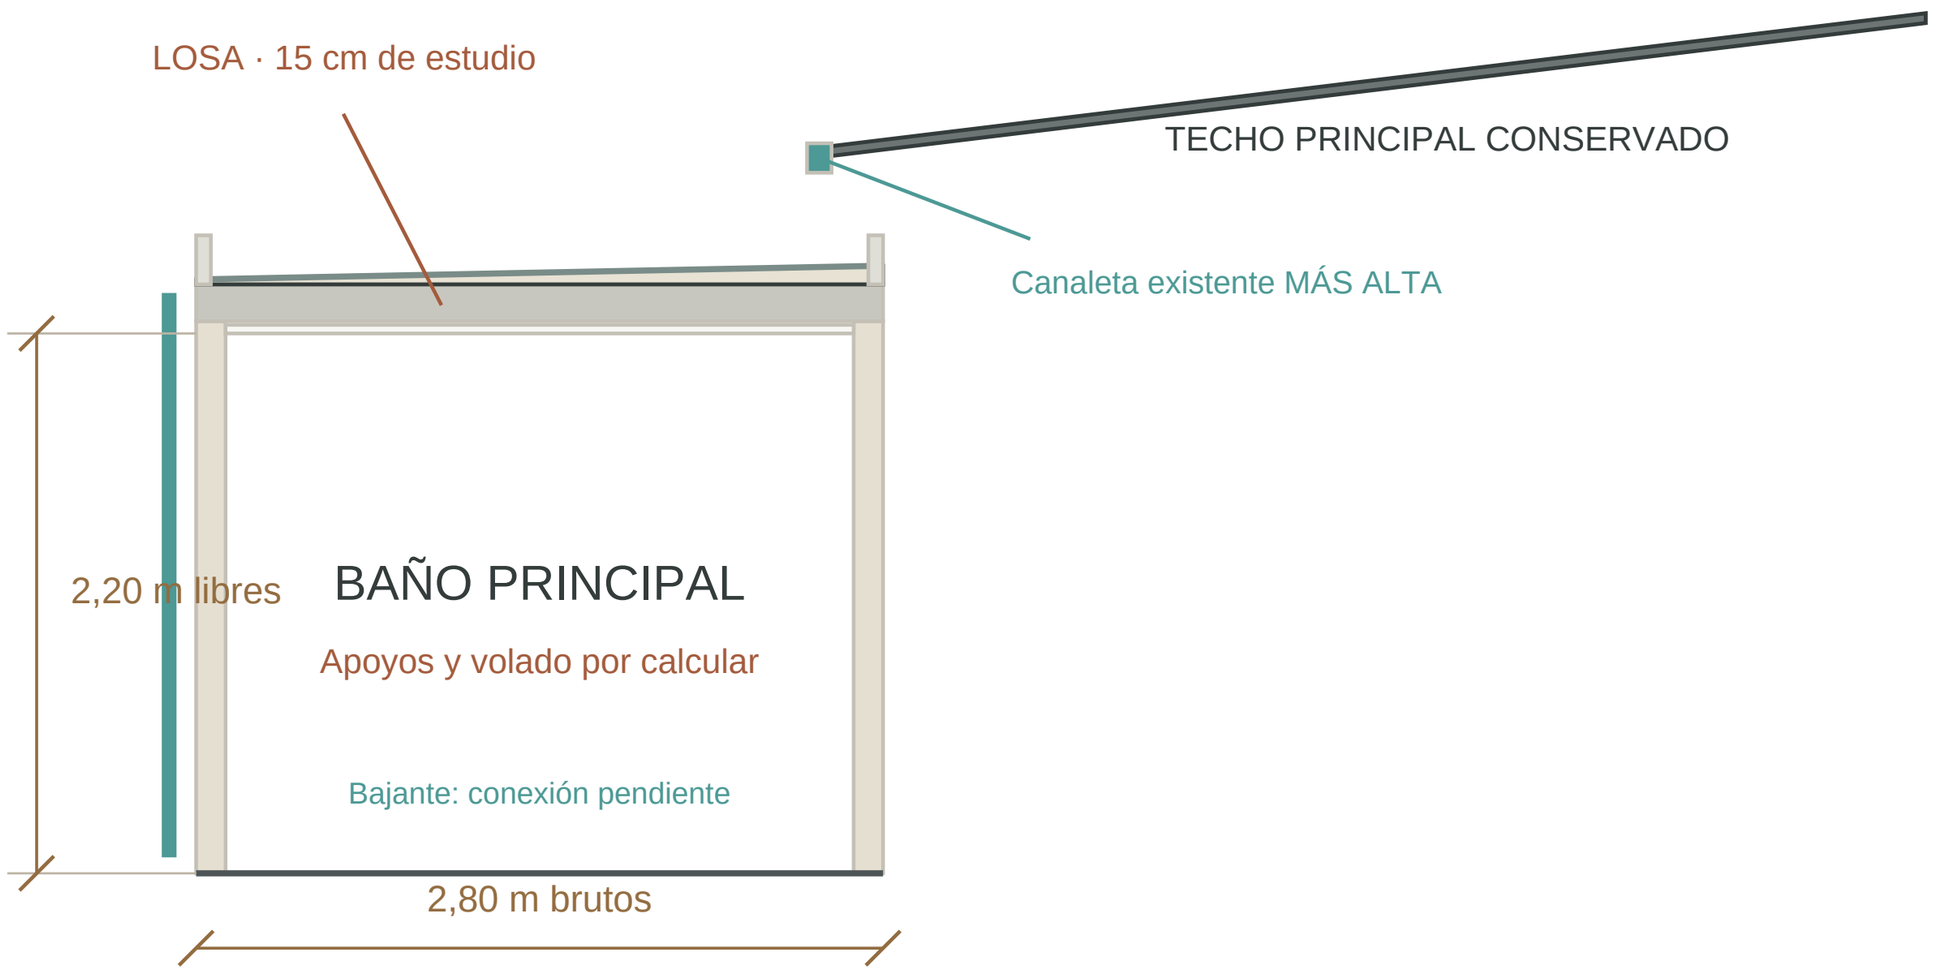

Revisión 12/11/2026 · 2212a8f4 | Modelo y propuesta de coordinación - comprobar en sitio

## HUECOS, PUERTAS Y PASOS - MEDIDAS DEL MODELO

| IDENTIFICACIÓN | NIVEL | ANCHO m | ALTO m | COTA INFERIOR m |
|---|---|---|---|---|
| Acceso al baño principal | PA | 0,90 | 2,10 | 2,30 |
| Entrada · 1,10 libre / hoja 1,15 x 2,10 | PB | 1,24 | 2,15 | 0,00 |
| Sala · ventanal hacia el patio | PB | 2,80 | 1,20 | 0,65 |
| Social · frente, lado izquierdo | PB | 0,70 | 0,60 | 1,22 |
| Social · frente, lado derecho | PB | 0,70 | 0,60 | 1,22 |
| Principal · frente, lado izquierdo | PA | 0,70 | 0,60 | 3,56 |
| Principal · frente, lado derecho | PA | 0,70 | 0,60 | 3,56 |
| Principal · ventana hacia calle | PA | 1,50 | 0,75 | 3,44 |
| Dormitorio · ventanal hacia patio | PA | 3,45 | 1,40 | 3,00 |
| Cocina · ventana hacia calle | PB | 2,05 | 0,85 | 1,10 |
| Cocina · ventana de retorno | PB | 1,60 | 0,85 | 1,10 |
| Baño social (hoja 0,70 x 1,95) | PB | 0,72 | 1,98 | 0,00 |
| Acceso al estudio · Dos subidas rectas17,5cm | PA | 1,00 | 2,20 | 2,65 |
| Paso cocina sin hoja · luz útil | PB | 0,826 | 1,935 | 0,00 |
| Estudio · corredera al balcón | PA | 1,80 | 2,10 | 2,65 |
| Baño social · ventana a calle | PB | 0,60 | 0,75 | 1,10 |
| Lavandería · ventana a calle | PB | 0,80 | 0,75 | 1,10 |
| Puerta baño patio (hoja 0,80 x 1,98) | Patio | 0,85 | 2,05 | -0,23 |
| Puerta bodega (hoja 0,80 x 1,98) | Patio | 0,85 | 2,05 | -0,23 |
| Ventana bodega | Patio | 0,80 | 0,20 | 1,85 |
| Ventana baño patio | Patio | 0,75 | 0,60 | Por medir |

Cotas inferiores referidas al origen común del modelo. En PA no equivalen a antepecho desde su piso.